


CUADRO DE COORDENADAS DE REGISTROS Y CAJAS

PUNTO	PROGRESIVA	ESTE	NORTE	COTA FONDO	COTA TAPA	OBSERVACION
CL	0+000.00	345717.302	9282826.994	259.100	260.600	llegada de CAR Varones y cuneta Eje 01
RS-01	0+011.27	345708.727	9282819.681	259.066	260.600	empalme cuneta Eje 02
RS-02	0+022.00	345700.563	9282812.718	259.034	260.600	limpieza
RS-03	0+032.50	345692.574	9282805.905	259.002	260.600	empalme cuneta Eje 06
RS-04	0+042.68	345684.828	9282799.299	258.972	260.600	empalme cuneta Eje 07
RS-05	0+052.00	345677.737	9282793.251	258.944	260.600	limpieza
RS-06	0+058.81	345672.559	9282788.830	258.924	260.600	quiebre 1 (45 grados) y empalme cuneta Eje 11
RS-07	0+066.89	345671.917	9282780.776	258.899	260.600	
CC	0+066.89	345669.635	9282778.829	258.320	260.600	poza de disipacion y empalme cuneta Eje 12: entrega al R-01 de CAR Mujeres
R-01 (receptor)	0+073.39	345666.974	9282776.560	258.720	259.250	0+000 del tramo CAR Mujeres

Coordenadas UTM WGS84 - Zona 18 Sur. Ubicacion referencial: el plano de arquitectura se georeferencio con el R-01 del CAR Mujeres y el rumbo de su lindero (azimut 49.54); verificar en campo.

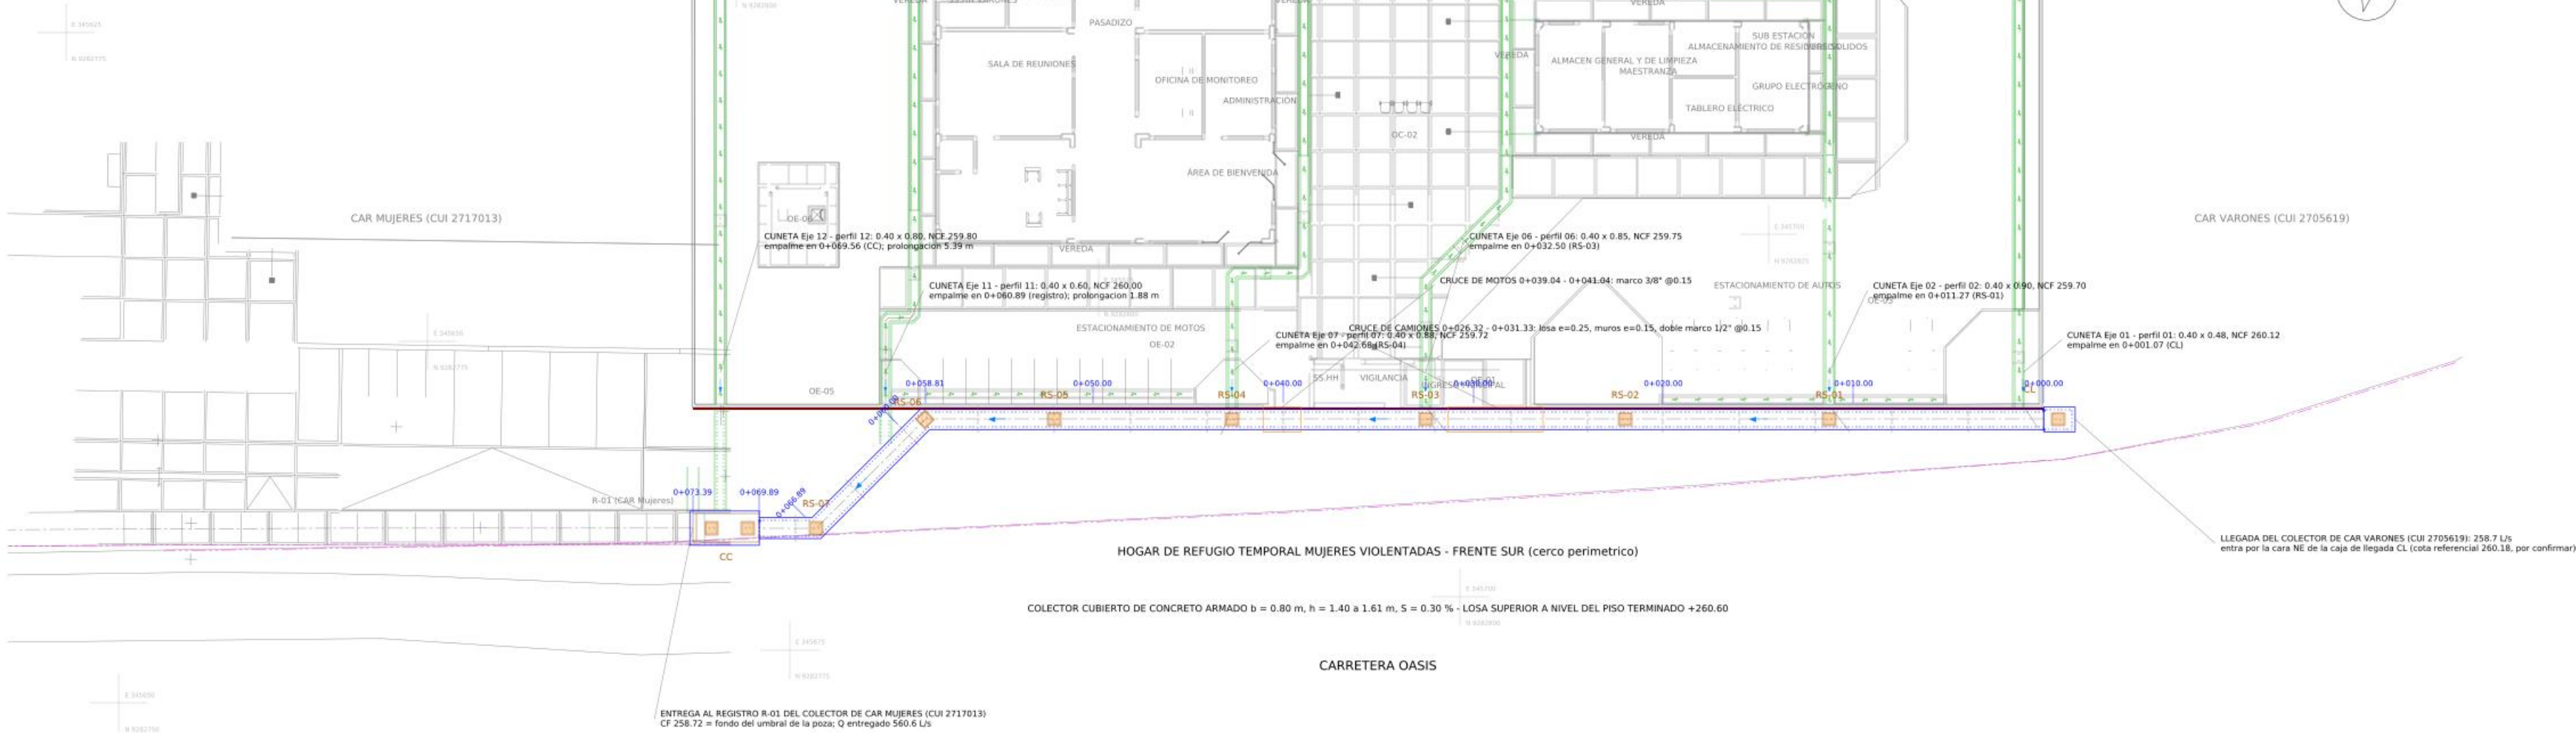


LEYENDA

- muro exterior del colector
- cara interior (bajo losa superior)
- eje del colector
- registro de limpieza con tapa removible
- jointa de dilatacion cada 4.00 m
- cruce vehicular (motos / camiones)
- poza de disipacion (caja de caída)
- cuneta de arquitectura que llega al colector
- cercos perimetricos del predio
- lindero con la Crta. Oasis
- arquitectura (referencia)
- sentido del flujo

NOTAS

- Colector de concreto armado $f_c=210 \text{ kg/cm}^2$, cubierto en todo su recorrido, losa superior vaciada monoliticamente con los muros.
- El colector va por fuera del cerco, dentro del predio: muro lado predio a 0.025 m del cerco (junta de tecnopor de 1"). Eje a 0.575 m del cerco.
- Progresivas a lo largo del eje desde la caja de llegada CL (limite con CAR Varones), crecientes hacia la entrega al CAR Mujeres.
- Registros de limpieza con tapa removible a ras del piso terminado, en cada empalme de cuneta, en los quiebres y cada 12.00 m como maximo.
- Cotas en m.s.n.m. Cara superior de la losa = piso terminado del frente +260.60. Fondo 259.10 (0+000) a 258.89 (brink), $S = 0.30 \%$.
- Cajas: CL de llegada (0+000) con poza de 0.30 m; CC de caída con poza de 0.40 m bajo el fondo del receptor y umbral de salida.
- Las cunetas de arquitectura (perfiles 01 a 12) entran por ventana en el muro lado predio; las de los Ejes 11 y 12 se prolongan fuera del cerco.
- Ver perfil en DP-02 y DP-03, secciones en DP-04 a DP-06, cajas en DP-07, acero y especificaciones en DP-08, isometricos en DP-09 y DP-10.

PROYECTO: CREACION DEL SERVICIO DE ATENCION INTEGRAL A MUJERES VICTIMAS DE VIOLENCIA EN EL HOGAR DE REFUGIO TEMPORAL MUJERES VIOLENTADAS, DISTRITO DE MORALES, PROVINCIA Y DEPARTAMENTO DE SAN MARTIN - CUI N. 2675514		
ENTIDAD: GERENCIA TERRITORIAL BAJO MAYO - TARAPOTO		
UBICACION: PREDIO RURAL LOS MANGOS - MORALES - SAN MARTIN - SAN MARTIN		
ESPECIALIDAD: INSTALACIONES SANITARIAS - DRENAJE PLUVIAL		
PLANO: PLANTA DEL COLECTOR PLUVIAL TRAMO HOGAR DE REFUGIO (0+000.00 - 0+073.39) - TRAZO, REGISTROS, CAJAS Y EMPALME CON CAR MUJERES		
PROYECTISTA: _____ CIP: _____		
ELABORADO: HIDROCONSULT	ESCALA: 1/200	
REVISADO: _____	FECHA: OCT. 2026	LAMINA:
FIRMA Y SELLO:	REVISION: 00	DP-01

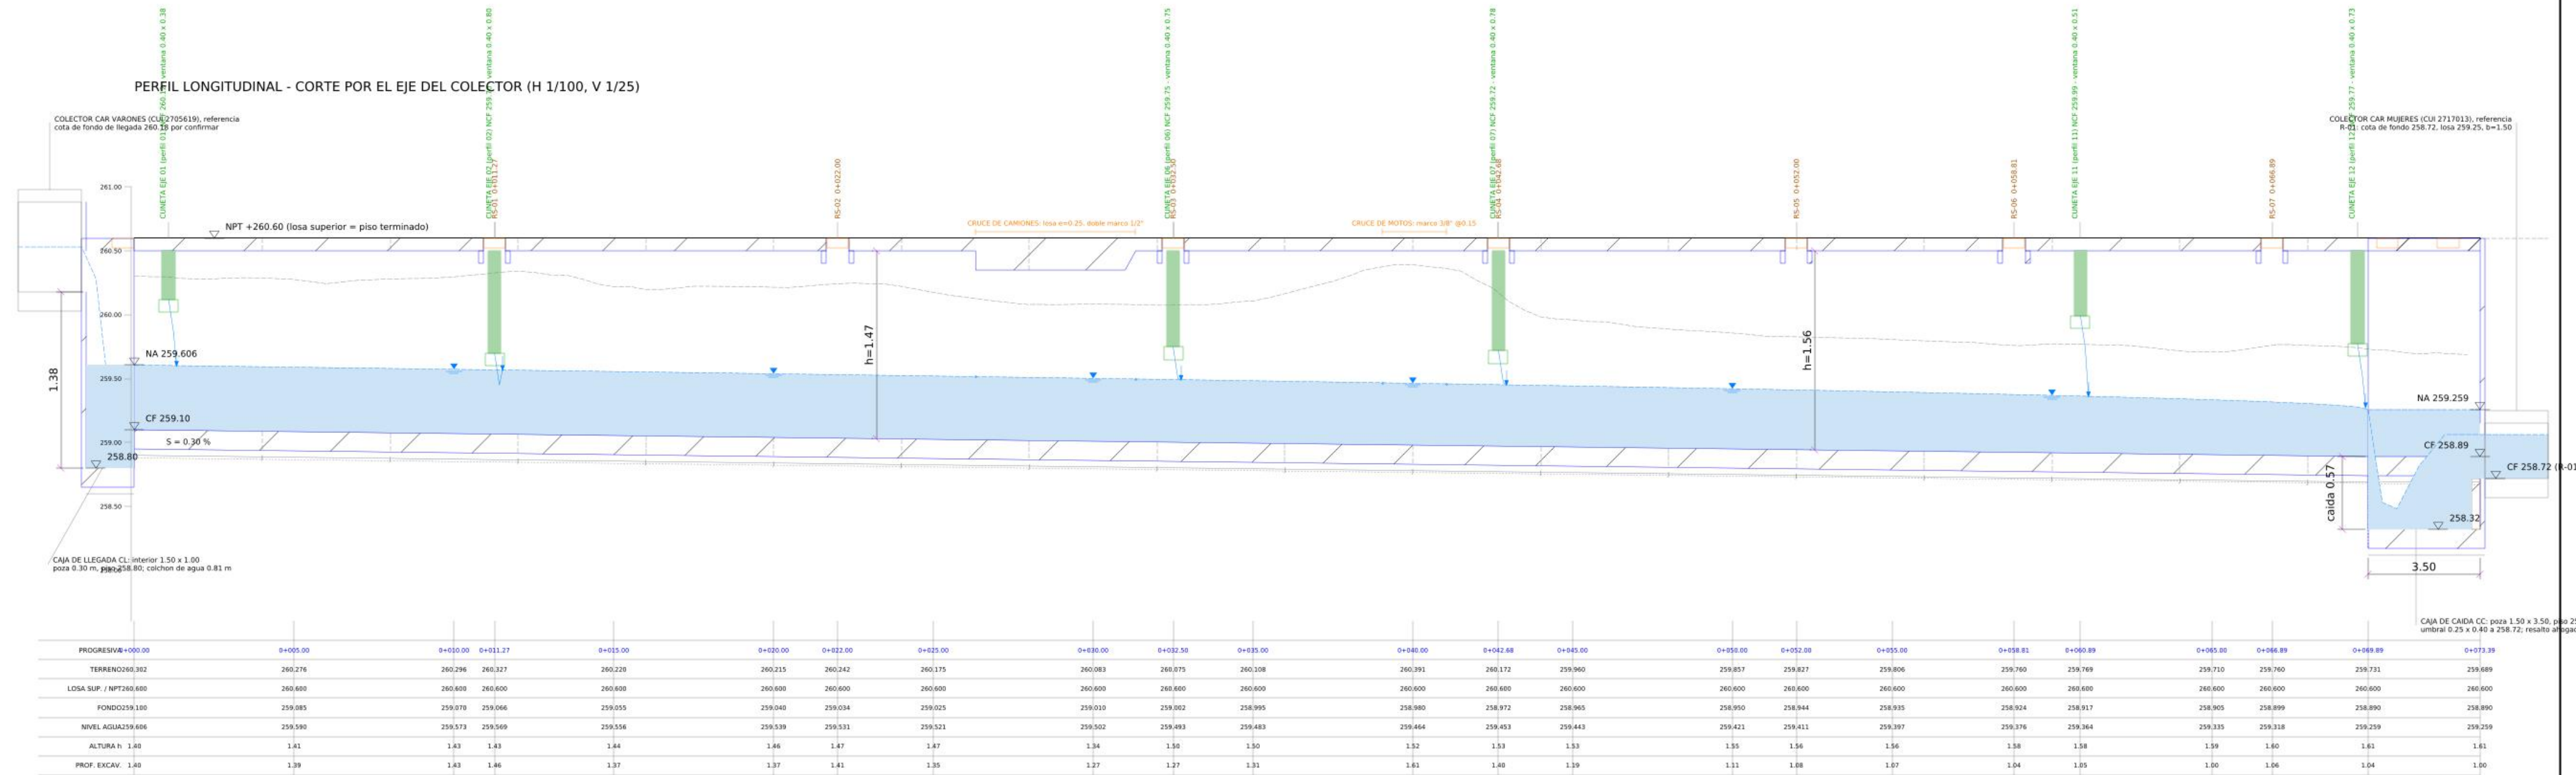


- LEYENDA
- piso terminado / losa superior (NPT +260.60)
 - - - terreno existente (superficie topografica)
 - ▭ concreto armado cortado (losas, cajas)
 - ▭ solado e=0.05 y limite de excavacion
 - ▭ agua: nivel de diseno (Q = 560.6 L/s)
 - ▭ tapa de registro 0.68 x 0.68 x 0.08
 - ▭ ventana de llegada de cuneta 0.40 x H en el muro lado predio
 - ▭ junta de dilatacion cada 4.00 m
 - ▭ umbral de la poza de disipacion
 - ▭ colectores vecinos (referencia)

- NOTAS
- Corte longitudinal por el eje con exageracion vertical x4 (H 1/100, V 1/25). Cotas en m s.n.m. Se ve la cara interior del muro lado predio con las ventanas de las cunetas.
 - El nivel de agua de diseno resulta del calculo de flujo gradualmente variado (memoria de calculo, hoja PERFIL FLUJO); control: tirante critico en la caida libre a la caja CC.
 - Caudal de diseno 560.6 L/s: CAR Varones (258.7 L/s, dato de su memoria) + Hogar de Refugio (301.9 L/s), TR 25 anos. Velocidad 1.35 m/s (autolimpieza, CE.040).
 - Registros con tapa de concreto 0.68 x 0.68 x 0.08, borde engrosado 0.15 x 0.10 y contramarco metalico (DP-06B). No hay registros dentro de los cruces vehiculares.
 - Relleno nivelado del retiro hasta la cota de la losa (+260.60) donde el terreno existente queda por debajo.
 - Ver perfil detallado por tramos (escala real 1/50) en las laminas DP-03A y DP-03B; cajas en DP-07; empalme de cunetas en DP-06C.


PROYECTO: CREACION DEL SERVICIO DE ATENCION INTEGRAL A MUJERES VICTIMAS DE VIOLENCIA EN EL HOGAR DE REFUGIO TEMPORAL MUJERES VIOLENTADAS, DISTRITO DE MORALES, PROVINCIA Y DEPARTAMENTO DE SAN MARTIN - CUI N. 2675514 ENTIDAD: GERENCIA TERRITORIAL BAJO MAYO - TARAPOTO		
UBICACION: PREDIO RURAL LOS MANGOS - MORALES - SAN MARTIN - SAN MARTIN ESPECIALIDAD: INSTALACIONES SANITARIAS - DRENAJE PLUVIAL		
PLANO: PERFIL LONGITUDINAL GENERAL DEL COLECTOR ESCALA H 1/100 - V 1/25 - CORTE POR EL EJE: NIVELES DE DISENO, PERFIL HIDRAULICO, CAJAS, REGISTROS Y EMPALMES (0+000.00 - 0+073.39)		
PROYECTISTA: _____ CIP: _____		
ELABORADO: HIDROCONSULT	ESCALA: 1/200	
REVISADO: _____	FECHA: OCT. 2026	LAMINA: _____
FIRMA Y SELLO: _____	REVISION: 00	DP-02

TRAMO 1: 0+000.00 A 0+020.00

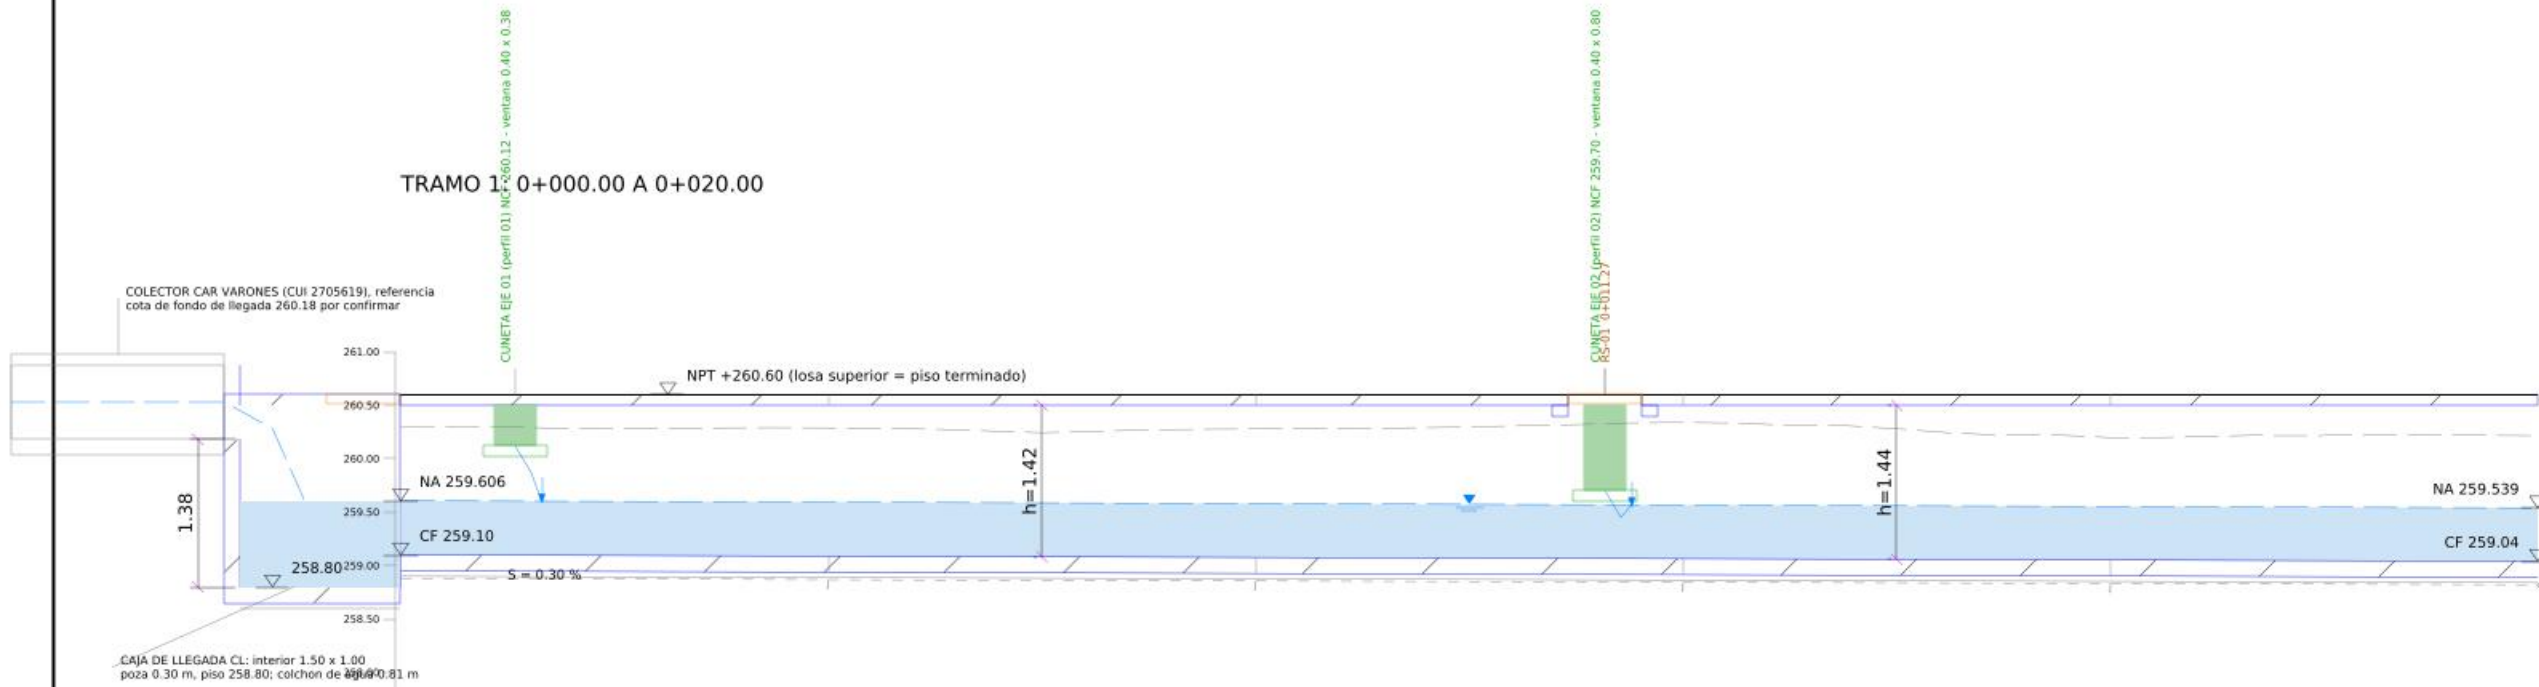

PROGRESIVA	0+000.00	0+005.00	0+010.00	0+011.27	0+015.00	0+020.00
TERRENO	260.382	260.276	260.296	260.327	260.220	260.215
LOSA SUP. / NPT	260.600	260.600	260.600	260.600	260.600	260.600
FONDO	259.100	259.085	259.070	259.066	259.055	259.040
NIVEL AGUA	259.606	259.590	259.573	259.569	259.556	259.539
ALTURA h	1.40	1.41	1.43	1.43	1.44	1.46
PROF. EXCAV.	1.40	1.39	1.43	1.46	1.37	1.37

TRAMO 2: 0+020.00 A 0+040.00

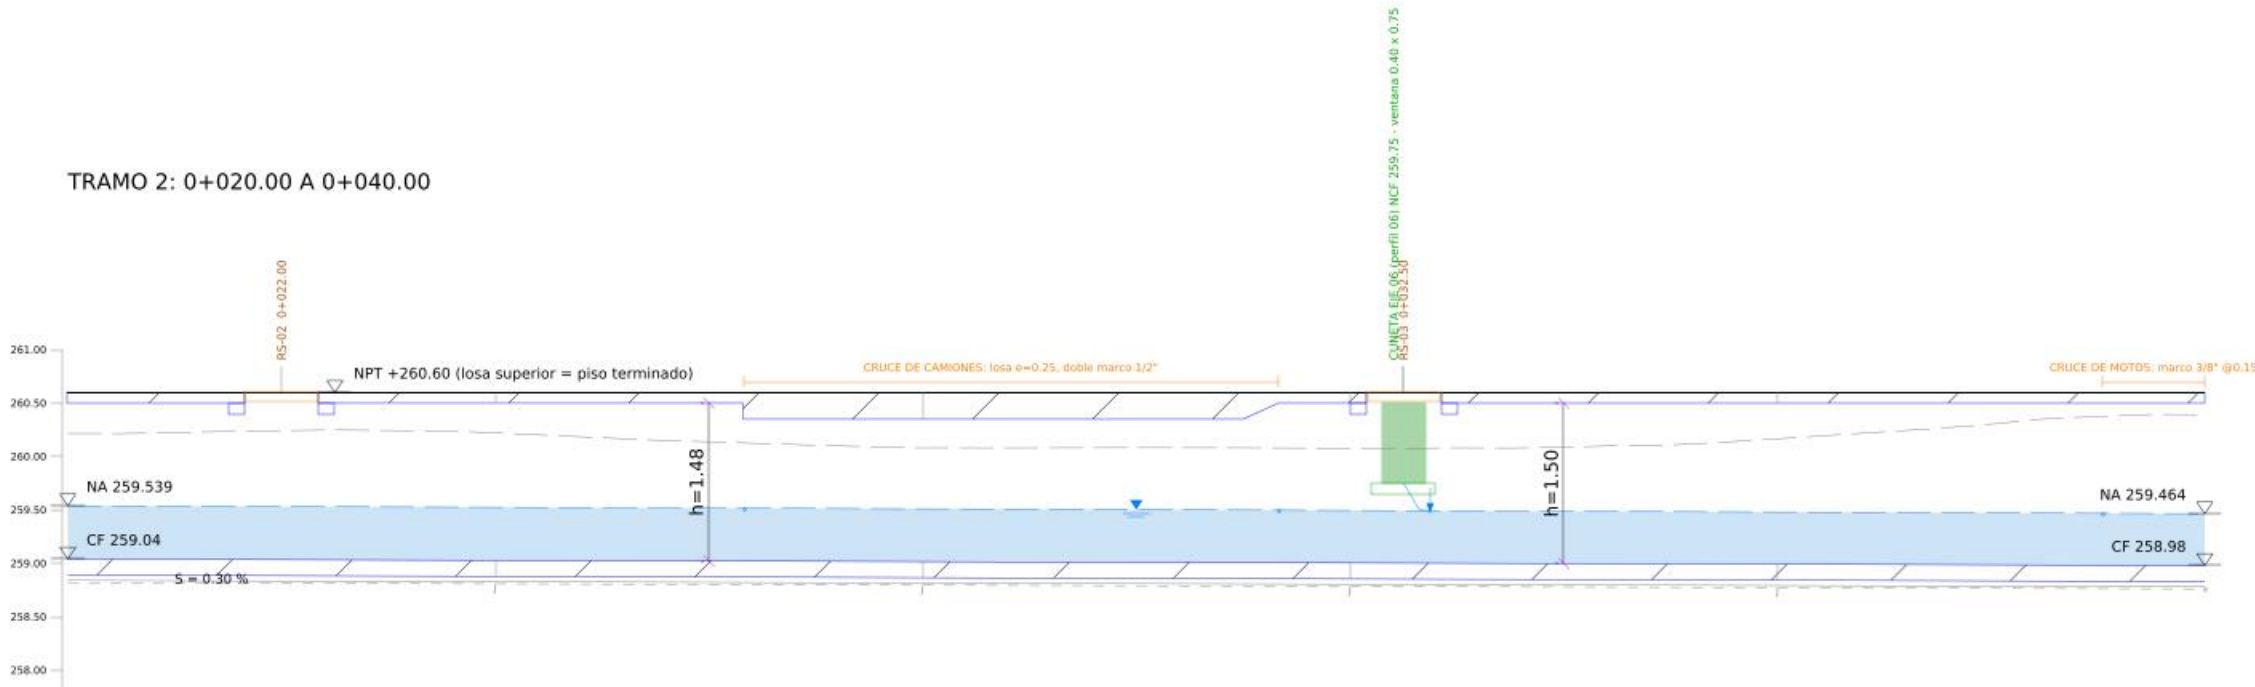

PROGRESIVA	0+020.00	0+025.00	0+030.00	0+032.50	0+035.00	0+040.00
TERRENO	260.215	260.175	260.083	260.075	260.108	260.391
LOSA SUP. / NPT	260.600	260.600	260.600	260.600	260.600	260.600
FONDO	259.040	259.025	259.010	259.002	258.995	258.980
NIVEL AGUA	259.539	259.521	259.502	259.493	259.483	259.464
ALTURA h	1.46	1.47	1.34	1.50	1.50	1.52
PROF. EXCAV.	1.37	1.41	1.27	1.27	1.31	1.61

LEYENDA

- concreto armado cortado
- solado e=0.05
- tapa de registro
- agua (nivel de diseño)
- piso terminado +260.60
- terreno existente
- ventana de llegada de cuneta
- junta de dilatacion cada 4.00 m

NOTAS

- Escala real: horizontal = vertical.
- Cotas en m.s.n.m.; progresivas desde la caja CL.
- Prof. excav. medida desde el terreno existente al fondo del solado.

PROYECTO:
CREACION DEL SERVICIO DE ATENCION INTEGRAL A MUJERES VICTIMAS DE VIOLENCIA EN EL HOGAR DE REFUGIO TEMPORAL
MUJERES VIOLENTADAS, DISTRITO DE MORALES, PROVINCIA Y DEPARTAMENTO DE SAN MARTIN - CUI N. 2675514
ENTIDAD: GERENCIA TERRITORIAL BAJO MAYO - TARAPOTO

UBICACION: PREDIO RURAL LOS MANGOS - MORALES - SAN MARTIN - SAN MARTIN
ESPECIALIDAD: INSTALACIONES SANITARIAS - DRENAJE PLUVIAL

PLANO: PERFIL LONGITUDINAL DETALLADO DEL COLECTOR
TRAMOS 1 Y 2 (0+000.00 - 0+040.00) - ESCALA REAL 1/50 (H = V)

PROYECTISTA: _____ CIP: _____

ELABORADO: HIDROCONSULT

ESCALA: 1/50


REVISADO: _____

FECHA: OCT. 2026 LAMINA:


FIRMA Y SELLO:

REVISION: 00

TRAMO 3: 0+040.00 A 0+060.00

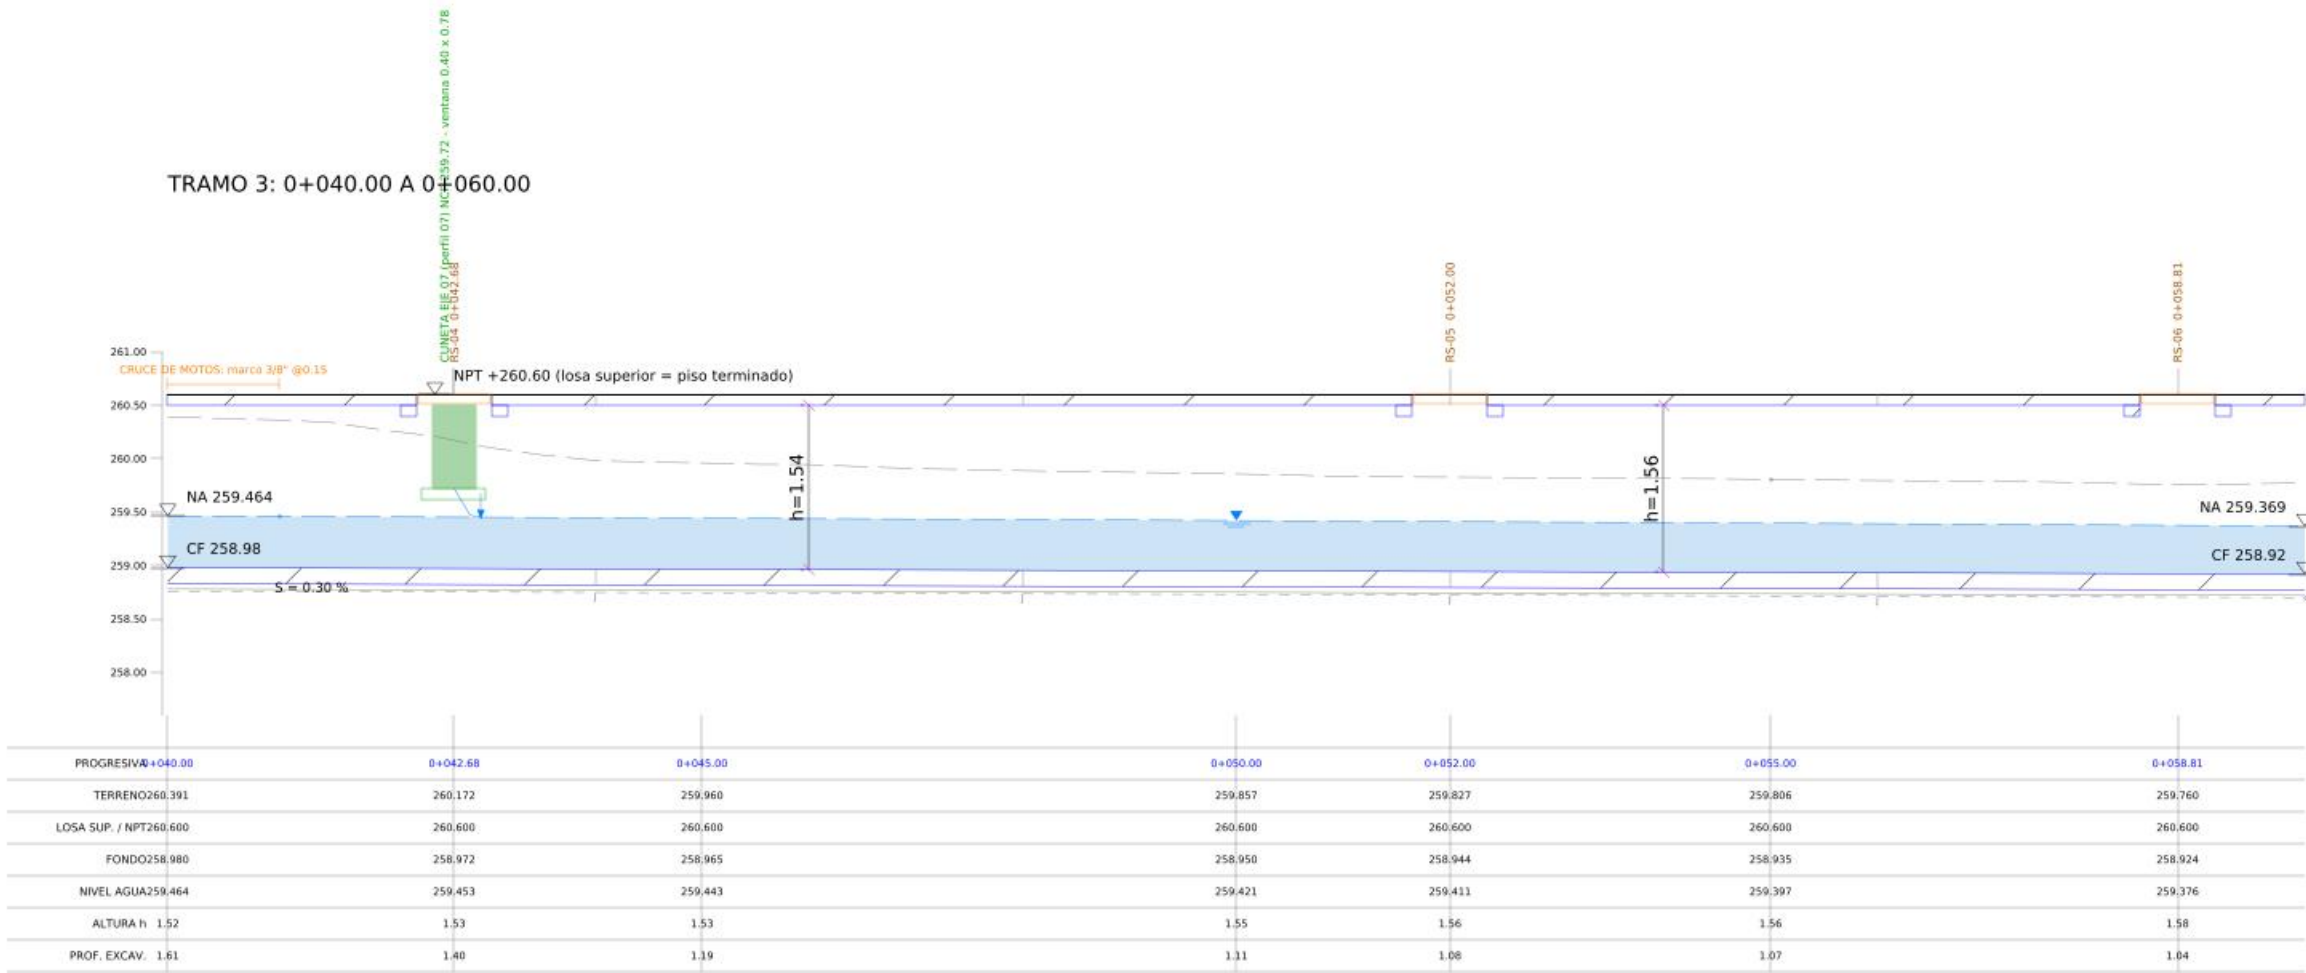

TRAMO 4: 0+060.00 A 0+073.39

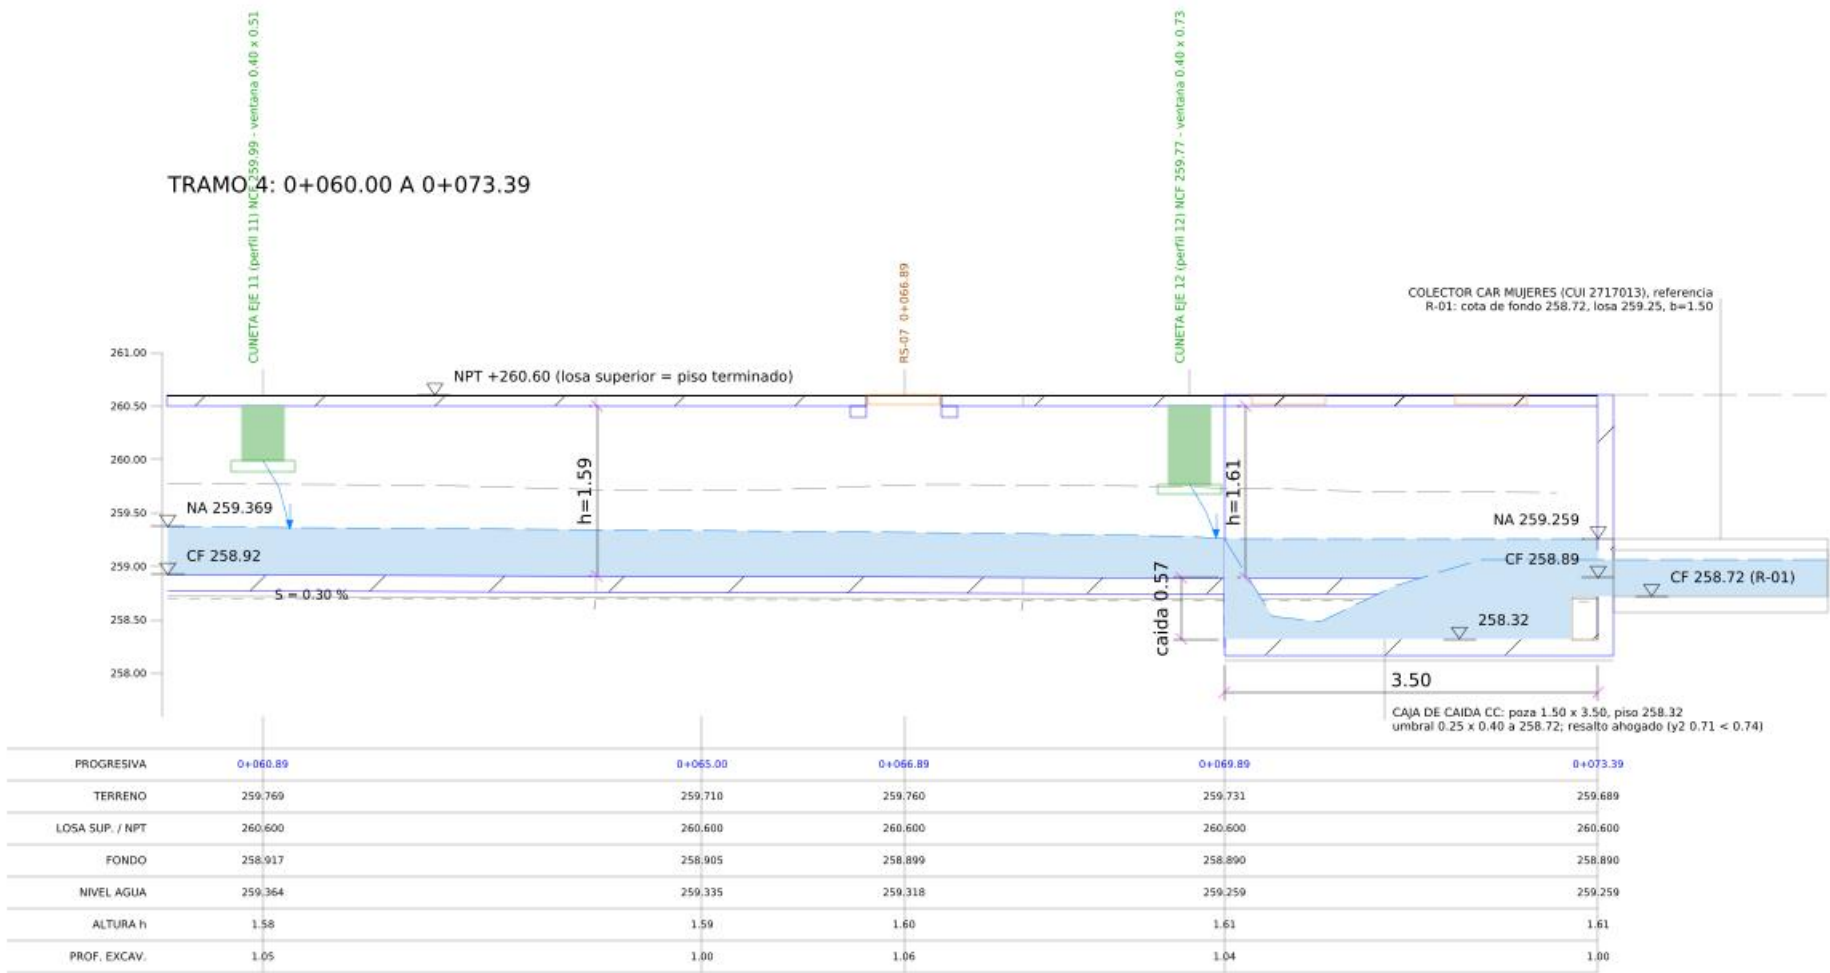


LEYENDA

- concreto armado cortado
- solado e=0.05
- tapa de registro
- agua (nivel de diseño)
- piso terminado +260.60
- terreno existente
- ventana de llegada de cuneta
- junta de dilatacion cada 4.00 m

NOTAS


- Escala real: horizontal = vertical.
- Cotas en m.s.n.m.; progresivas desde la caja CL.
- Prof. excav. medida desde el terreno existente al fondo del solado.

PROYECTO: CREACION DEL SERVICIO DE ATENCION INTEGRAL A MUJERES VICTIMAS DE VIOLENCIA EN EL HOGAR DE REFUGIO TEMPORAL MUJERES VIOLENTADAS, DISTRITO DE MORALES, PROVINCIA Y DEPARTAMENTO DE SAN MARTIN - CUI N. 2675514 ENTIDAD: GERENCIA TERRITORIAL BAJO MAYO - TARAPOTO		
UBICACION: PREDIO RURAL LOS MANGOS - MORALES - SAN MARTIN - SAN MARTIN ESPECIALIDAD: INSTALACIONES SANITARIAS - DRENAJE PLUVIAL		
PLANO: PERFIL LONGITUDINAL DETALLADO DEL COLECTOR TRAMOS 3 Y 4 (0+040.00 - 0+073.39) - ESCALA REAL 1/50 (H = V)		
PROYECTISTA: _____ CIP: _____		
ELABORADO: HIDROCONSULT	ESCALA: 1/50	
REVISADO: _____	FECHA: OCT. 2026	LAMINA: _____
FIRMA Y SELLO: _____	REVISION: 00	DP-03E

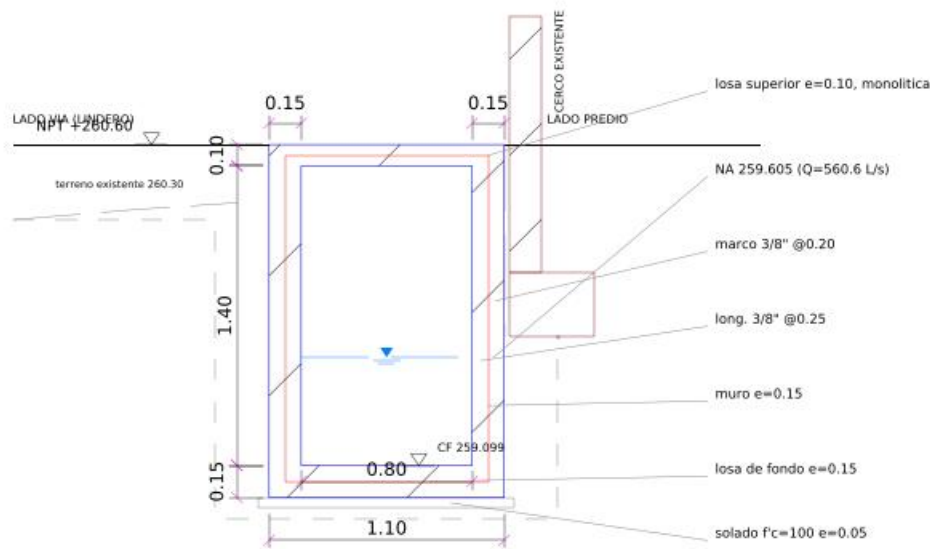


SECCION S-01

PROG. 0+000.50 - CF 259.099 - TRAMO NORMAL - ESC. 1/25

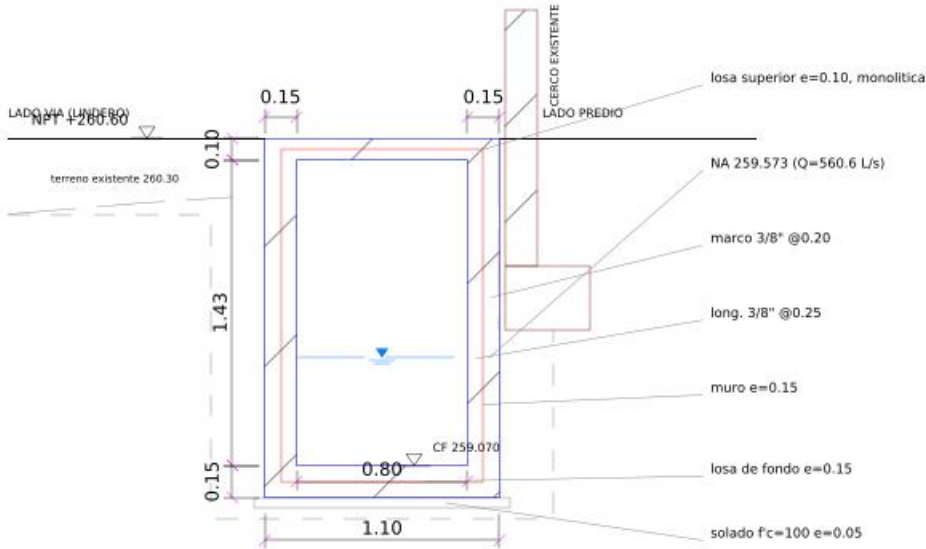


SECCION S-02

PROG. 0+010.00 - CF 259.070 - TRAMO NORMAL - ESC. 1/25

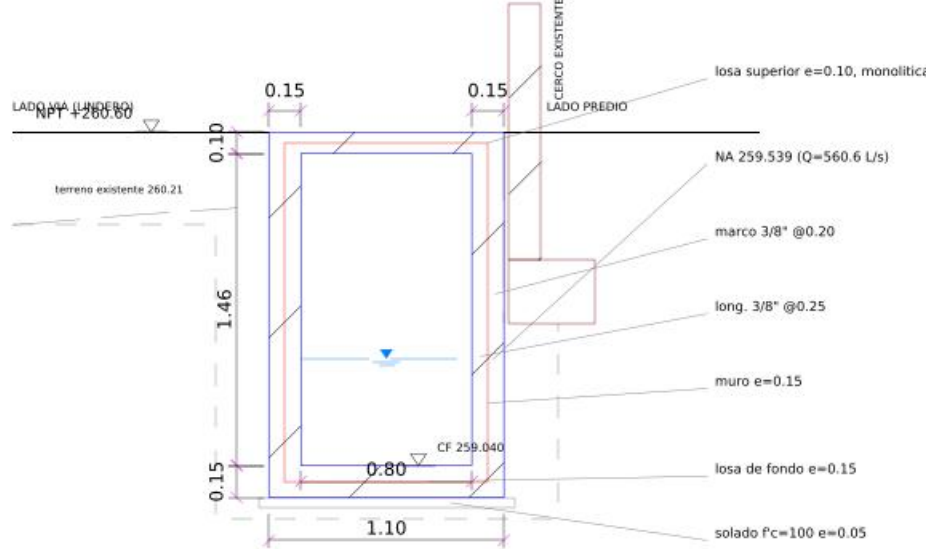

SECCION S-03

PROG. 0+020.00 - CF 259.040 - TRAMO NORMAL - ESC. 1/25

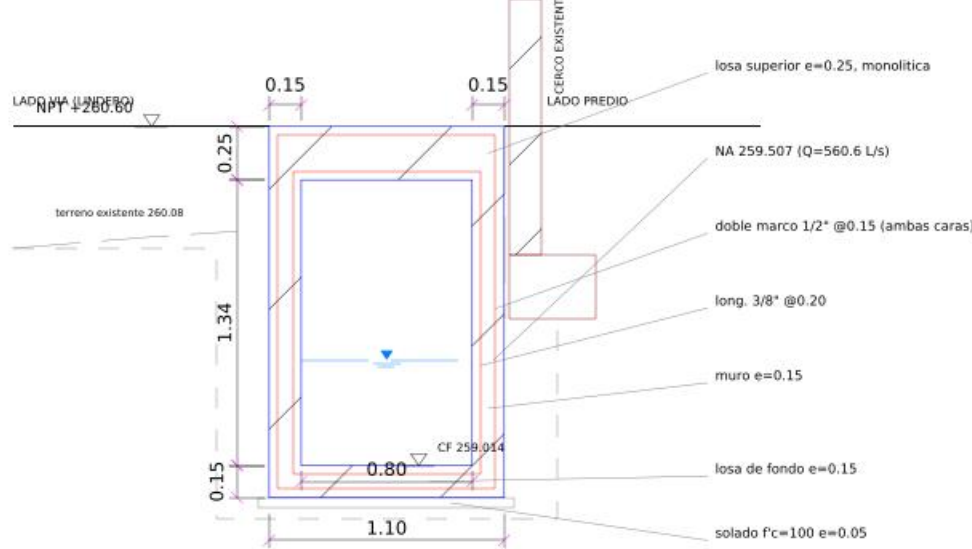

SECCION S-04

PROG. 0+028.80 - CF 259.014 - CRUCE DE CAMIONES - ESC. 1/25


LEYENDA

- concreto armado $f'c=210$ kg/cm²
- solado $f'c=100$ kg/cm²
- acero transversal: marco cerrado (rojo)
- acero longitudinal (verde)
- nivel de agua de diseno
- piso terminado +260.60
- terreno existente
- limite de excavacion
- cercos perimetricos existentes

NOTAS


- Altura interior h segun el perfil longitudinal (1.40 m en 0+000 a 1.61 m en el brink).
- Tramo normal y cruce de motos: un solo marco cerrado en el eje de muros y losas (una capa, E.060.14.3.4); recubrimiento minimo 0.04 m en muros y losa de fondo y 0.025 m en la losa superior.
- Junta de tecnopor de 1" entre el muro lado predio y el cimientto del cerco; junta de 1" entre la losa superior y el piso adyacente.
- El cruce de camiones (S-04) lleva losas $e=0.25$ y doble marco de 1/2" @0.15 (marco exterior e interior, recubrimiento 0.04); el cruce de motos (S-05) marco unico de 3/8" @0.15.
- Los registros no se ubican dentro de los cruces vehiculares.

PROYECTO: CREACION DEL SERVICIO DE ATENCION INTEGRAL A MUJERES VICTIMAS DE VIOLENCIA EN EL HOGAR DE REFUGIO TEMPORAL MUJERES VIOLENTADAS, DISTRITO DE MORALES, PROVINCIA Y DEPARTAMENTO DE SAN MARTIN - CUI N. 2675514 ENTIDAD: GERENCIA TERRITORIAL BAJO MAYO - TARAPOTO		
UBICACION: PREDIO RURAL LOS MANGOS - MORALES - SAN MARTIN - SAN MARTIN ESPECIALIDAD: INSTALACIONES SANITARIAS - DRENAJE PLUVIAL		
PLANO: SECCIONES TRANSVERSALES DEL COLECTOR SECCIONES S-01 A S-04 CON DISTRIBUCION DE ACERO - ESC. 1/25		
PROYECTISTA: _____ CIP: _____		
ELABORADO: HIDROCONSULT	ESCALA: 1/25	
REVISADO: _____	FECHA: OCT. 2026	LAMINA: _____
FIRMA Y SELLO: _____	REVISION: 00	

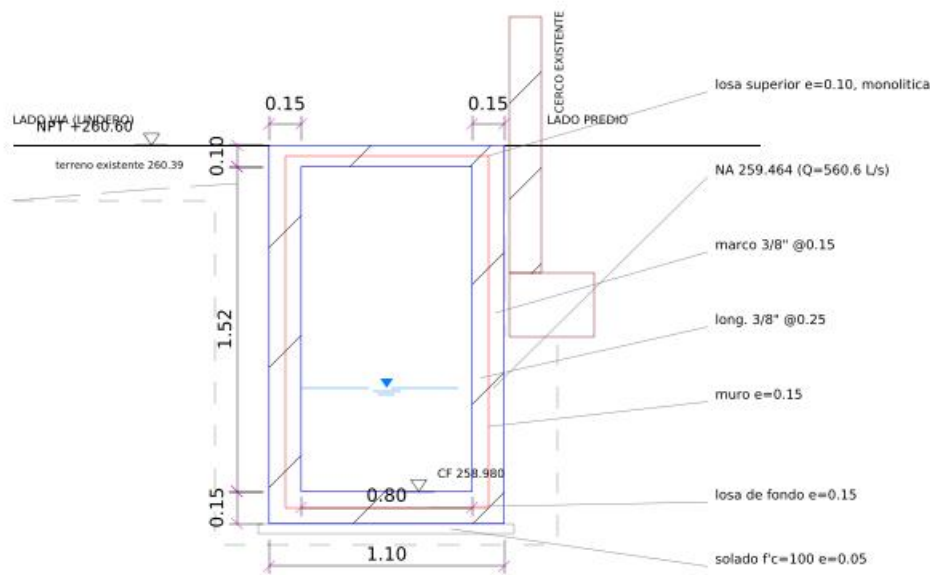


SECCION S-05

PROG. 0+040.00 - CF 258.980 - CRUCE DE MOTOS - ESC. 1/25

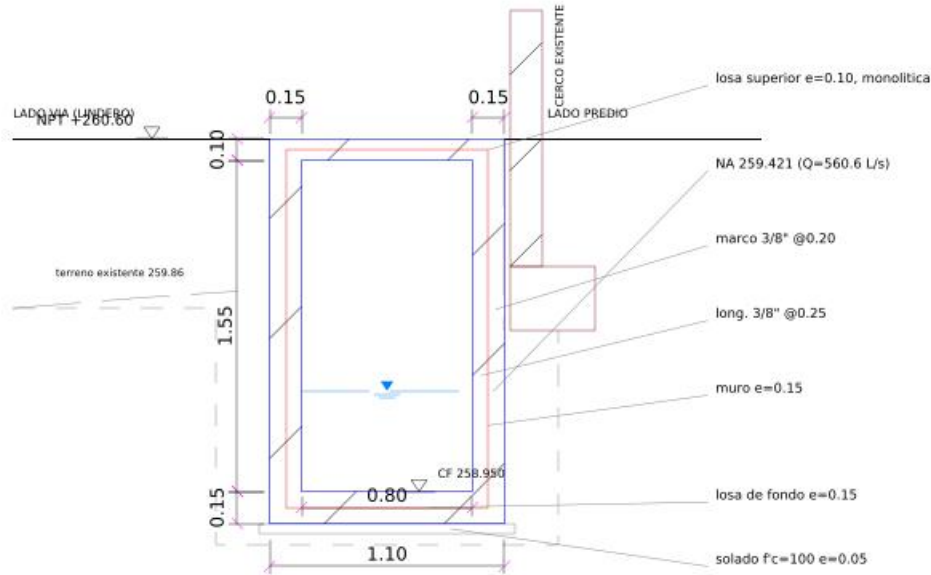


SECCION S-06

PROG. 0+050.00 - CF 258.950 - TRAMO NORMAL - ESC. 1/25

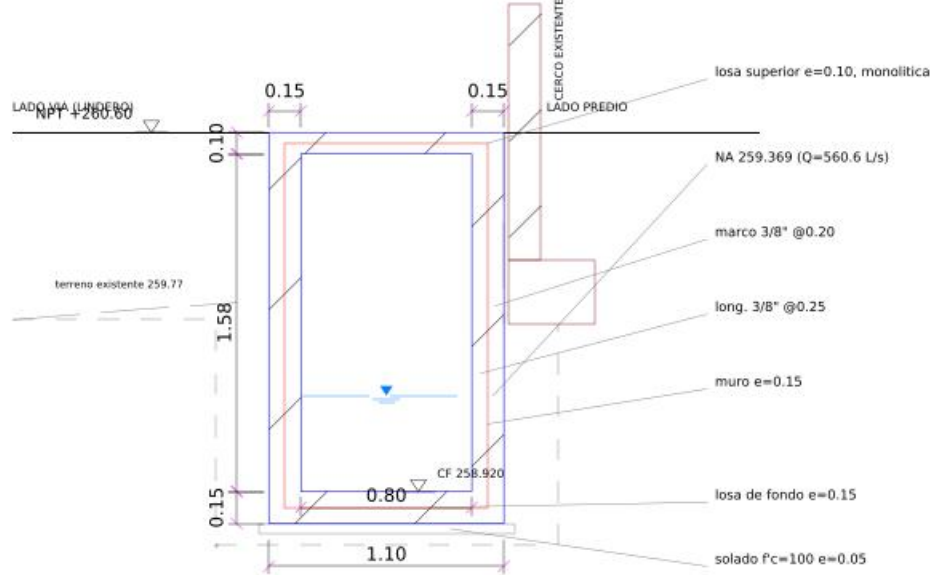

SECCION S-07

PROG. 0+060.00 - CF 258.920 - TRAMO NORMAL - ESC. 1/25

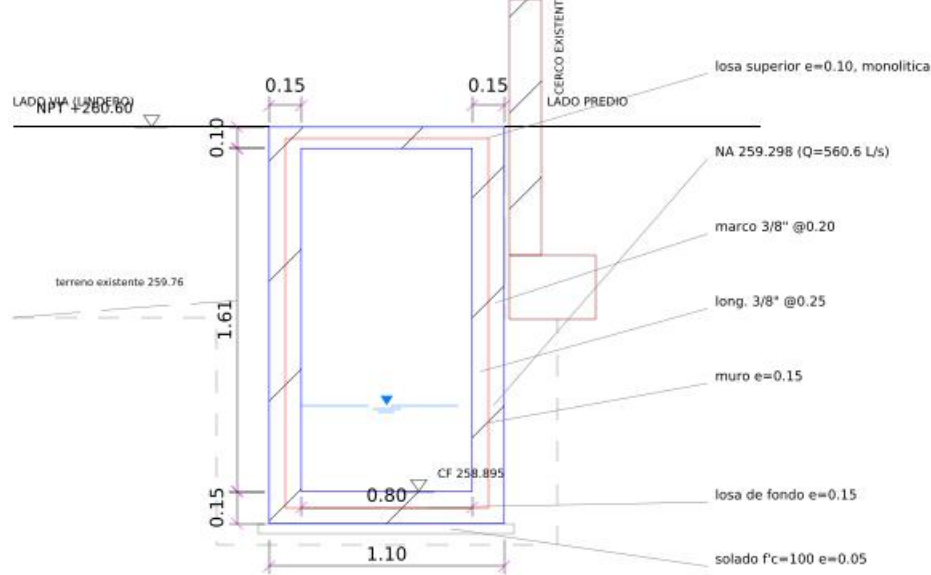

SECCION S-08

PROG. 0+068.50 - CF 258.895 - TRAMO NORMAL - ESC. 1/25


LEYENDA

- concreto armado $f'c=210$ kg/cm²
- solado $f'c=100$ kg/cm²
- acero transversal: marco cerrado (rojo)
- acero longitudinal (verde)
- nivel de agua de diseno
- piso terminado +260.60
- terreno existente
- limite de excavacion
- cercos perimetricos existentes

NOTAS

- Altura interior h segun el perfil longitudinal (1.40 m en 0+000 a 1.61 m en el brink).
- Tramo normal y cruce de motos: un solo marco cerrado en el eje de muros y losas (una capa, E.060.14.3.4); recubrimiento minimo 0.04 m en muros y losa de fondo y 0.025 m en la losa superior.
- Junta de tecnopor de 1" entre el muro lado predio y el cimientto del cerco; junta de 1" entre la losa superior y el piso adyacente.
- El cruce de camiones (S-04) lleva losas $e=0.25$ y doble marco de 1/2" @0.15 (marco exterior e interior, recubrimiento 0.04); el cruce de motos (S-05) marco unico de 3/8" @0.15.
- Los registros no se ubican dentro de los cruces vehiculares.


PROYECTO: CREACION DEL SERVICIO DE ATENCION INTEGRAL A MUJERES VICTIMAS DE VIOLENCIA EN EL HOGAR DE REFUGIO TEMPORAL MUJERES VIOLENTADAS, DISTRITO DE MORALES, PROVINCIA Y DEPARTAMENTO DE SAN MARTIN - CUI N. 2675514 ENTIDAD: GERENCIA TERRITORIAL BAJO MAYO - TARAPOTO		
UBICACION: PREDIO RURAL LOS MANGOS - MORALES - SAN MARTIN - SAN MARTIN ESPECIALIDAD: INSTALACIONES SANITARIAS - DRENAJE PLUVIAL		
PLANO: SECCIONES TRANSVERSALES DEL COLECTOR SECCIONES S-05 A S-08 CON DISTRIBUCION DE ACERO - ESC. 1/25		
PROYECTISTA: _____ CIP: _____		
ELABORADO: HIDROCONSULT	ESCALA: 1/25	
REVISADO: _____	FECHA: OCT. 2026	LAMINA:
FIRMA Y SELLO:	REVISION: 00	

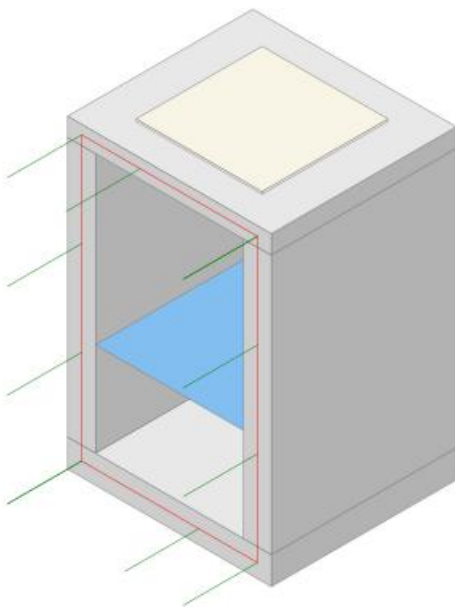

CF 259.099
losa superior 260.60
NA 259.605
marco 3/8" @0.20
long. 3/8" @0.25
registro: tapa 0.68 x 0.68, luz 0.60
h interior 1.40 m

ISOMETRICO S-01


PROG. 0+000.50 - interior 0.80 x 1.40 m - TRAMO NORMAL

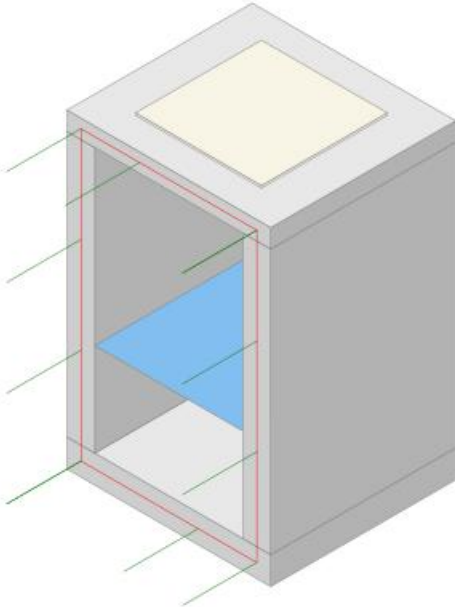

CF 259.070
losa superior 260.60
NA 259.573
marco 3/8" @0.20
long. 3/8" @0.25
registro: tapa 0.68 x 0.68, luz 0.60
h interior 1.43 m

ISOMETRICO S-02


PROG. 0+010.00 - interior 0.80 x 1.43 m - TRAMO NORMAL

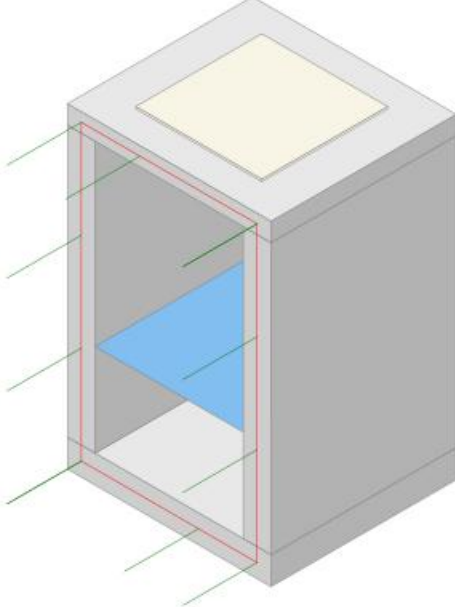

CF 259.040
losa superior 260.60
NA 259.539
marco 3/8" @0.20
long. 3/8" @0.25
registro: tapa 0.68 x 0.68, luz 0.60
h interior 1.46 m

ISOMETRICO S-03

PROG. 0+020.00 - interior 0.80 x 1.46 m - TRAMO NORMAL

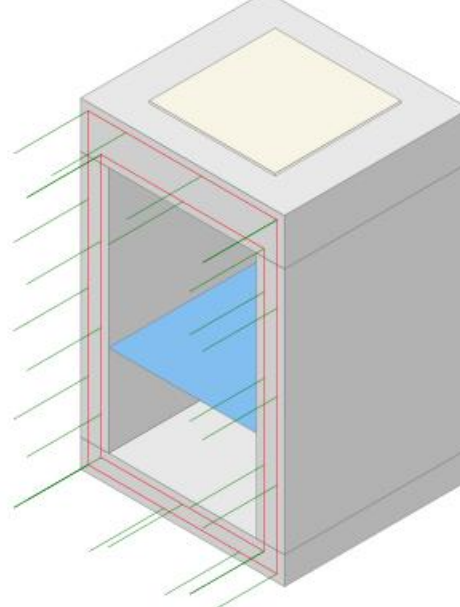

CF 259.014
losa superior 260.60
NA 259.507
doble marco 1/2" @0.15
long. 3/8" @0.20
registro: tapa 0.68 x 0.68, luz 0.60
h interior 1.34 m

ISOMETRICO S-04

PROG. 0+028.80 - interior 0.80 x 1.34 m - CRUCE DE CAMIONES

LEYENDA

- concreto armado (cara superior)
- concreto armado (cara frontal / corte)
- concreto armado (cara lateral)
- tapa de registro removible
- agua (nivel de diseno)
- acero en la cara de corte

NOTAS

- Vistas isometricas sin escala; medidas reales en las laminas DP-04 y DP-06.
- Se muestra 1.00 m de colector cortado en la progresiva indicada.

PROYECTO:
CREACION DEL SERVICIO DE ATENCION INTEGRAL A MUJERES VICTIMAS DE VIOLENCIA EN EL HOGAR DE REFUGIO TEMPORAL
MUJERES VIOLENTADAS, DISTRITO DE MORALES, PROVINCIA Y DEPARTAMENTO DE SAN MARTIN - CUI N. 2675514
ENTIDAD: GERENCIA TERRITORIAL BAJO MAYO - TARAPOTO

UBICACION: PREDIO RURAL LOS MANGOS - MORALES - SAN MARTIN - SAN MARTIN
ESPECIALIDAD: INSTALACIONES SANITARIAS - DRENAJE PLUVIAL

PLANO: ISOMETRICOS DE LAS SECCIONES TRANSVERSALES
SECCIONES S-01 A S-04 - TRAMOS DE 1.00 m CON REGISTRO Y ACERO EN LA CARA DE CORTE

PROYECTISTA: _____ CIP: _____

ELABORADO: HIDROCONSULT

ESCALA: 1/25

REVISADO: _____


FECHA: OCT. 2026

LAMINA:

FIRMA Y SELLO:

REVISION: 00


DP-05A

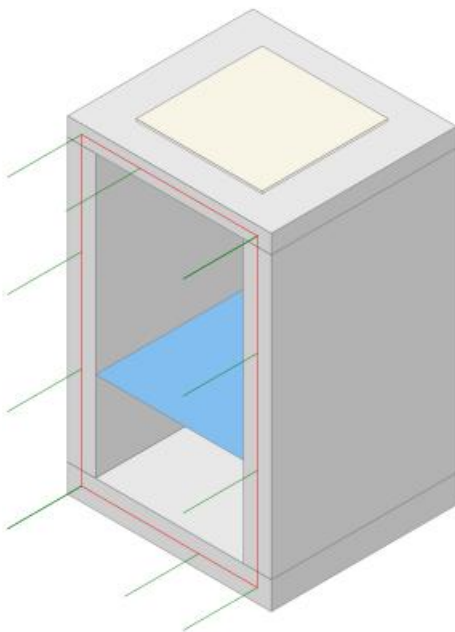

CF 258.980
losa superior 260.60
NA 259.464
marco 3/8" @0.15
long. 3/8" @0.25
registro: tapa 0.68 x 0.68, luz 0.60
h interior 1.52 m

ISOMETRICO S-05


PROG. 0+040.00 - interior 0.80 x 1.52 m - CRUCE DE MOTOS

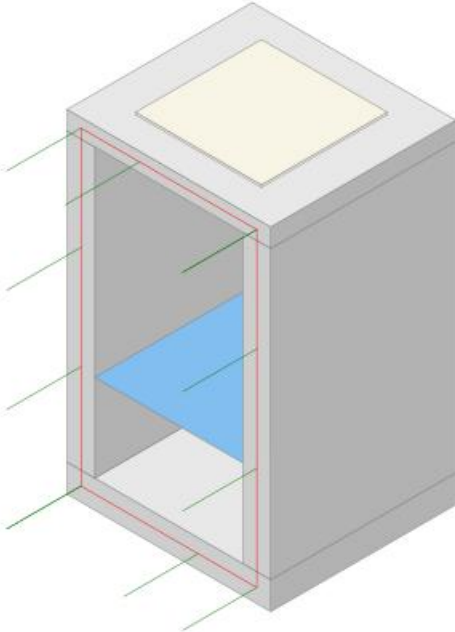

CF 258.950
losa superior 260.60
NA 259.421
marco 3/8" @0.20
long. 3/8" @0.25
registro: tapa 0.68 x 0.68, luz 0.60
h interior 1.55 m

ISOMETRICO S-06


PROG. 0+050.00 - interior 0.80 x 1.55 m - TRAMO NORMAL

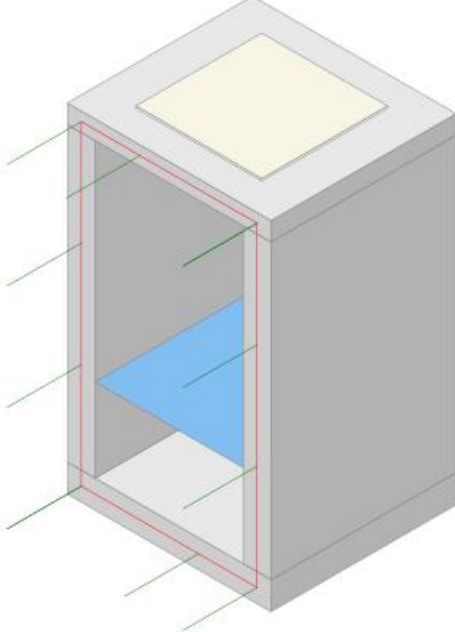

CF 258.920
losa superior 260.60
NA 259.369
marco 3/8" @0.20
long. 3/8" @0.25
registro: tapa 0.68 x 0.68, luz 0.60
h interior 1.58 m

ISOMETRICO S-07

PROG. 0+060.00 - interior 0.80 x 1.58 m - TRAMO NORMAL

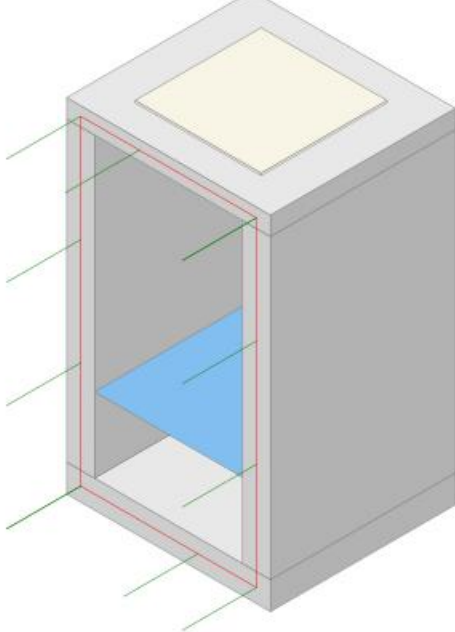

CF 258.895
losa superior 260.60
NA 259.298
marco 3/8" @0.20
long. 3/8" @0.25
registro: tapa 0.68 x 0.68, luz 0.60
h interior 1.61 m

ISOMETRICO S-08

PROG. 0+068.50 - interior 0.80 x 1.61 m - TRAMO NORMAL


LEYENDA

- concreto armado (cara superior)
- concreto armado (cara frontal / corte)
- concreto armado (cara lateral)
- tapa de registro removible
- agua (nivel de diseno)
- acero en la cara de corte

NOTAS

- Vistas isometricas sin escala; medidas reales en las laminas DP-04 y DP-06.
- Se muestra 1.00 m de colector cortado en la progresiva indicada.

PROYECTO: CREACION DEL SERVICIO DE ATENCION INTEGRAL A MUJERES VICTIMAS DE VIOLENCIA EN EL HOGAR DE REFUGIO TEMPORAL MUJERES VIOLENTADAS, DISTRITO DE MORALES, PROVINCIA Y DEPARTAMENTO DE SAN MARTIN - CUI N. 2675514 ENTIDAD: GERENCIA TERRITORIAL BAJO MAYO - TARAPOTO		
UBICACION: PREDIO RURAL LOS MANGOS - MORALES - SAN MARTIN - SAN MARTIN ESPECIALIDAD: INSTALACIONES SANITARIAS - DRENAJE PLUVIAL		
PLANO: ISOMETRICOS DE LAS SECCIONES TRANSVERSALES SECCIONES S-05 A S-08 - TRAMOS DE 1.00 m CON REGISTRO Y ACERO EN LA CARA DE CORTE		
PROYECTISTA: _____ CIP: _____		
ELABORADO: HIDROCONSULT	ESCALA: 1/25	
REVISADO: _____	FECHA: OCT. 2026	LAMINA:
FIRMA Y SELLO:	REVISION: 00	

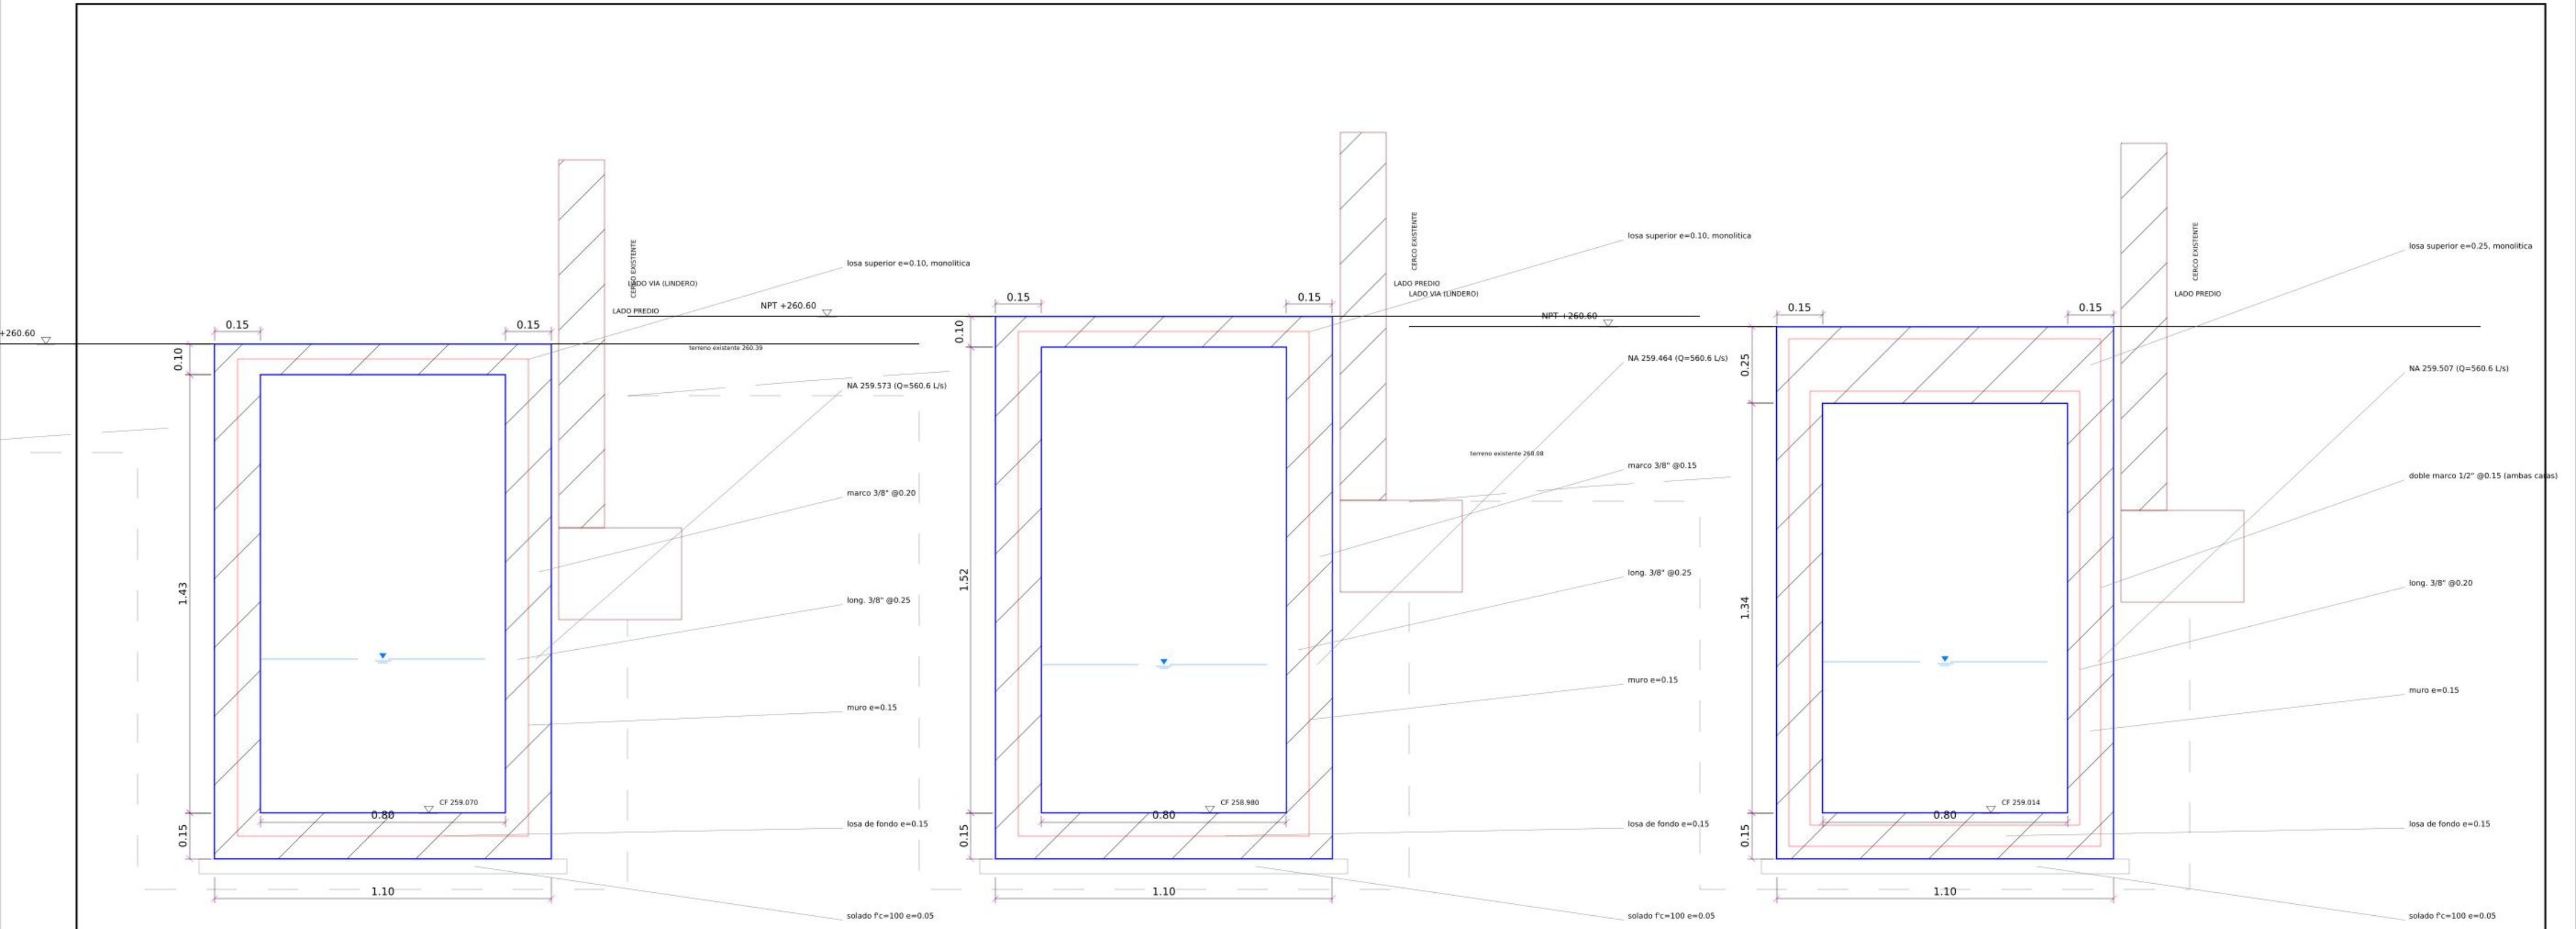

SECCION TIPICA A-A: TRAMO NORMAL

ESC. 1/10 - h segun perfil (aqui 1.43 m, prog. 0+010.00)

SECCION TIPICA B-B: CRUCE DE MOTOS

ESC. 1/10 - h segun perfil (aqui 1.52 m, prog. 0+040.00)

SECCION TIPICA C-C: CRUCE DE CAMIONES

ESC. 1/10 - h segun perfil (aqui 1.34 m, prog. 0+028.80)


LEYENDA

- concreto armado $f'c=210$ kg/cm²
- solado $f'c=100$ kg/cm² $e=0.05$
- acero transversal: marco cerrado (rojo)
- acero longitudinal (verde), sobresale 0.40 de traslape
- nivel de agua de disenno
- cercos perimetricos existentes
- jointa de tecnopor 1"

NOTAS

- Muros $e=0.15$ en todo el tramo; losa de fondo $e=0.15$; losa superior $e=0.10$ ($e=0.25$ en el cruce de camiones).
- Tramo normal y motos: marco unico en el eje de la seccion. En el cruce de camiones el acero va en ambas caras (doble marco 1/2" @0.15) y la losa superior es $e=0.25$.
- El tramo diagonal (quiebres a 45 grados) tiene la seccion tipica A-A; en las esquinas las barras llevan ganchos de 0.40 m (ver DP-09).
- Empalme de las cunetas: ver DP-06C. Registro, tapa y junta: ver DP-06B.


PROYECTO: CREACION DEL SERVICIO DE ATENCION INTEGRAL A MUJERES VICTIMAS DE VIOLENCIA EN EL HOGAR DE REFUGIO TEMPORAL MUJERES VIOLENTADAS, DISTRITO DE MORALES, PROVINCIA Y DEPARTAMENTO DE SAN MARTIN - CUI N. 2675514 ENTIDAD: GERENCIA TERRITORIAL BAJO MAYO - TARAPOTO		
UBICACION: PREDIO RURAL LOS MANGOS - MORALES - SAN MARTIN - SAN MARTIN ESPECIALIDAD: INSTALACIONES SANITARIAS - DRENAJE PLUVIAL		
PLANO: DETALLES TIPICOS DEL COLECTOR SECCIONES TIPICAS: TRAMO NORMAL, CRUCE DE MOTOS, CRUCE DE CAMIONES Y TRAMO DIAGONAL - ESC. 1/10		
PROYECTISTA: _____ CIP: _____		
ELABORADO: HIDROCONSULT	ESCALA: 1/10	
REVISADO: _____	FECHA: OCT. 2026	LAMINA:
FIRMA Y SELLO:	REVISION: 00	

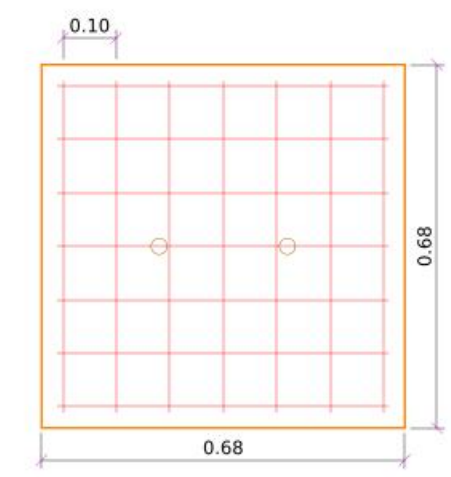


7 + 7 barras 3/8" @0.10, L=0.62; asas 3/8" liso



concreto $f'c=210 \text{ kg/cm}^2$ - peso aprox. 95 kg

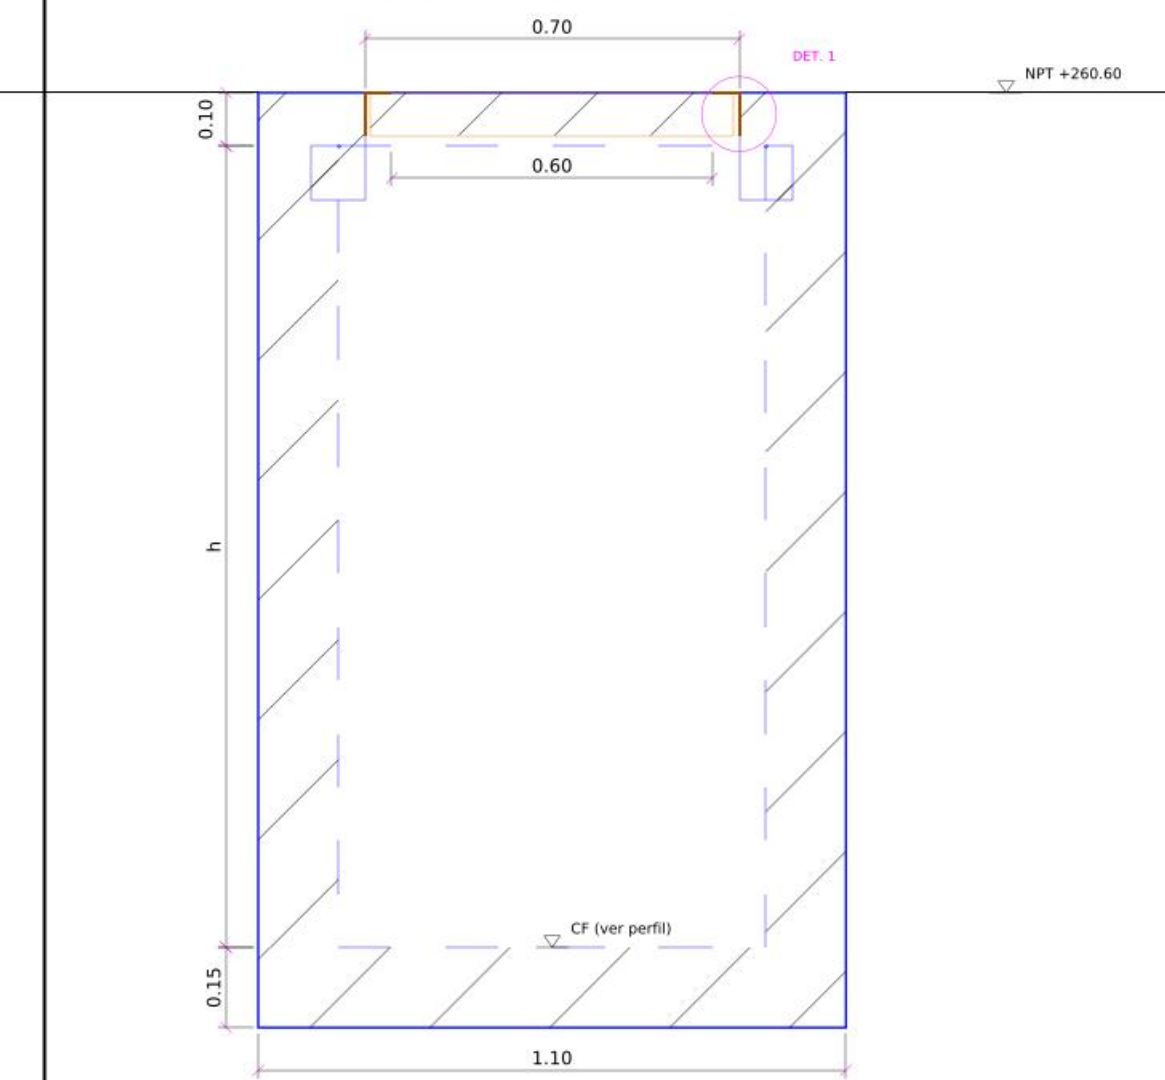

ESC. 1/10

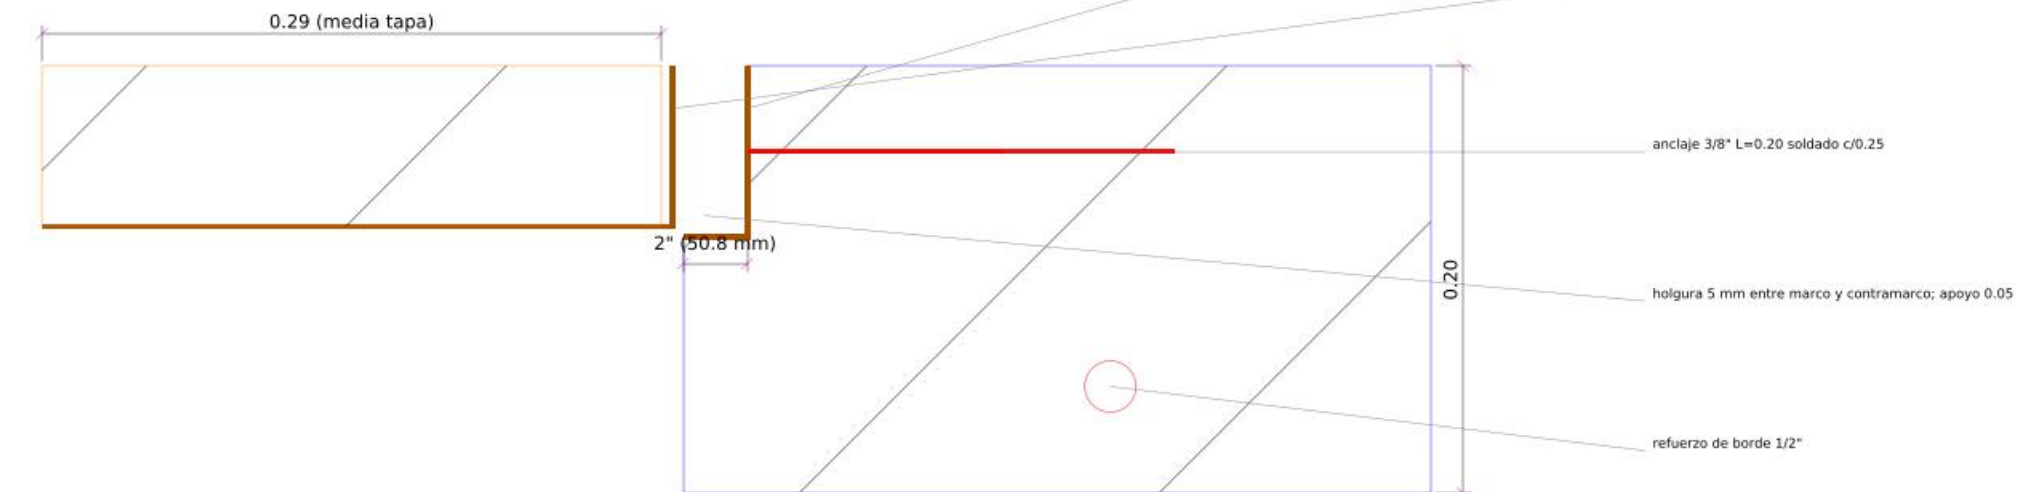


ESC. 1/2.5

Contramarco ángulo L 2"x3"x3/16": 4 x 0.70 = 2.80 m (10.2 kg); anclajes 3/8" L=0.20: 8 und
Marco de tapa ángulo L 1 1/2"x1 1/2"x1/8": 4 x 0.68 = 2.72 m (5.0 kg)
Acero tapa 3/8" @0.10: 14 x 0.62 = 8.68 m (4.9 kg); asas 3/8" liso: 2 x 0.40 m
Concreto tapa f'c=210: 0.68 x 0.68 x 0.08 = 0.037 m3
Refuerzo de borde 1/2": 8 x 1.40 = 11.20 m (11.3 kg); borde engrosado: perímetro 3.00 x 0.15 x 0.10 = 0.045 m3

 concreto armado $f_c = 210 \text{ kg/cm}^2$
 angulos metalicos (marco y contramarco)
 tapa removible
 acero de refuerzo
 junta de dilatacion / tecnopor

PROYECTO: CREACION DEL SERVICIO DE ATENCION INTEGRAL A MUJERES VICTIMAS DE HOGAR EN EL HOGAR TEMPORAL MUJERES VIOLENTAS, DISTRITO DE MORALES, PROVINCIA Y DEPARTAMENTO DE SAN MARTIN - CUI N. 2675514		
ENTIDAD: GERENCIA TERRITORIAL BAJO MAYO - TARAPOTO		
UBICACION: PREDIO RURAL LOS MANGOS - MORALES - SAN MARTIN - SAN MARTIN ESPECIALIDAD: INSTALACIONES SANITARIAS - DRENAJE PLUVIAL		
PLANO: DETALLES DE REGISTRO DE LIMPIEZA, TAPA, MARCO Y CONTRAMARCO REGISTRO CON TAPA REMOVIBLE, ANGULOS METALICOS, EMPALME DE CUNETA Y JUNTA DE DILATACION		
PROYECTISTA: _____ CIP: _____		
ELABORADO: HIDROCONSULT	ESCALA: 1/10	
REVISADO: _____	FECHA: OCT. 2026	LAMINA:
FIRMA Y SELLO:	REVISION: 00	DP-0

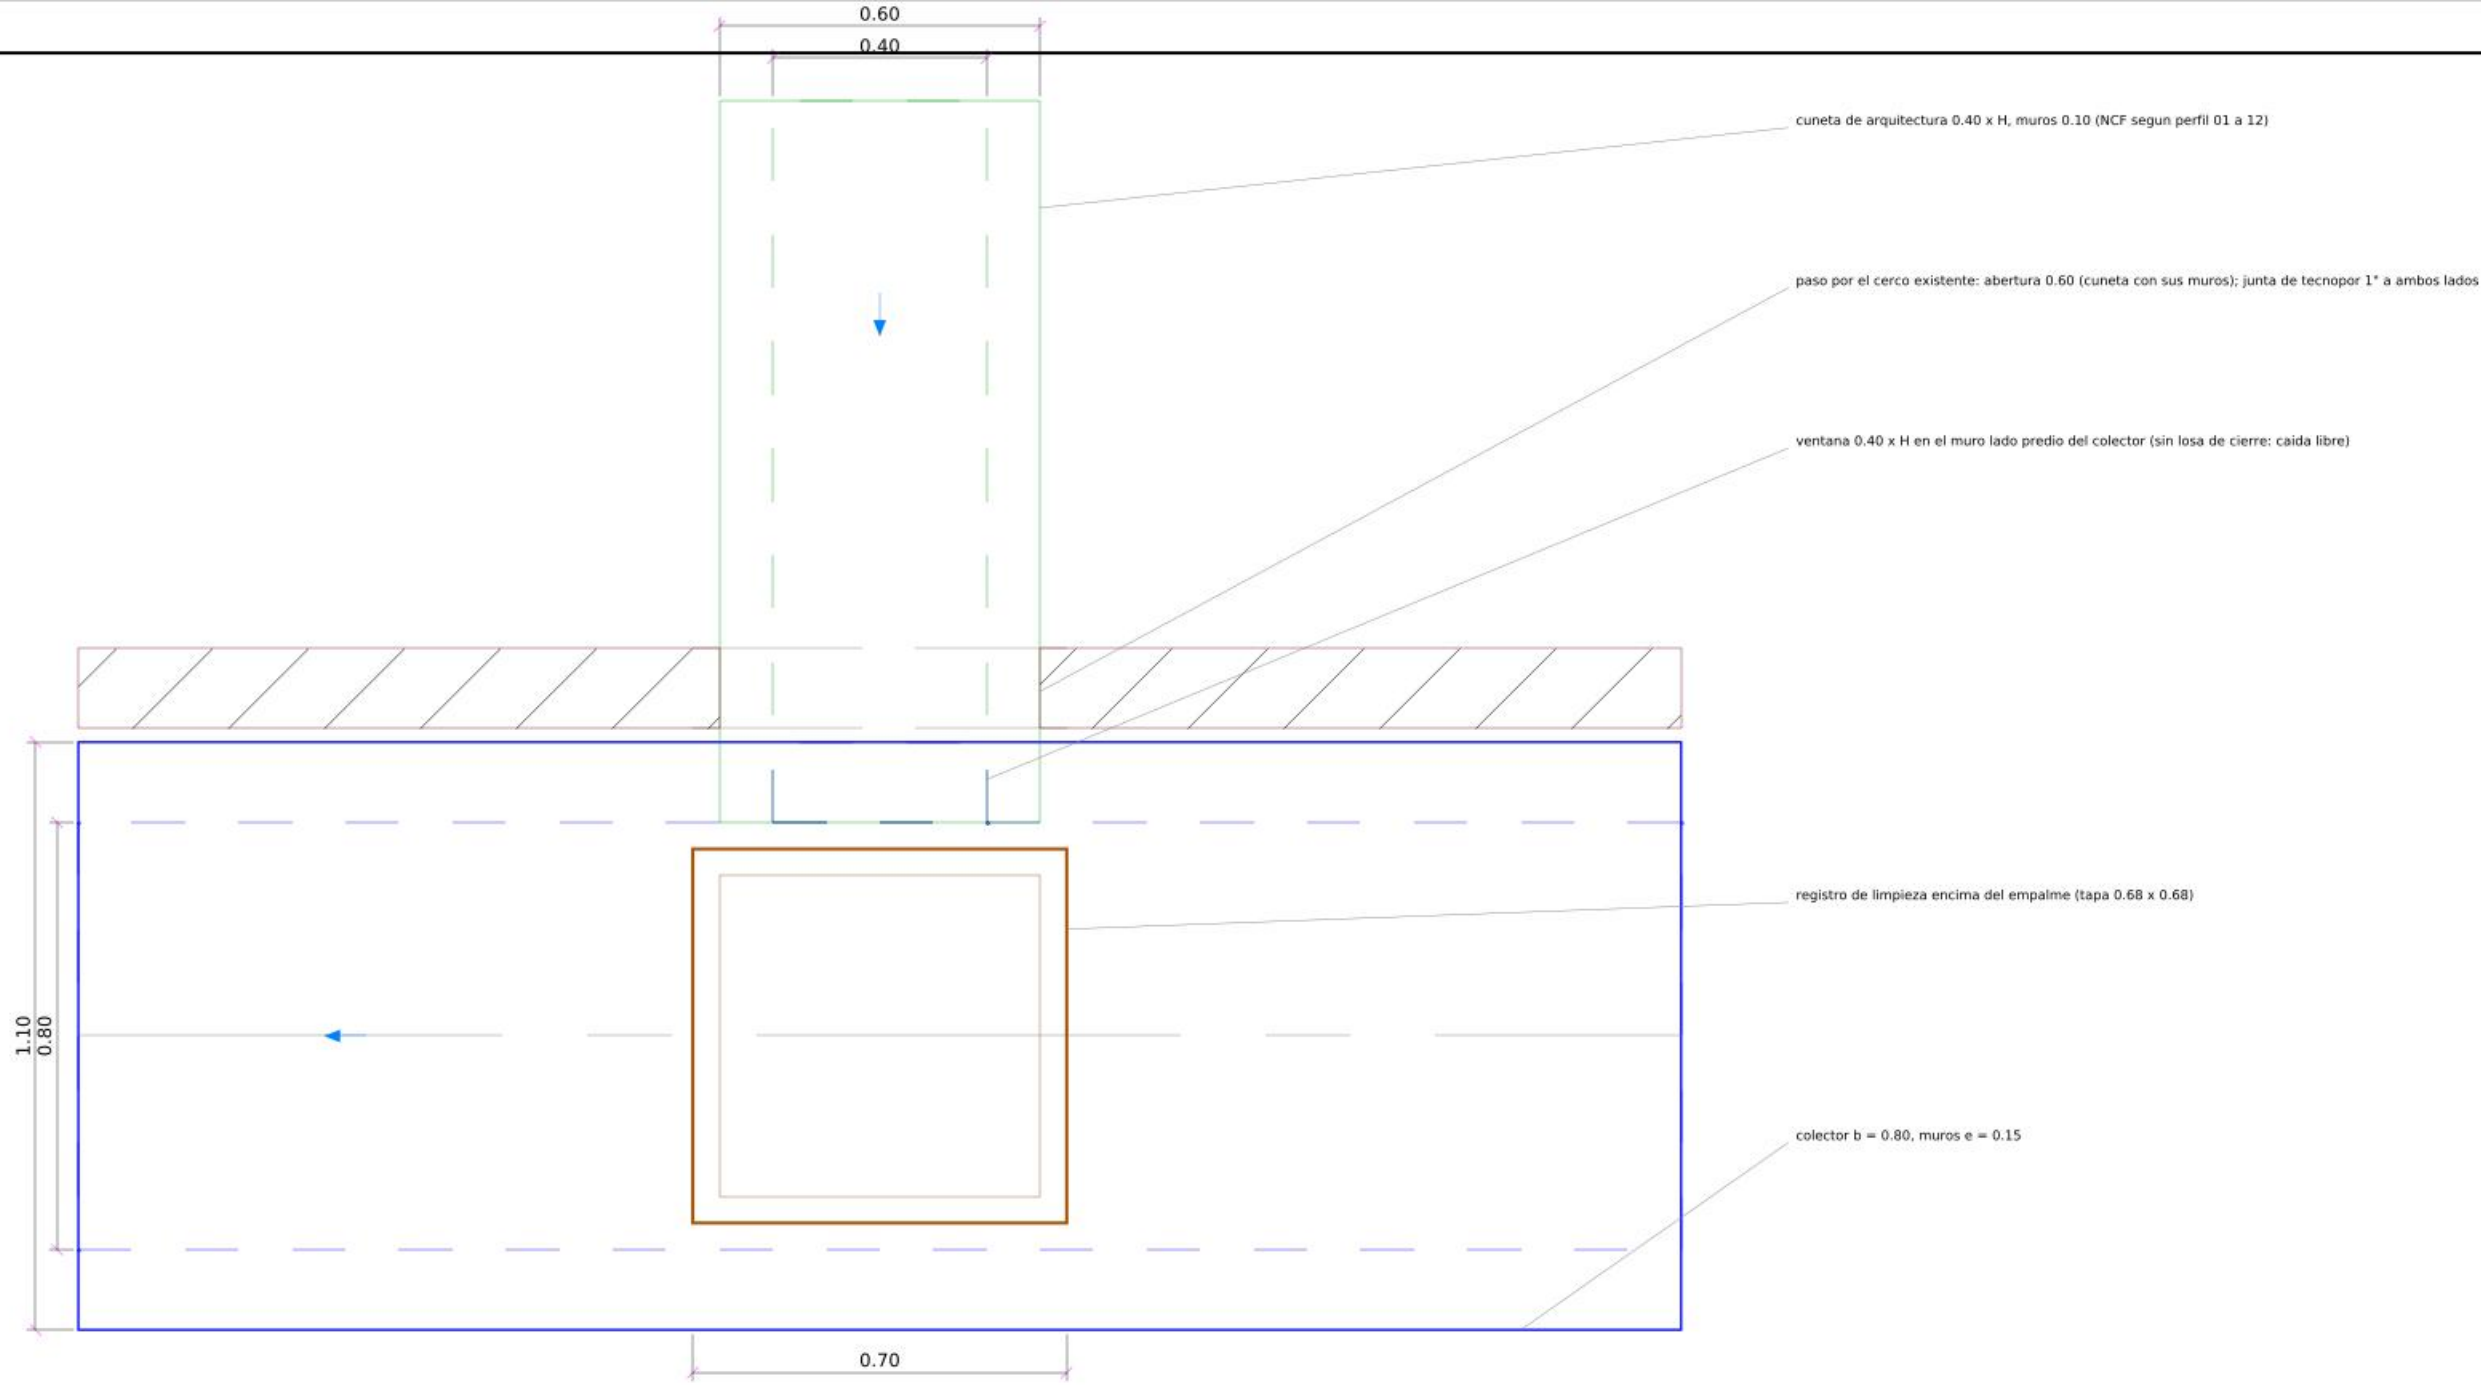


E1. EMPALME DE CUNETA - PLANTA

ESC. 1/10 - losa superior retirada para mostrar la ventana

LEYENDA

- concreto armado del colector $f_c=210$
- cuneta y cerco existentes (arquitectura)
- cuneta de arquitectura
- junta de tecnopor 1"
- nivel de agua
- sentido del flujo

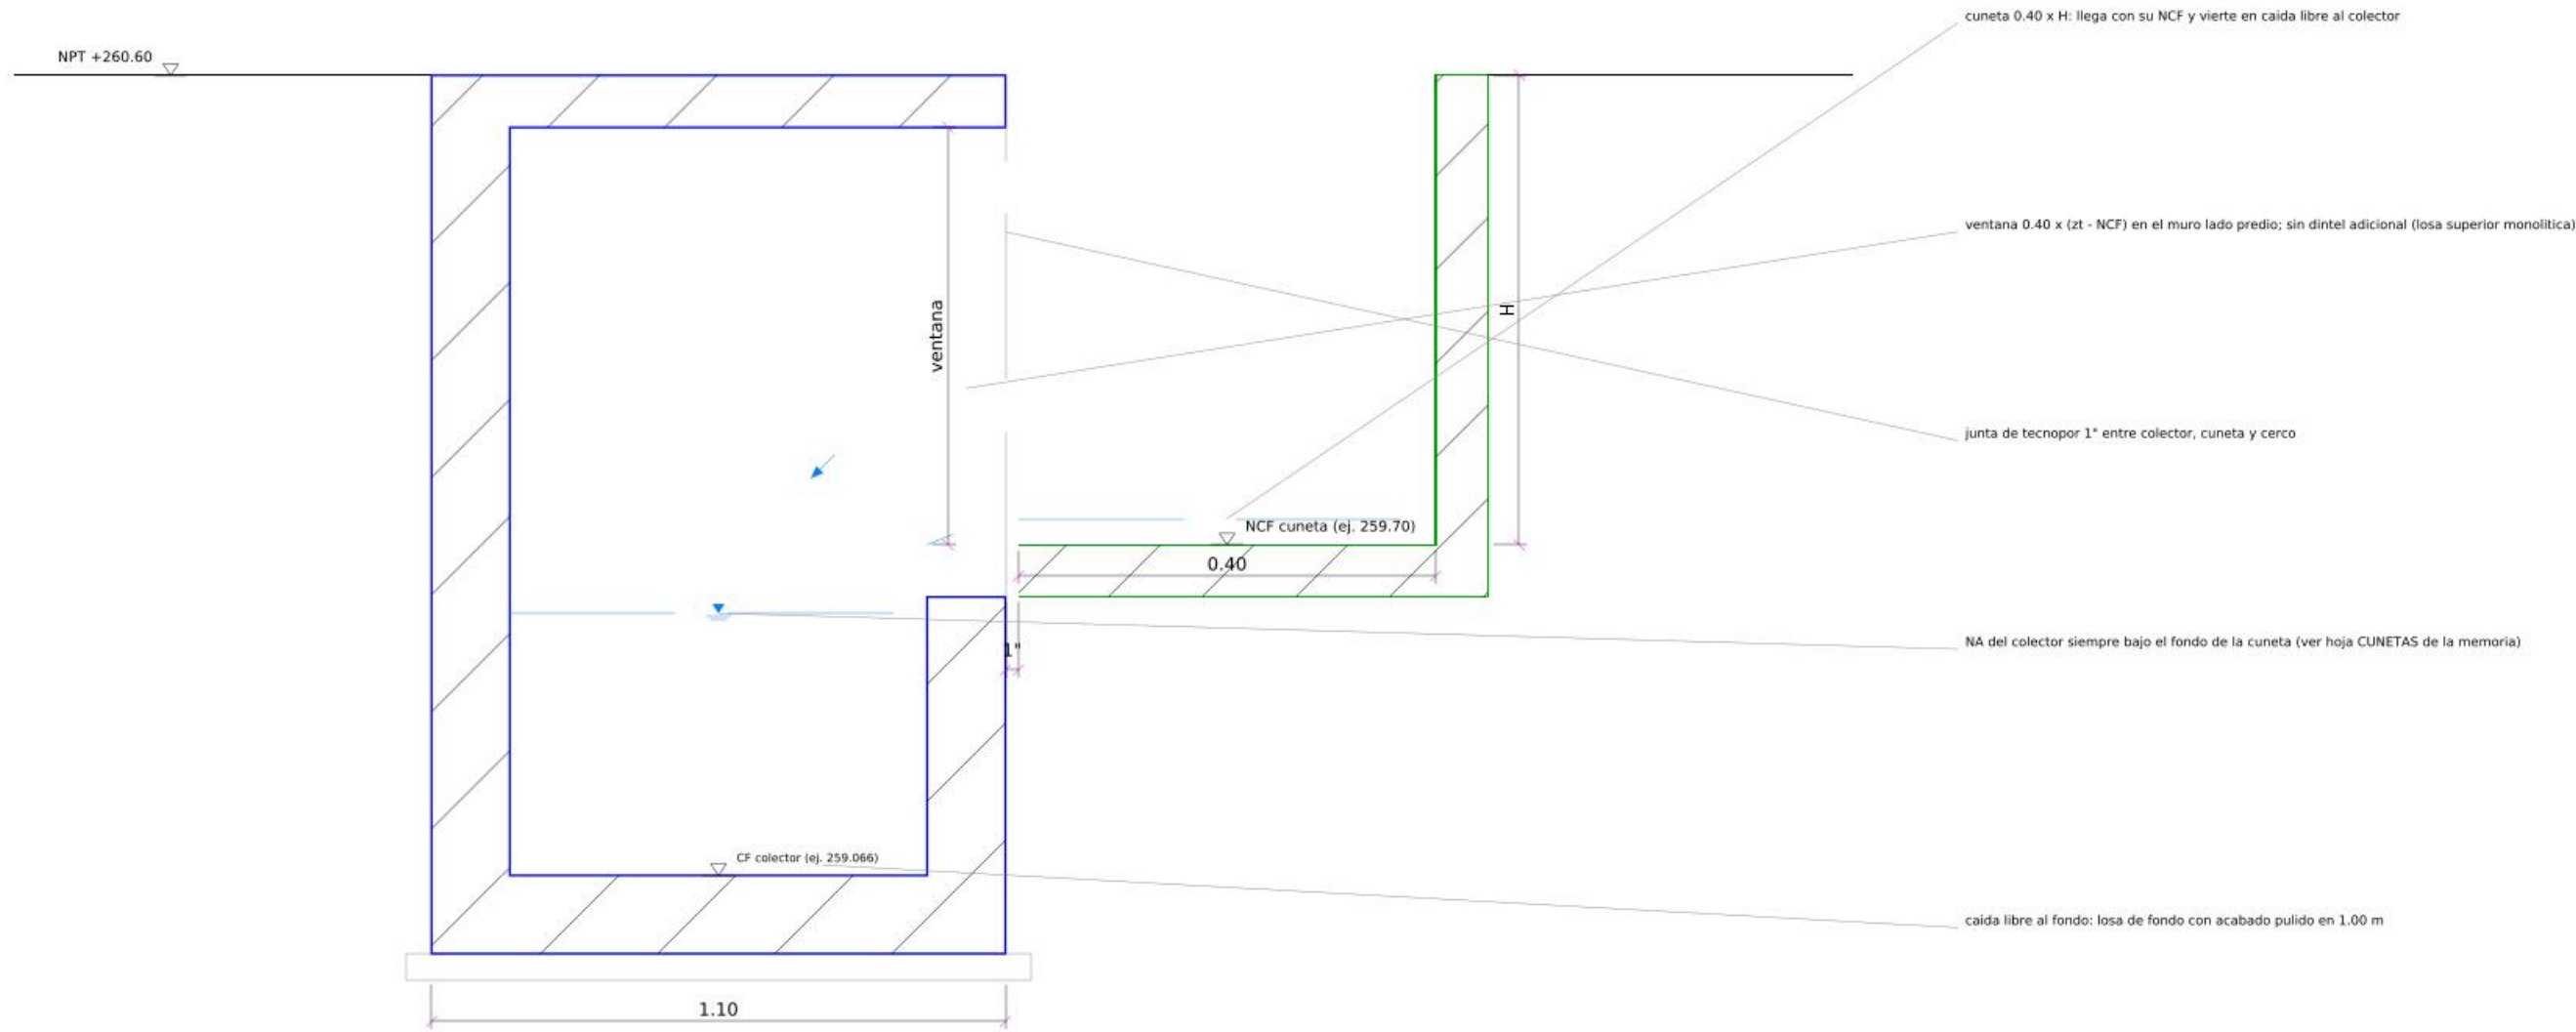

CUADRO DE EMPALMES


CUNETA	PROG.	NCF LLEGA	H VENTANA	REGISTRO
Eje 01	0+001.07	260.12	0.38	CL
Eje 02	0+011.27	259.70	0.80	RS-01
Eje 06	0+032.50	259.75	0.75	RS-03
Eje 07	0+042.68	259.72	0.78	RS-04
Eje 11	0+060.89	259.99	0.51	RS-06*
Eje 12	0+068.56	259.77	0.73	CC

* cuneta Eje 11: entra al tramo diagonal junto al registro RS-06; cuneta Eje 12: entra a la caja de caída CC.

E2. EMPALME DE CUNETA - CORTE TRANSVERSAL (MIRANDO AGUAS ABAJO)

ESC. 1/10 - ejemplo cuneta Eje 02 (0+011.27); en las demas varia H y la cota de fondo

PROYECTO: CREACION DEL SERVICIO DE ATENCION INTEGRAL A MUJERES VICTIMAS DE VIOLENCIA EN EL HOGAR DE REFUGIO TEMPORAL MUJERES VIOLENTADAS, DISTRITO DE MORALES, PROVINCIA Y DEPARTAMENTO DE SAN MARTIN - CUI N. 2675514 ENTIDAD: GERENCIA TERRITORIAL BAJO MAYO - TARAPOTO		
UBICACION: PREDIO RURAL LOS MANGOS - MORALES - SAN MARTIN - SAN MARTIN ESPECIALIDAD: INSTALACIONES SANITARIAS - DRENAJE PLUVIAL		
PLANO: DETALLE DEL EMPALME DE CUNETA AL COLECTOR VENTANA EN EL MURO LADO PREDIO, CAIDA AL FONDO, JUNTAS Y REGISTRO - CUNETAS EJES 01, 02, 06, 07, 11 Y 12 - ESC. 1/10		
PROYECTISTA: _____ CIP: _____		
ELABORADO: HIDROCONSULT	ESCALA: 1/10	
REVISADO: _____	FECHA: OCT. 2026	LAMINA:
FIRMA Y SELLO:	REVISION: 00	

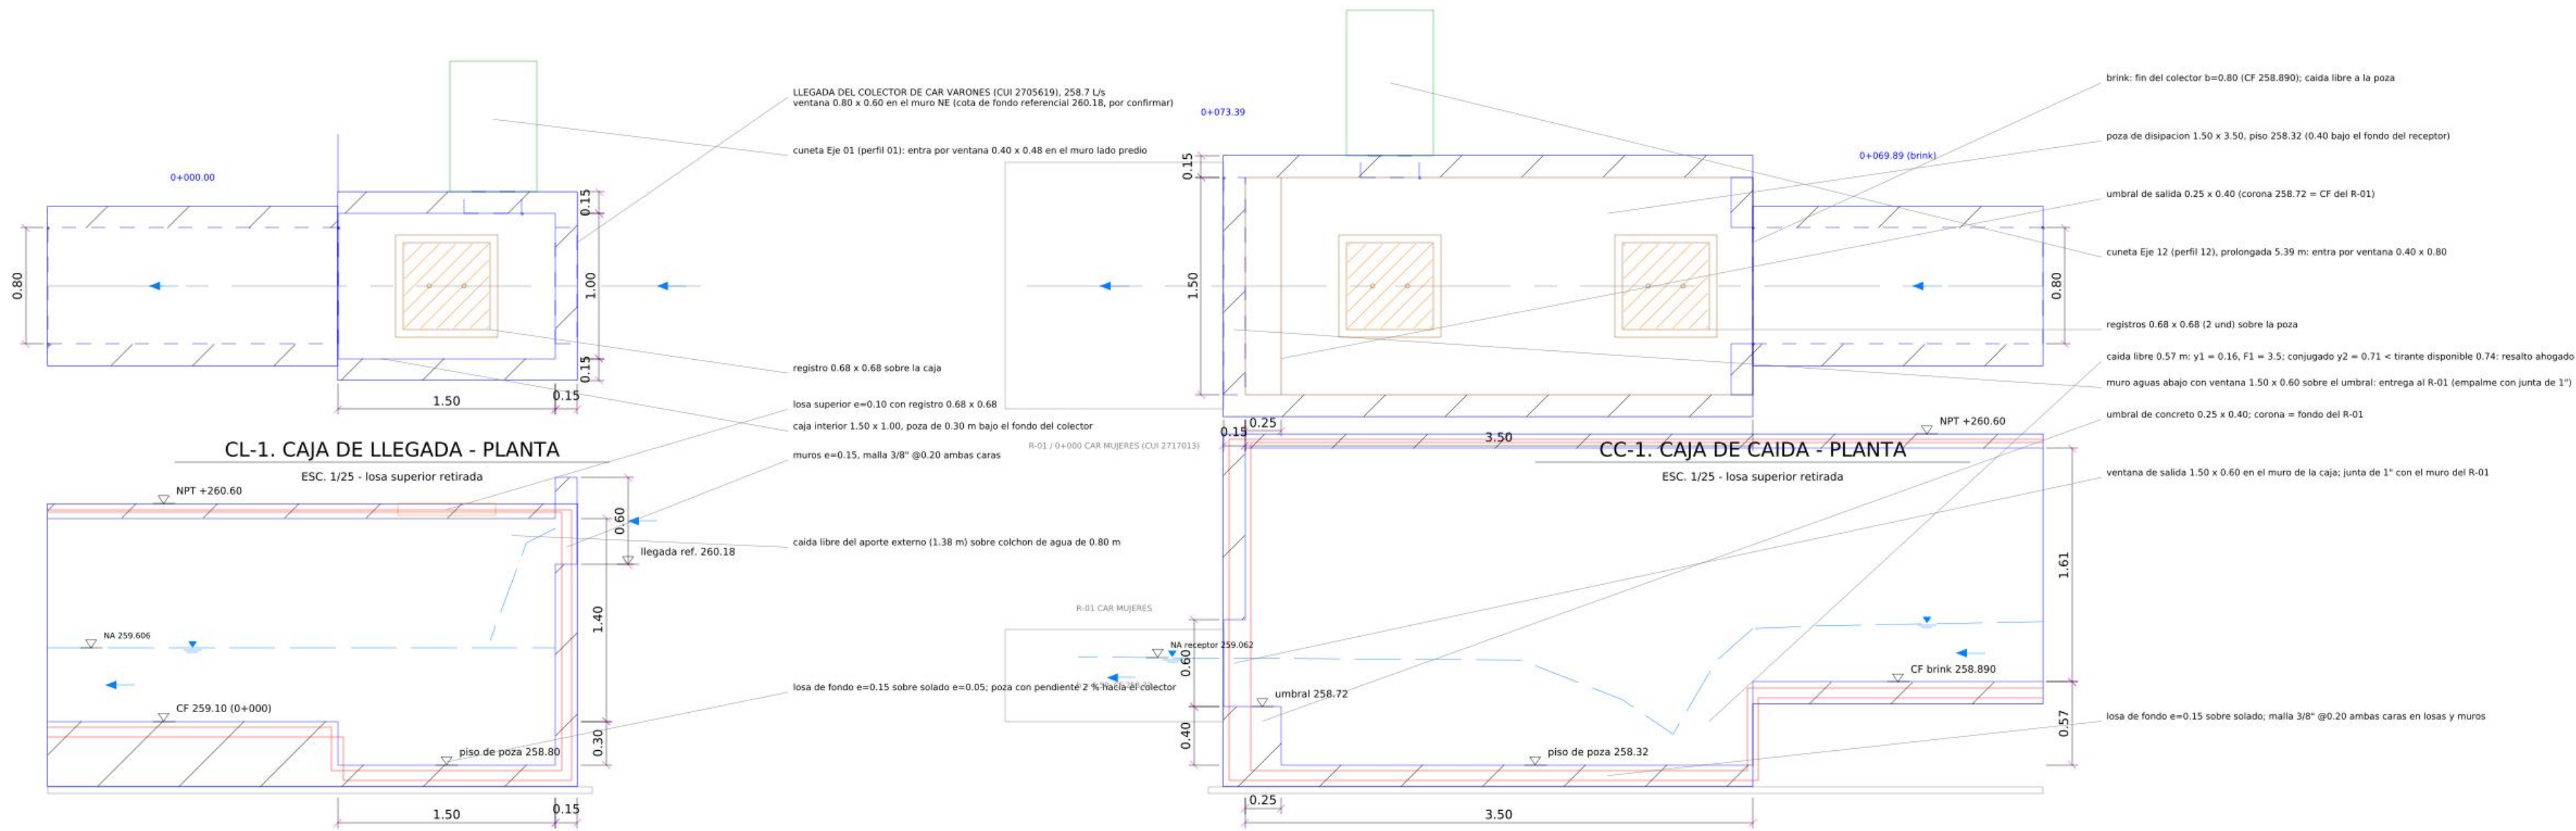

CL-2. CAJA DE LLEGADA - CORTE LONGITUDINAL POR EL EJE
ESC. 1/25

CC-2. CAJA DE CAIDA - CORTE LONGITUDINAL POR EL EJE
ESC. 1/25

CUADRO DE MATERIALES DE LAS CAJAS

CAJA	PARTIDA	CANTIDAD	UND
Caja de llegada CL	concreto f'c=210 (losas + muros)	1.80	m3
	encofrado	18.50	m2
	acero 3/8" @0.20	82.6	kg
Caja de caída CC	excavacion / solado	7.05 / 2.66	m3 / m2
	concreto f'c=210 (losas + muros)	4.38	m3
	encofrado	50.05	m2
	acero 3/8" @0.20	206.8	kg
	excavacion / solado	15.04 / 7.13	m3 / m2

LEYENDA

- concreto armado f'c=210 kg/cm2
- solado f'c=100 e=0.05
- acero transversal (marcos y malla, rojo)
- acero perpendicular al corte (verde)
- nivel de agua / chorro
- poza de disipacion y umbral
- receptor (CAR Mujeres), referencia
- cuneta que llega

NOTAS

- Ambas cajas quedan dentro del predio, cubiertas con losa e=0.10 y registros de 0.68 x 0.68.
- La caja de llegada recibe el colector de CAR Varones (CUI 2705619) como aporte externo; su cota y ancho de llegada (ventana 0.80 x 0.60) son referenciales y se ajustaran a su proyecto.
- La caja de caída entrega al R-01 del colector del CAR Mujeres (CUI 2717013) con fondo del umbral 258.72; el resalto queda ahogado por el tirante del receptor (memoria, hoja EMPALME).
- Secciones transversales de las cajas: muros e=0.15, losa de fondo e=0.15, malla 3/8" @0.20 en ambas caras; esquinas con ganchos de 0.40 m.
- Junta de tecnopor 1" + sello entre la caja CC y el muro del R-01, y entre la caja CL y el colector de llegada.

PROYECTO: CREACION DEL SERVICIO DE ATENCION INTEGRAL A MUJERES VICTIMAS DE VIOLENCIA EN EL HOGAR DE REFUGIO TEMPORAL MUJERES VIOLENTADAS, DISTRITO DE MORALES, PROVINCIA Y DEPARTAMENTO DE SAN MARTIN - CUI N. 2675514 ENTIDAD: GERENCIA TERRITORIAL BAJO MAYO - TARAPOTO		
UBICACION: PREDIO RURAL LOS MANGOS - MORALES - SAN MARTIN - SAN MARTIN ESPECIALIDAD: INSTALACIONES SANITARIAS - DRENAJE PLUVIAL		
PLANO: CAJA DE LLEGADA (0+000) Y CAJA DE CAIDA CON POZA DE DISIPACION (ENTREGA AL CAR MUJERES) PLANTAS, CORTES, ARMADO Y CUADRO DE MATERIALES - ESC. 1/25		
PROYECTISTA: _____ CIP: _____		
ELABORADO: HIDROCONSULT	ESCALA: 1/25	
REVISADO: _____	FECHA: OCT. 2026	LAMINA: _____
FIRMA Y SELLO: _____	REVISION: 00	DP-07

CUADRO DE DOBLADO DE ACERO

ELEMENTO	FORMA	DIAMETRO	ESPACIAM.	LONGITUD (m)	LONG. TOTAL (m)	PESO (kg)
Colector: marcos tramo normal	marco unico cerrado (eje de la seccion)	3/8"	0.20 ver figura: 2 x (0.95 + h + 0.125)	0.30	1725.9	966.5
Colector: marcos cruce de motos	marco unico cerrado (eje de la seccion)	3/8"	0.15	ver figura	76.9	43.0
Colector: marcos cruce de camiones	marco doble (exterior + interior)	1/2"	0.15	ver figura	377.5	375.3
Colector: barras longitudinales	recta con traslape 0.40	3/8"	0.25 / 0.20	continua	1762.7	987.1
Cajas CL y CC: muros y losas	mallá 3/8" @0.20 ambas caras	3/8"	0.20	ver DP-07	516.6	289.3
Registros: refuerzo de borde de abertura	recta	1/2"	2 por lado	1.40	112.0	111.3
Tapas de registro (incluye asas)	recta / U	3/8"	0.10	0.62 / 0.40	94.8	53.1
Anclajes de contramarco		3/8"	8 por registro	0.20	16.0	9.0
Prolongacion de cunetas Ejes 11 y 12	U + rectas	3/8"	0.20	ver DP-06C	175.2	98.1
TOTAL						2932.7


Resumen: acero 3/8" = 2446.1 kg.; acero 1/2" = 486.6 kg.; total = 2932.7 kg (incluye traslapes y ganchos). Angulos metalicos: 151.4 kg.

ESPECIFICACIONES TECNICAS

CONCRETO ARMADO: f'c = 210 kg/cm2 (colector, cajas, tapas, prolongacion de cunetas). Cemento tipo I; agregados limpios; slump 3" a 4".
CONCRETO SIMPLE: solado f'c = 100 kg/cm2, e = 0.05 m; umbral de la poza f'c = 210 kg/cm2 vaciado con la losa de fondo.
ACERO DE REFUERZO: fy = 4200 kg/cm2 (grado 60), corrugado. Ganchos de 0.30 m en marcos y 0.40 m en esquinas de cajas.
RECUBRIMIENTOS: 0.04 m en muros y losa de fondo; 0.025 m en losa superior del tramo normal; 0.04 m en el cruce de camiones; 0.025 m en tapas.
TRASLAPES: 3/8" = 0.40 m ; 1/2" = 0.50 m, alternados. Barras longitudinales de 9.00 m.
LOSA SUPERIOR: vaciada monoliticamente con los muros en todo el colector; acabado frotachado y brunado (a nivel del piso terminado +260.60).
REGISTROS: marco y contramarco de angulo 2"x2"x3/16" y 1 1/2"x1 1/2"x1/8" con anclajes, pintura anticorrosiva y esmalte; tapas de concreto 0.68 x 0.68 x 0.08 con asas.
JUNTAS: cada 4.00 m, e = 1", relleno de poliestireno expandido y sello elastomerico de poliuretano. Tecnopor de 1" entre el colector y el cerco, las cunetas y el piso adyacente.
CAJAS: muros e = 0.15 y losa de fondo e = 0.15 con mallá 3/8" @0.20 en ambas caras; umbral 0.25 x 0.40 en la caja de calda.
CURADO: humedo mínimo 7 dias; no transitar sobre la losa antes de 14 dias; no cargar con camiones antes de 28 dias.
RELLENO: material propio seleccionado, capas de 0.15 m, 95 % del Proctor modificado; incluye la nivelacion del retro hasta la cota de la losa.
EXCAVACION: zanja de 1.60 m de ancho (0.25 m a cada lado del muro); entibar si la profundidad supera 1.50 m o el suelo lo requiere.
VERIFICAR la cota de llegada del colector de CAR Varones (CUI 2705619) antes de vaciar la caja de llegada; verificar en campo la ubicacion del R-01 del CAR Mujeres (CUI 2717013).


GROSOR DE PLUMILLA POR COLOR (CTB)

color 5 concreto (cortes y contornos) 0.40 mm
color 1 acero transversal (marcos) 0.30 mm
color 94 acero longitudinal 0.30 mm
color 32 registros y marcos metalicos 0.30 mm
color 6 cotas, cortes y linderos 0.18 mm
color 14 cerco perimetrico 0.30 mm
color 7 textos, titulos, piso terminado 0.25 mm
color 92 cunetas 0.25 mm
color 30 tapas y cruces vehiculares 0.18 mm
color 34 poza y umbral 0.18 mm
color 150 agua y flujo 0.13 mm
color 8 achurados, auxiliares y arq. base 0.09 mm
color 9 grillas 0.05 mm
caras de isometricos y agua: color verdadero (RGB), plumilla 0.05 mm

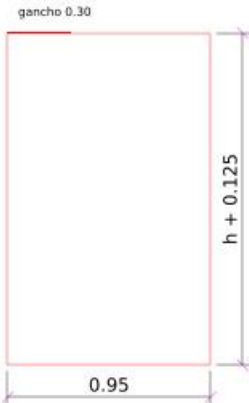

MARCO UNICO 3/8" (tramo normal @0.20, motos @0.15)

un marco cerrado en el eje de muros y losas: 0.95 x (h + 0.125); gancho de 0.30 m; una capa (E.060 14.3.4)

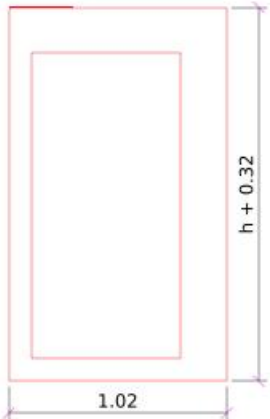


MARCO DOBLE 1/2" @0.15 (cruce de camiones)

marco exterior 1.02 x (h + 0.32) y marco interior 0.80 + 0.22 x (h + 0.08); una capa en cada cara; losa superior e=0.25

NOTAS GENERALES


- Dimensiones en metros y cotas en m.s.n.m., salvo indicacion.
- El colector esta dimensionado para 560.6 L/s (CAR Varones 258.7 + Hogar de Refugio 301.9; TR 25 años).
- Verificaciones hidraulica y estructural segun memoria de calculo del proyecto (RNE CE.040, E.020, E.060; AASHTO LRFD HL-93).
- Las cunetas de arquitectura (perfiles 01 a 12) y sus cotas de fondo son datos del plano PLANTA GENERAL REFUGIO (03-10-2026).
- Confirmar la capacidad portante con el estudio de mecanica de suelos antes del vaciado (presion de contacto 0.33 kg/cm2).

PROYECTO: CREACION DEL SERVICIO DE ATENCION INTEGRAL A MUJERES VICTIMAS DE VIOLENCIA EN EL HOGAR DE REFUGIO TEMPORAL MUJERES VIOLENTADAS, DISTRITO DE MORALES, PROVINCIA Y DEPARTAMENTO DE SAN MARTIN - CUI N. 2675514 ENTIDAD: GERENCIA TERRITORIAL BAJO MAYO - TARAPOTO		
UBICACION: PREDIO RURAL LOS MANGOS - MORALES - SAN MARTIN - SAN MARTIN ESPECIALIDAD: INSTALACIONES SANITARIAS - DRENAJE PLUVIAL		
PLANO: CUADROS DE ACERO, ESPECIFICACIONES TECNICAS Y NOTAS CUADRO DE DOBLADO Y RESUMEN DE ACERO, ESPECIFICACIONES DE MATERIALES Y GROSORES DE IMPRESION		
PROYECTISTA: _____ CIP: _____		
ELABORADO: HIDROCONSULT	ESCALA: 1/25	
REVISADO: _____	FECHA: OCT. 2026	LAMINA:
FIRMA Y SELLO:	REVISION: 00	DP-08

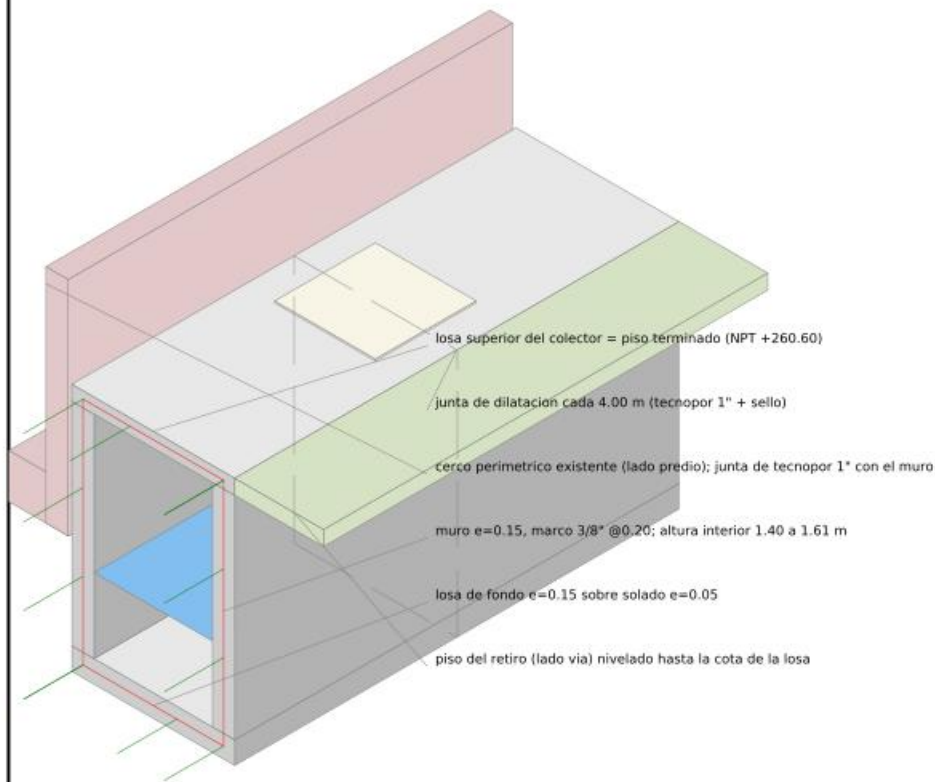

ISOMETRICO 1: COLECTOR JUNTO AL CERCO

tramo tipico de 3.00 m - sin escala

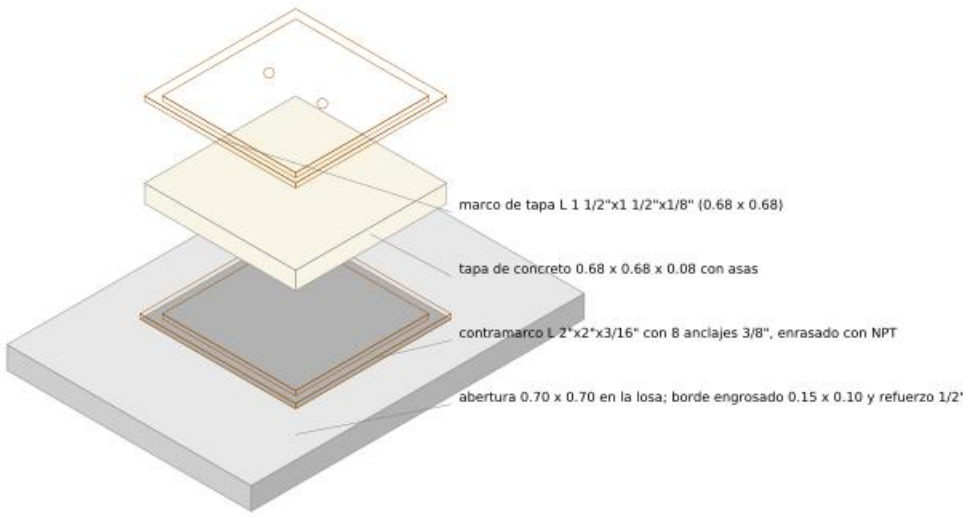


LEYENDA

- concreto armado
- tapa de registro
- agua
- cuneta que llega
- cercos perimetricos existentes
- piso / relleno del retiro
- umbral de la poza
- marco y contramarco metalico


ISOMETRICO 2: REGISTRO DE LIMPIEZA

vista explotada: contramarco, tapa y marco - sin escala

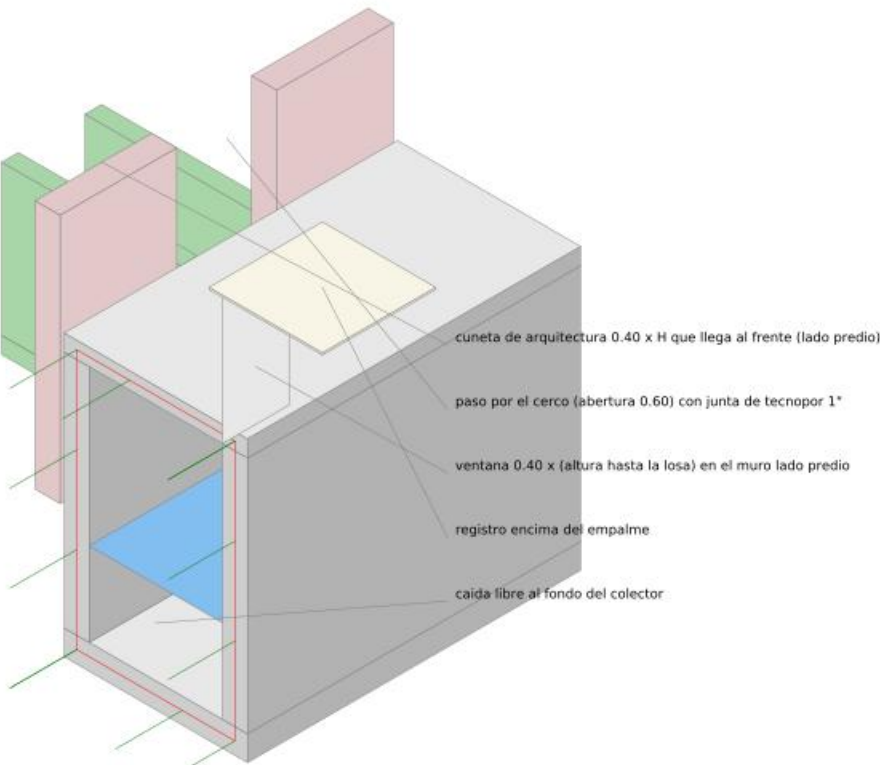

ISOMETRICO 3: EMPALME DE CUNETA

cunetas Ejes 01, 02, 06, 07, 11 y 12 - losa superior cortada - sin escala

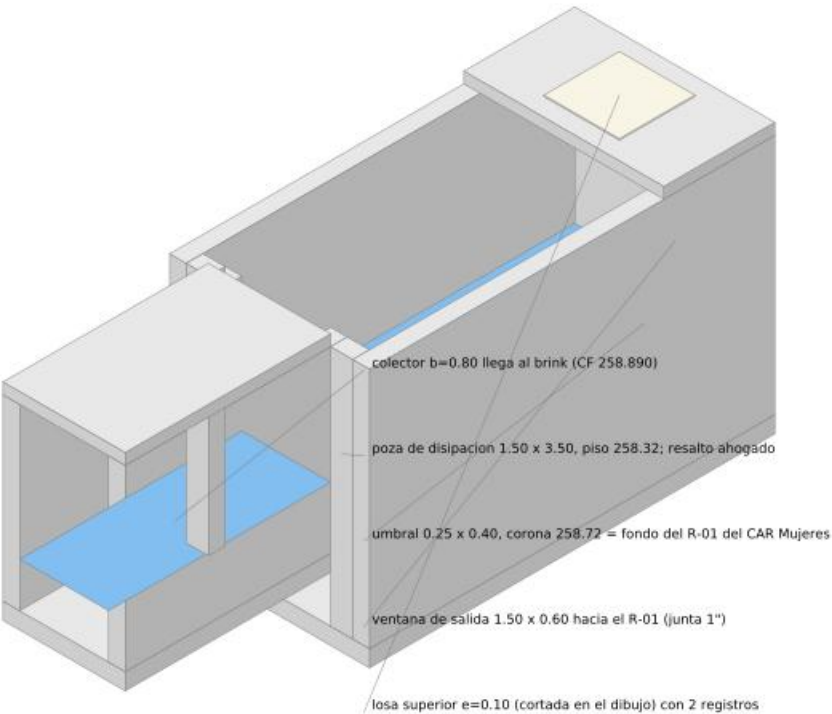

ISOMETRICO 4: CAJA DE CAIDA CON POZA

entrega al R-01 del CAR Mujeres - losa superior cortada - sin escala

PROYECTO:
CREACION DEL SERVICIO DE ATENCION INTEGRAL A MUJERES VICTIMAS DE VIOLENCIA EN EL HOGAR DE REFUGIO TEMPORAL
MUJERES VIOLENTADAS, DISTRITO DE MORALES, PROVINCIA Y DEPARTAMENTO DE SAN MARTIN - CUI N. 2675514
ENTIDAD: GERENCIA TERRITORIAL BAJO MAYO - TARAPOTO

UBICACION: PREDIO RURAL LOS MANGOS - MORALES - SAN MARTIN - SAN MARTIN
ESPECIALIDAD: INSTALACIONES SANITARIAS - DRENAJE PLUVIAL

PLANO: ISOMETRICOS CONSTRUCTIVOS
COLECTOR JUNTO AL CERCO, REGISTRO DE LIMPIEZA, EMPALME DE CUNETA Y CAJA DE CAIDA

PROYECTISTA: _____ CIP: _____

ELABORADO: HIDROCONSULT

ESCALA: 1/25

REVISADO: _____

FECHA: OCT. 2026

LAMINA:


FIRMA Y SELLO:

REVISION: 00

LEYENDA

- colector y cajas de concreto armado (losa superior)
- muro lado predio
- tapa de registro
- cuneta que llega (0.40 x H, muros 0.10)
- colector receptor (CAR Mujeres), referencia

Vista isométrica de conjunto con el trazo real (recta frontal, dos quiebres a 45 grados y recta final hasta la caja de caída); escala vertical ampliada x2 para leer el relieve. Medidas reales en las laminas DP-01 a DP-09.

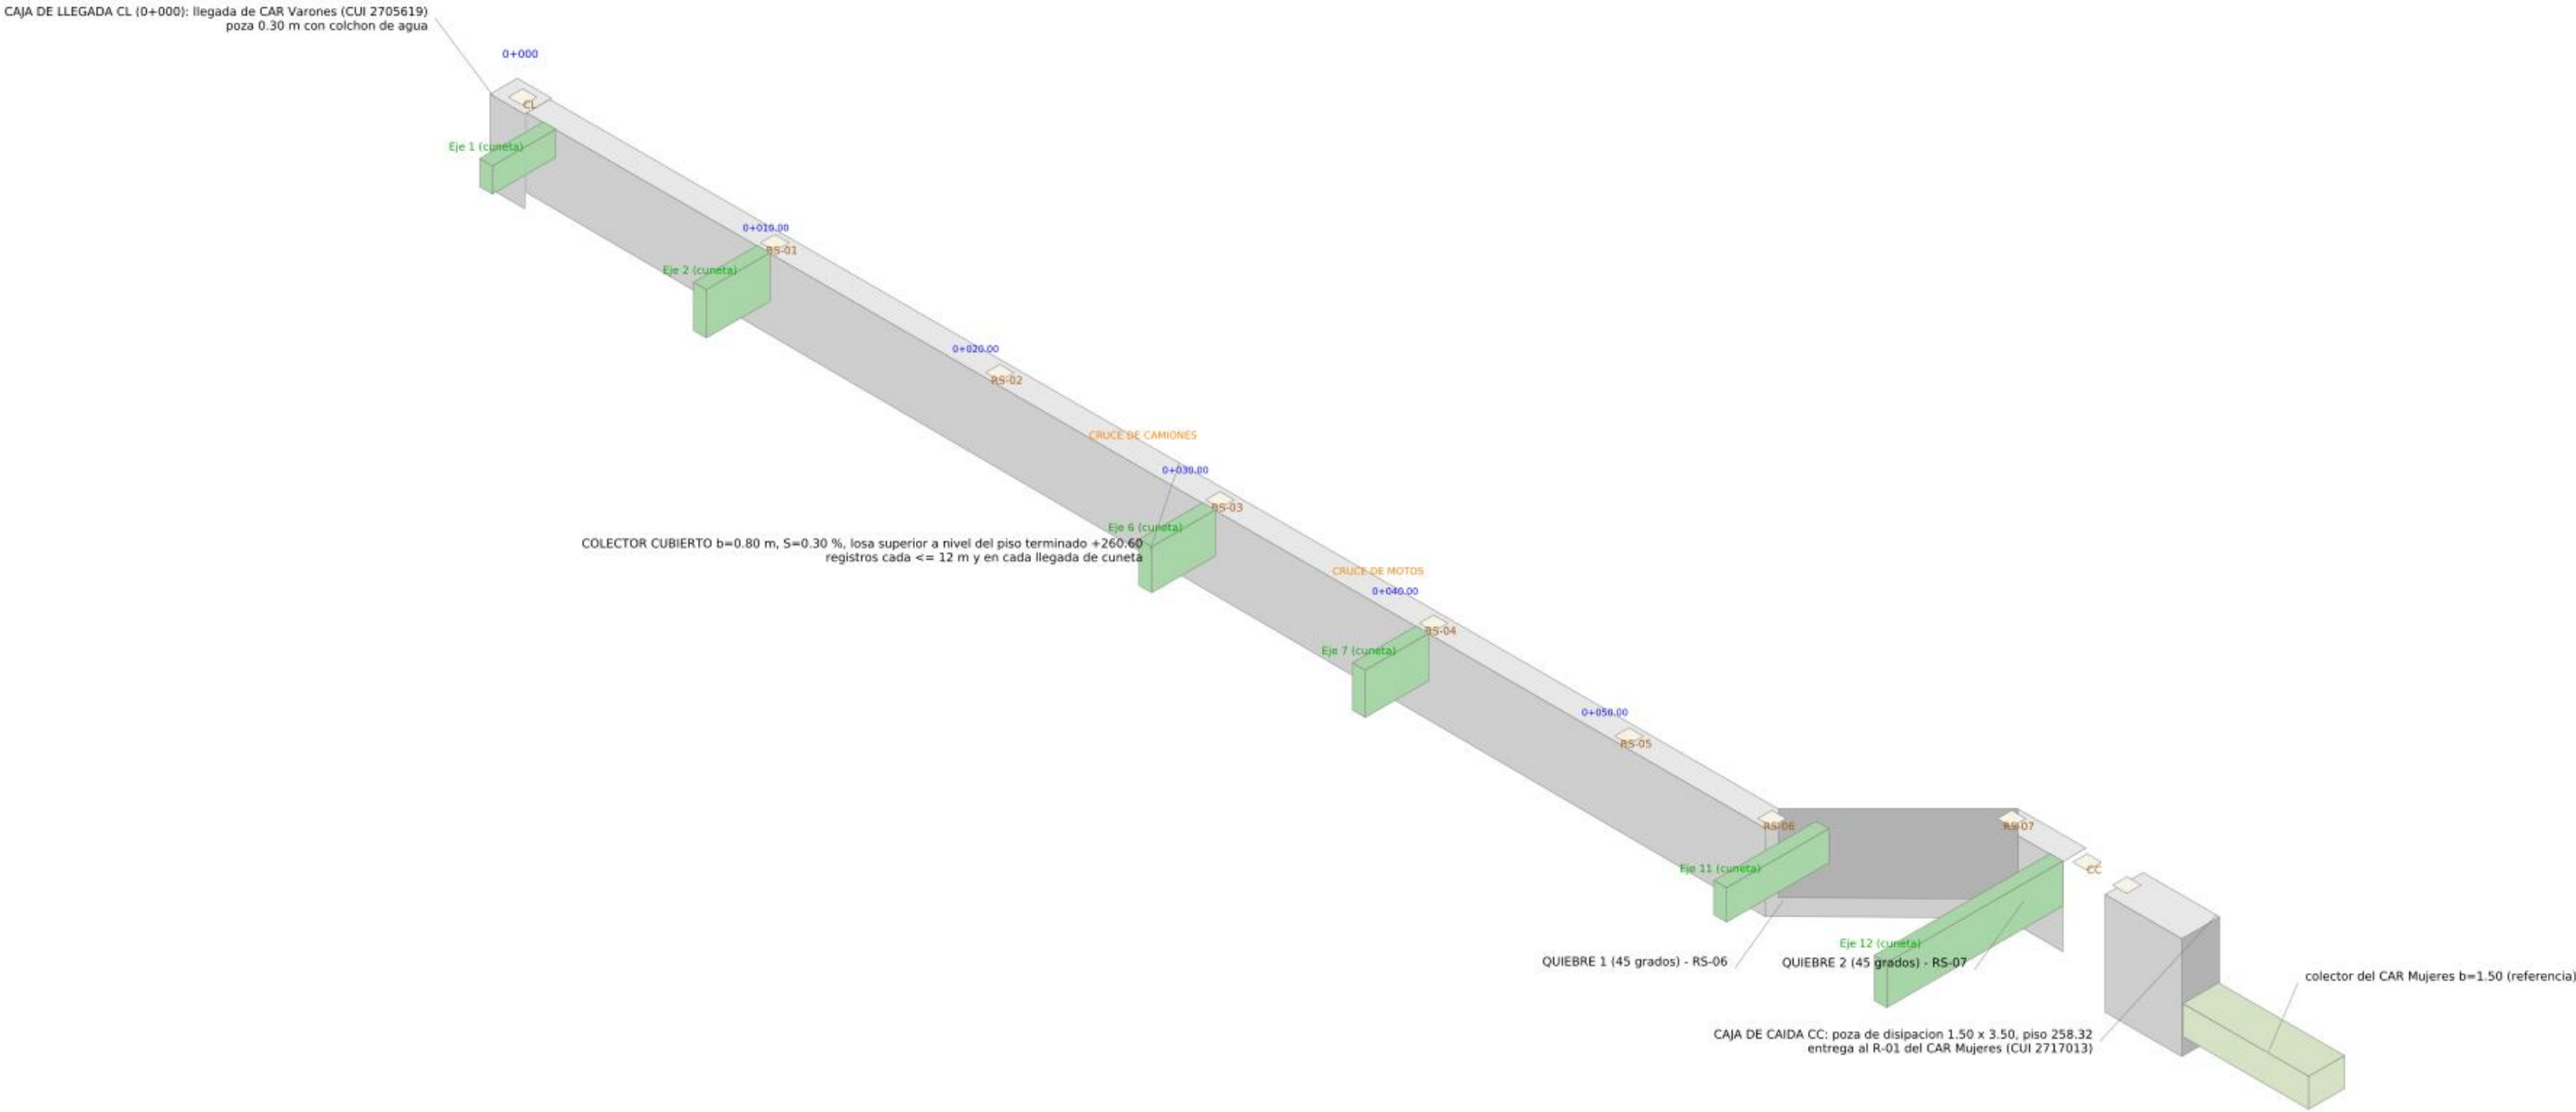

PROYECTO: CREACION DEL SERVICIO DE ATENCION INTEGRAL A MUJERES VICTIMAS DE VIOLENCIA EN EL HOGAR DE REFUGIO TEMPORAL MUJERES VIOLENTADAS, DISTRITO DE MORALES, PROVINCIA Y DEPARTAMENTO DE SAN MARTIN - CUI N. 2675514 ENTIDAD: GERENCIA TERRITORIAL BAJO MAYO - TARAPOTO		
UBICACION: PREDIO RURAL LOS MANGOS - MORALES - SAN MARTIN - SAN MARTIN ESPECIALIDAD: INSTALACIONES SANITARIAS - DRENAJE PLUVIAL		
PLANO: ISOMETRICO GENERAL DEL COLECTOR PLUVIAL VISTA DE CONJUNTO CON EL TRAZO REAL: CAJA DE LLEGADA, COLECTOR CUBIERTO, REGISTROS, EMPALMES DE CUNETAS, QUIEBRES A 45 GRADOS		
PROYECTISTA: _____ CIP: _____		
ELABORADO: HIDROCONSULT	ESCALA: 1/200	
REVISADO: _____	FECHA: OCT. 2026	LAMINA:
FIRMA Y SELLO:	REVISION: 00	DP-10



PROG. 0+010.00 - ESC. 1/25



PROG. 0+028.80 - ESC. 1/25



PROG. 0+065.00 - ESC. 1/25

PARTIDA	UND	METRADO	CRITERIO
Trazo, niveles y replanteo	m2	126.69	franja de 1.60 m x L + cajas + prolongaciones de cuneta
Excavacion de zanja	m3	170.86	1.60 x Hz x L por tramo (Hz desde el terreno existente), cajas y cunetas
Refine y nivelacion de fondo	m2	93.65	1.20 x L + cajas
Relieno compactado con material propio	m3	84.28	relleno lateral de zanja + franja de nivelacion del retiro (1.00 m) + cajas
Eliminacion de material excedente	m3	103.90	(excavacion - relleno) x 1.25

1. H_z varía con el terreno existente (superficie topográfica) y la cota de fondo del colector; ver tabla de tramos en la planilla de metrados.
2. Criterio: los rellenos menores (nivelación de la franja adyacente, base de las cajas) van dentro de la partida de relleno, no como partida aparte.
3. Donde el terreno existente queda por debajo de la losa, el muro lado vía se vacía con encofrado exterior y luego se rellena.

PROYECTO: CREACION DEL SERVICIO DE ATENCION INTEGRAL A MUJERES VICTIMAS DE VIOLENCIA EN EL HOGAR DE REFUGIO TEMPORAL MUJERES VIOLENTADAS, DISTRITO DE MORALES, PROVINCIA Y DEPARTAMENTO DE SAN MARTIN - CUI N. 2675514		
ENTIDAD: REGION TERRITORIAL BAJO MAYO - TARAPOTO		
UBICACION: PREDIO RURAL LOS MANGOS - MORALES - SAN MARTIN - SAN MARTIN		
ESPECIALIDAD: INSTALACIONES SANITARIAS - DRENAJE PLUVIAL		
PLANO: DETALLE DE PARTIDAS; TRAZO, EXCAVACION, RELLENO Y ELIMINACION SECCION TIPICA DE ZANJA POR ZONA Y RESUMEN DE METRADO - ESC. 1/25		
PROYECTISTA: _____ CIP: _____		
ELABORADO: HIDROCONSULT	ESCALA: 1/25	
REVISADO: _____	FECHA: OCT. 2026	LAMINA:
FIRMA Y SELLO:	REVISION: 00	DA-0



PROG. 0+010.00 - h = 1.43 m - ESC. 1/25



PROG. 0+040.00 - h = 1.52 m - ESC. 1/25




PROG. 0+028.80 - h = 1.34 m - ESC. 1/25

RESUMEN DE CONCRETO Y ENCOFRADO (colector + cajas)


PARTIDA	UNO	METRADO
Solado Fc=100 e=0.05	m2	98.74
Concreto Fc=210 - losa de fondo	m3	13.02
Concreto Fc=210 - muros	m3	35.27
Concreto Fc=210 - losa superior (incluye bordes de registro)	m3	9.22
Encofrado y desencofrado	m2	578.57
Acabado frotochado y brumado de losa superior	m2	85.79
Prolongacion de cunetas: concreto / encofrado	m3 / m2	1.52 / 23.21

PROYECTO: CREACION DEL SERVICIO DE ATENCION INTEGRAL A MUJERES VICTIMAS DE VIOLENCIA EN EL HOGAR DE REFUGIO TEMPORAL MUJERES VIOLENTADAS, DISTRITO DE MORALES, PROVINCIA Y DEPARTAMENTO DE SAN MARTIN - CUI N. 2675514		
ENTIDAD: GERENCIA TERRITORIAL BAJO MAYO - TARAPOTO		
UBICACION: PREDIO RURAL LOS MANGOS - MORALES - SAN MARTIN - SAN MARTIN		
ESPECIALIDAD: INSTALACIONES SANITARIAS - DRENAJE PLUVIAL		
PLANO: DETALLE DE PARTIDAS: SOLADO, CONCRETO ARMADO Y ENCOFRADO AREAS Y VOLUMENES POR METRO LINEAL EN CADA ZONA - ESC. 1/25		
PROYECTISTA: _____ CIP: _____		
ELABORADO: HIDROCONSULT	ESCALA: 1/25	
REVISADO: _____	FECHA: OCT. 2026	LAMINA:
FIRMA Y SELLO:	REVISION: 00	DA-0

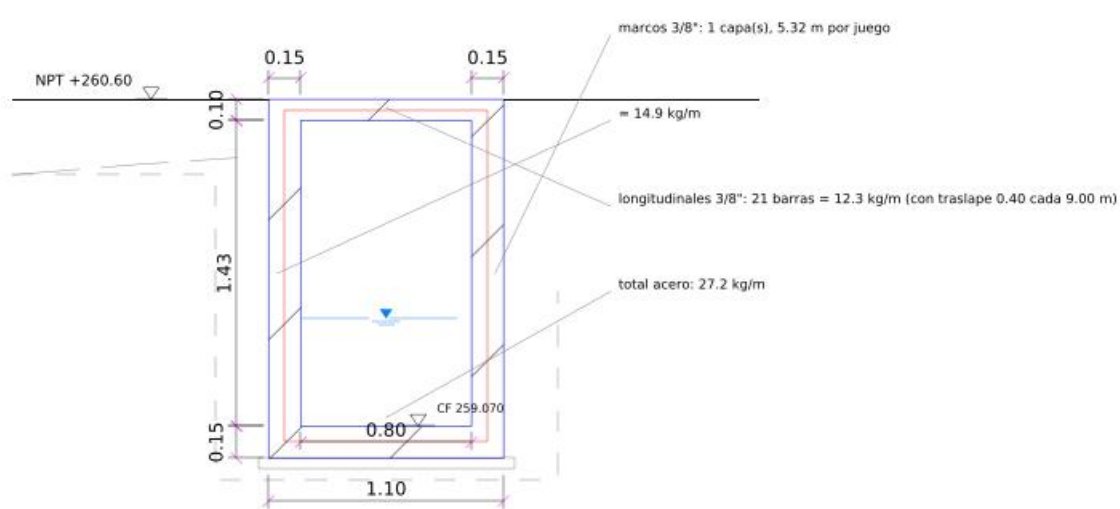


TRAMO NORMAL @0.20

PROG. 0+010.00 - ESC. 1/25

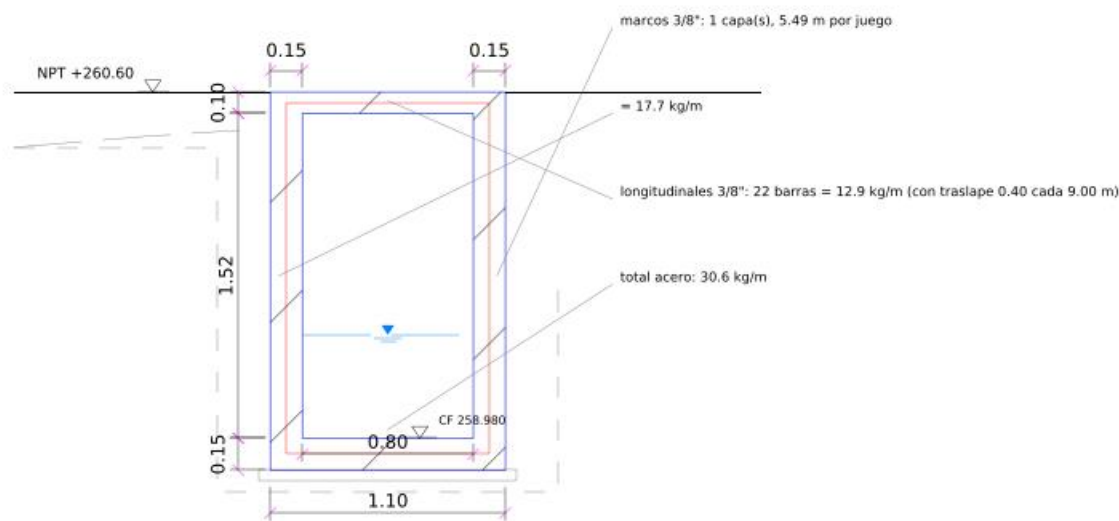

CRUCE DE MOTOS @0.15

PROG. 0+040.00 - ESC. 1/25

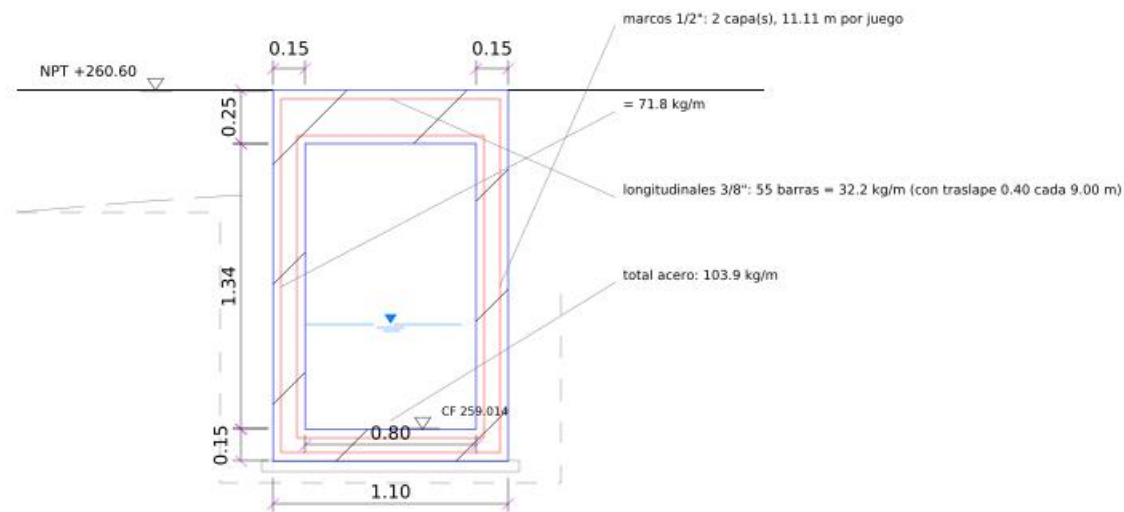

CRUCE DE CAMIONES 1/2" @0.15 DOBLE

PROG. 0+028.80 - ESC. 1/25

RESUMEN DE ACERO, REGISTROS, JUNTAS Y EMPALMES

PARTIDA	UND	METRADO
Acero fy=4200 colector y cajas - 3/8"	kg	2286.0
Acero fy=4200 colector - 1/2" (cruce de camiones)	kg	375.3
Acero en prolongacion de cunetas 3/8"	kg	98.1
Registros: contramarco L 2"x2"x3/16" (10 und)	kg	101.6
Registros: marco de tapa L 1 1/2"x1 1/2"x1/8"	kg	49.8
Tapas de concreto 0.68 x 0.68 x 0.08	und / m3	10 / 0.37
Acero en tapas, bordes, asas y anclajes	kg	173.4
Pintura anticorrosiva y esmalte en angulos	m2	9.82
Junta de dilatacion e=1" con sello (17 und x 5.90 m)	m	100.30
Junta de tecnopor e=1" con el cerco (muro)	m	58.81
Junta de tecnopor e=1" con el piso adyacente	m	150.97
Empalme de cuneta al colector (ventana + calida)	und	6

PROYECTO:
CREACION DEL SERVICIO DE ATENCION INTEGRAL A MUJERES VICTIMAS DE VIOLENCIA EN EL HOGAR DE REFUGIO TEMPORAL
MUJERES VIOLENTADAS, DISTRITO DE MORALES, PROVINCIA Y DEPARTAMENTO DE SAN MARTIN - CUI N. 2675514
ENTIDAD: GERENCIA TERRITORIAL BAJO MAYO - TARAPOTO

UBICACION: PREDIO RURAL LOS MANGOS - MORALES - SAN MARTIN - SAN MARTIN
ESPECIALIDAD: INSTALACIONES SANITARIAS - DRENAJE PLUVIAL

PLANO: DETALLE DE PARTIDAS: ACERO, REGISTROS, JUNTAS Y EMPALMES
DESPIECE POR METRO, INSUMOS POR REGISTRO Y LONGITUDES DE JUNTA - ESC. 1/25

PROYECTISTA: _____ CIP: _____

ELABORADO: HIDROCONSULT

ESCALA: 1/25

REVISADO: _____

FECHA: OCT. 2026

LAMINA:

FIRMA Y SELLO:

REVISION: 00