


CUADRO DE COORDENADAS DE REGISTROS Y CAJAS

PUNTO	PROGRESIVA	ESTE	NORTE	COTA FONDO	COTA TAPA	OBSERVACION
CL	0+000.00	345717.302	9282826.994	259.100	260.600	llegada de CAR Varones y cuneta Eje 01
RS-01	0+011.27	345708.727	9282819.681	259.066	260.600	empalme cuneta Eje 02
RS-02	0+022.00	345700.563	9282812.718	259.034	260.600	limpieza
RS-03	0+032.50	345692.574	9282805.905	259.002	260.600	empalme cuneta Eje 06
RS-04	0+042.68	345684.828	9282799.299	258.972	260.600	empalme cuneta Eje 07
RS-05	0+052.00	345677.737	9282793.251	258.944	260.600	limpieza
RS-06	0+058.81	345672.559	9282788.830	258.924	260.600	quebre 1 (45 grados) y empalme cuneta Eje 11
RS-07	0+066.89	345671.917	9282780.776	258.899	260.600	quebre 2 (45 grados)
CC	0+069.89	345669.635	9282778.829	258.320	260.600	poza de disipacion y empalme cuneta Eje 12: entrega al R-01 de CAR Mujeres
R-01 (receptor)	0+073.39	345666.974	9282776.560	258.720	259.250	0+000 del tramo CAR Mujeres

Coordenadas UTM WGS84 - Zona 18 Sur. Ubicacion referencial: el plano de arquitectura se georeferencio con el R-01 del CAR Mujeres y el rumbo de su lindero (azimut 49.54); verificar en campo.

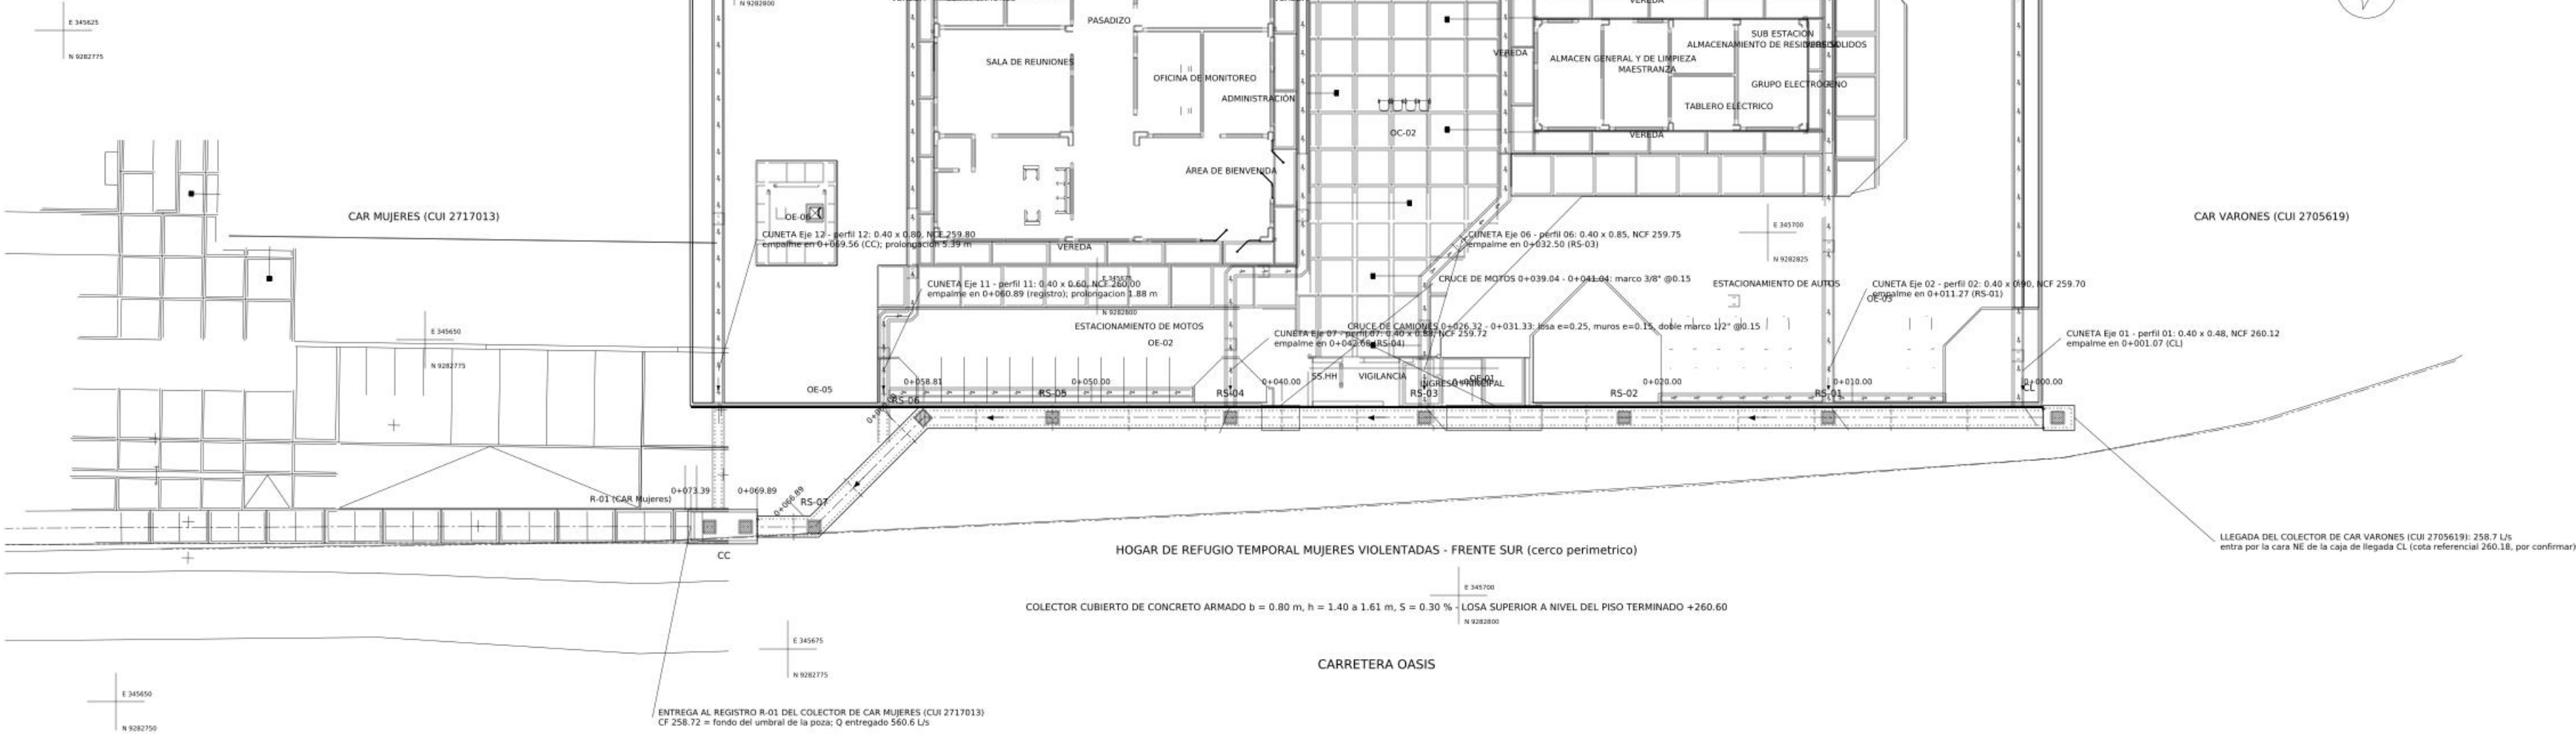


LEYENDA

- muro exterior del colector
- cara interior (bajo losa superior)
- eje del colector
- registro de limpieza con tapa removible
- jointa de dilatacion cada 4.00 m
- cruce vehicular (motos / camiones)
- poza de disipacion (caja de caída)
- cuneta de arquitectura que llega al colector
- cercos perimetricos del predio
- lindero con la Crta. Oasis
- arquitectura (referencia)
- sentido del flujo

NOTAS

- Colector de concreto armado $f_c=210 \text{ kg/cm}^2$, cubierto en todo su recorrido, losa superior vaciada monoliticamente con los muros.
- El colector va por fuera del cerco, dentro del predio: muro lado predio a 0.025 m del cerco (junta de tecnopor de 1"). Eje a 0.575 m del cerco.
- Progresivas a lo largo del eje desde la caja de llegada CL (limite con CAR Varones), crecientes hacia la entrega al CAR Mujeres.
- Registros de limpieza con tapa removible a ras del piso terminado, en cada empalme de cuneta, en los quebres y cada 12.00 m como maximo.
- Cotas en m.s.n.m. Cara superior de la losa = piso terminado del frente +260.60. Fondo 259.10 (0+000) a 258.89 (brink), $S = 0.30 \%$.
- Cajas: CL de llegada (0+000) con poza de 0.30 m; CC de caída con poza de 0.40 m bajo el fondo del receptor y umbral de salida.
- Las cunetas de arquitectura (perfiles 01 a 12) entran por ventana en el muro lado predio; las de los Ejes 11 y 12 se prolongan fuera del cerco.
- Ver perfil en DP-02 y DP-03, secciones en DP-04 a DP-06, cajas en DP-07, acero y especificaciones en DP-08, isometricos en DP-09 y DP-10.

PROYECTO: CREACION DEL SERVICIO DE ATENCION INTEGRAL A MUJERES VICTIMAS DE VIOLENCIA EN EL HOGAR DE REFUGIO TEMPORAL MUJERES VIOLENTADAS, DISTRITO DE MORALES, PROVINCIA Y DEPARTAMENTO DE SAN MARTIN - CUI N. 2675514 ENTIDAD: GERENCIA TERRITORIAL BAJO MAYO - TARAPOTO		
UBICACION: PREDIO RURAL LOS MANGOS - MORALES - SAN MARTIN - SAN MARTIN ESPECIALIDAD: INSTALACIONES SANITARIAS - DRENAJE PLUVIAL		
PLANO: PLANTA DEL COLECTOR PLUVIAL TRAMO HOGAR DE REFUGIO (0+000.00 - 0+073.39) - TRAZO, REGISTROS, CAJAS Y EMPALME CON CAR MUJERES		
PROYECTISTA: _____ CIP: _____		
ELABORADO: HIDROCONSULT	ESCALA: 1/200	
REVISADO: _____	FECHA: OCT. 2026	LAMINA: _____
FIRMA Y SELLO: _____	REVISION: 00	DP-01

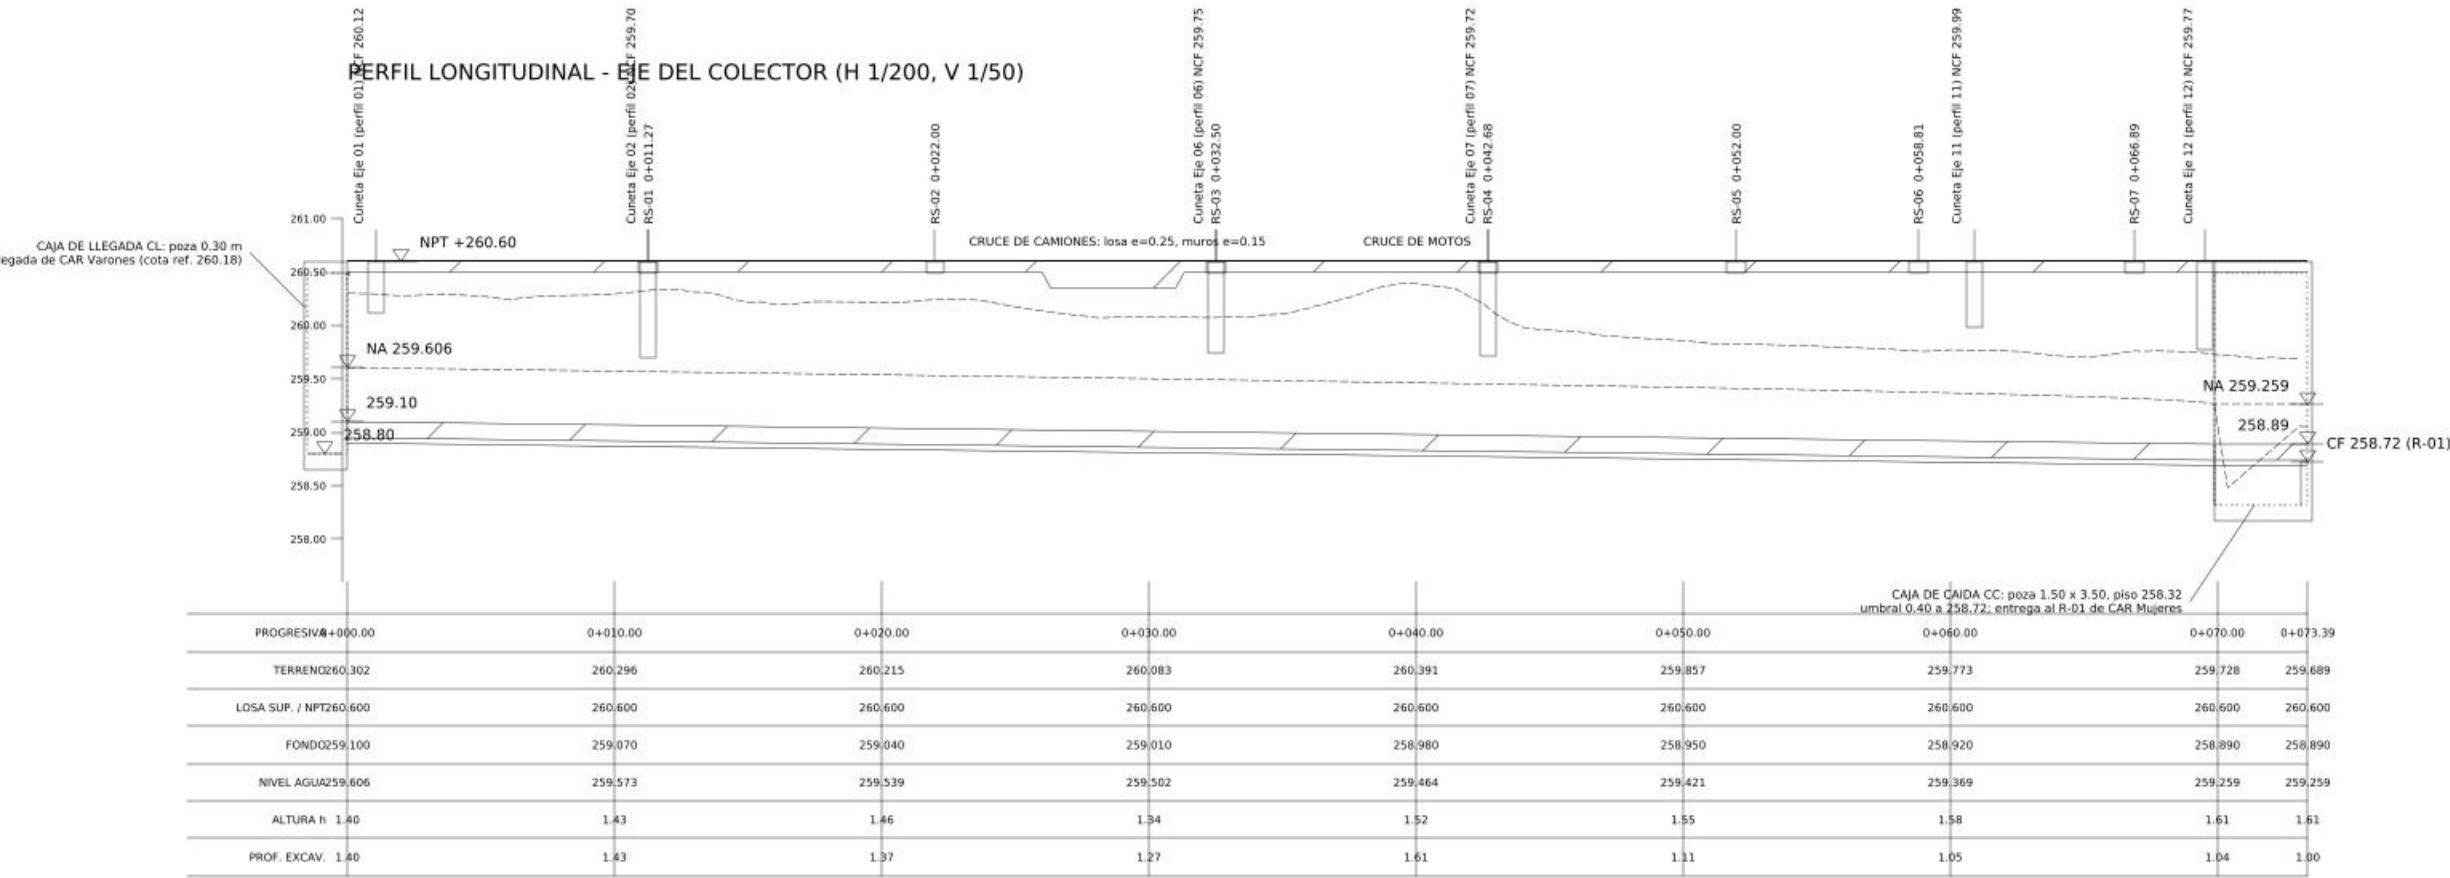


LEYENDA

- piso terminado / losa superior (NPT +260.60)
- - - - - terreno existente (superficie topografica)
- colector de concreto armado
- solado e=0.05
- - - - - nivel de agua de diseno (Q = 560.6 L/s)
- registro de limpieza
- llegada de cuneta
- poza de disipacion y umbral

NOTAS

- Perfil con exageracion vertical x4 (H 1/200, V 1/50). Cotas en m.s.n.m.
- El nivel de agua de diseno resulta del calculo de flujo gradualmente variado (memoria de calculo, hoja PERFIL_FLUJO); control: tirante critico en el brink de la caída.
- Caudal de diseno 560.6 L/s: CAR Varones (258.7 L/s, dato de su memoria) + Hogar de Refugio (301.9 L/s), TR 25 años.
- Relleno nivelado del retro hasta la cota de la losa (+260.60) donde el terreno existente queda por debajo.
- Ver perfil detallado por tramos en las laminas DP-03A y DP-03B.

PROYECTO: CREACION DEL SERVICIO DE ATENCION INTEGRAL A MUJERES VICTIMAS DE VIOLENCIA EN EL HOGAR DE REFUGIO TEMPORAL MUJERES VIOLENTADAS, DISTRITO DE MORALES, PROVINCIA Y DEPARTAMENTO DE SAN MARTIN - CUI N. 2675514 ENTIDAD: GERENCIA TERRITORIAL BAJO MAYO - TARAPOTO		
UBICACION: PREDIO RURAL LOS MANGOS - MORALES - SAN MARTIN - SAN MARTIN ESPECIALIDAD: INSTALACIONES SANITARIAS - DRENAJE PLUVIAL		
PLANO: PERFIL LONGITUDINAL GENERAL DEL COLECTOR ESCALA H 1/200 - V 1/50 - NIVELES DE DISEÑO Y PERFIL HIDRAULICO (0+000.00 - 0+073.39)		
PROYECTISTA: _____ CIP: _____		
ELABORADO: HIDROCONSULT	ESCALA: 1/200	
REVISADO: _____	FECHA: OCT. 2026	LAMINA:
FIRMA Y SELLO:	REVISION: 00	DP-02

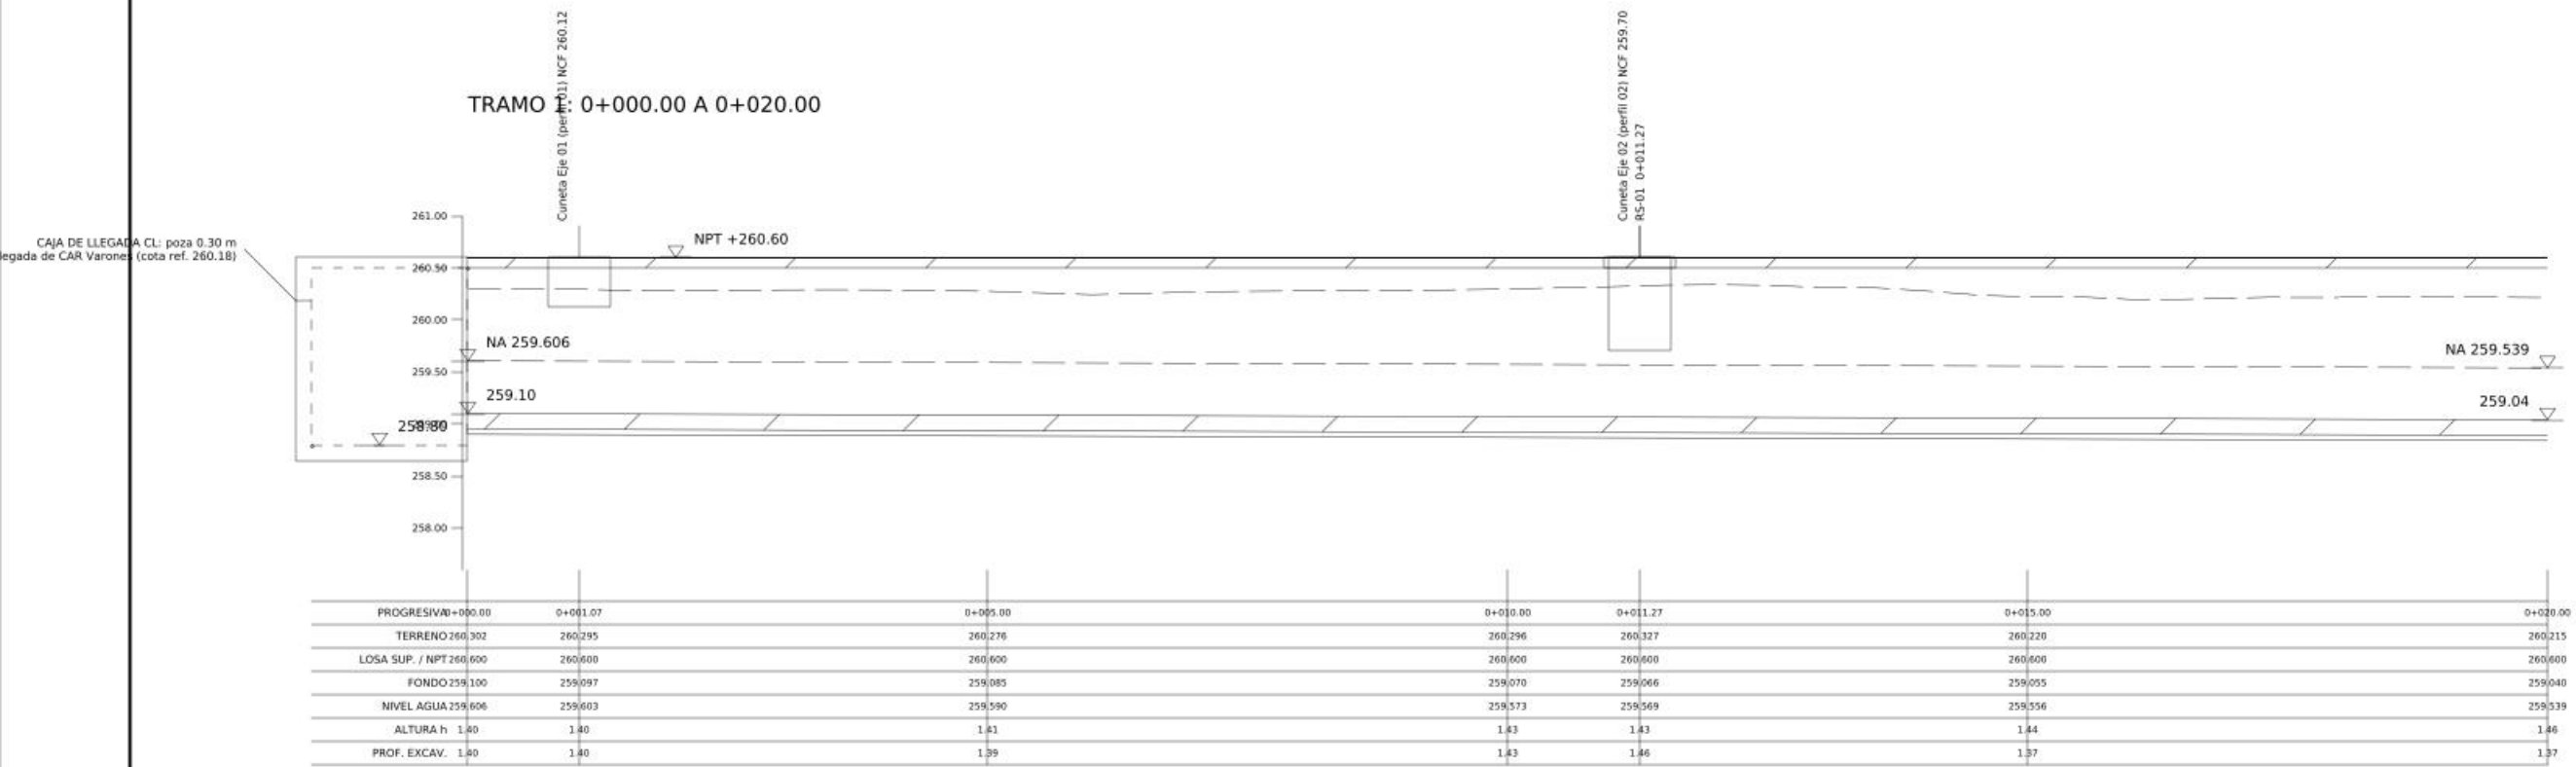


LEYENDA

- concreto armado del colector
- solado e=0.05
- tapa de registro
- nivel de agua de diseno
- piso terminado +260.60
- terreno existente
- llegada de cuneta

NOTAS

- Escala real: horizontal = vertical.
- Cotas en m.s.n.m.; progresivas desde la caja CL.
- Prof. excav. medida desde el terreno existente al fondo del solado.

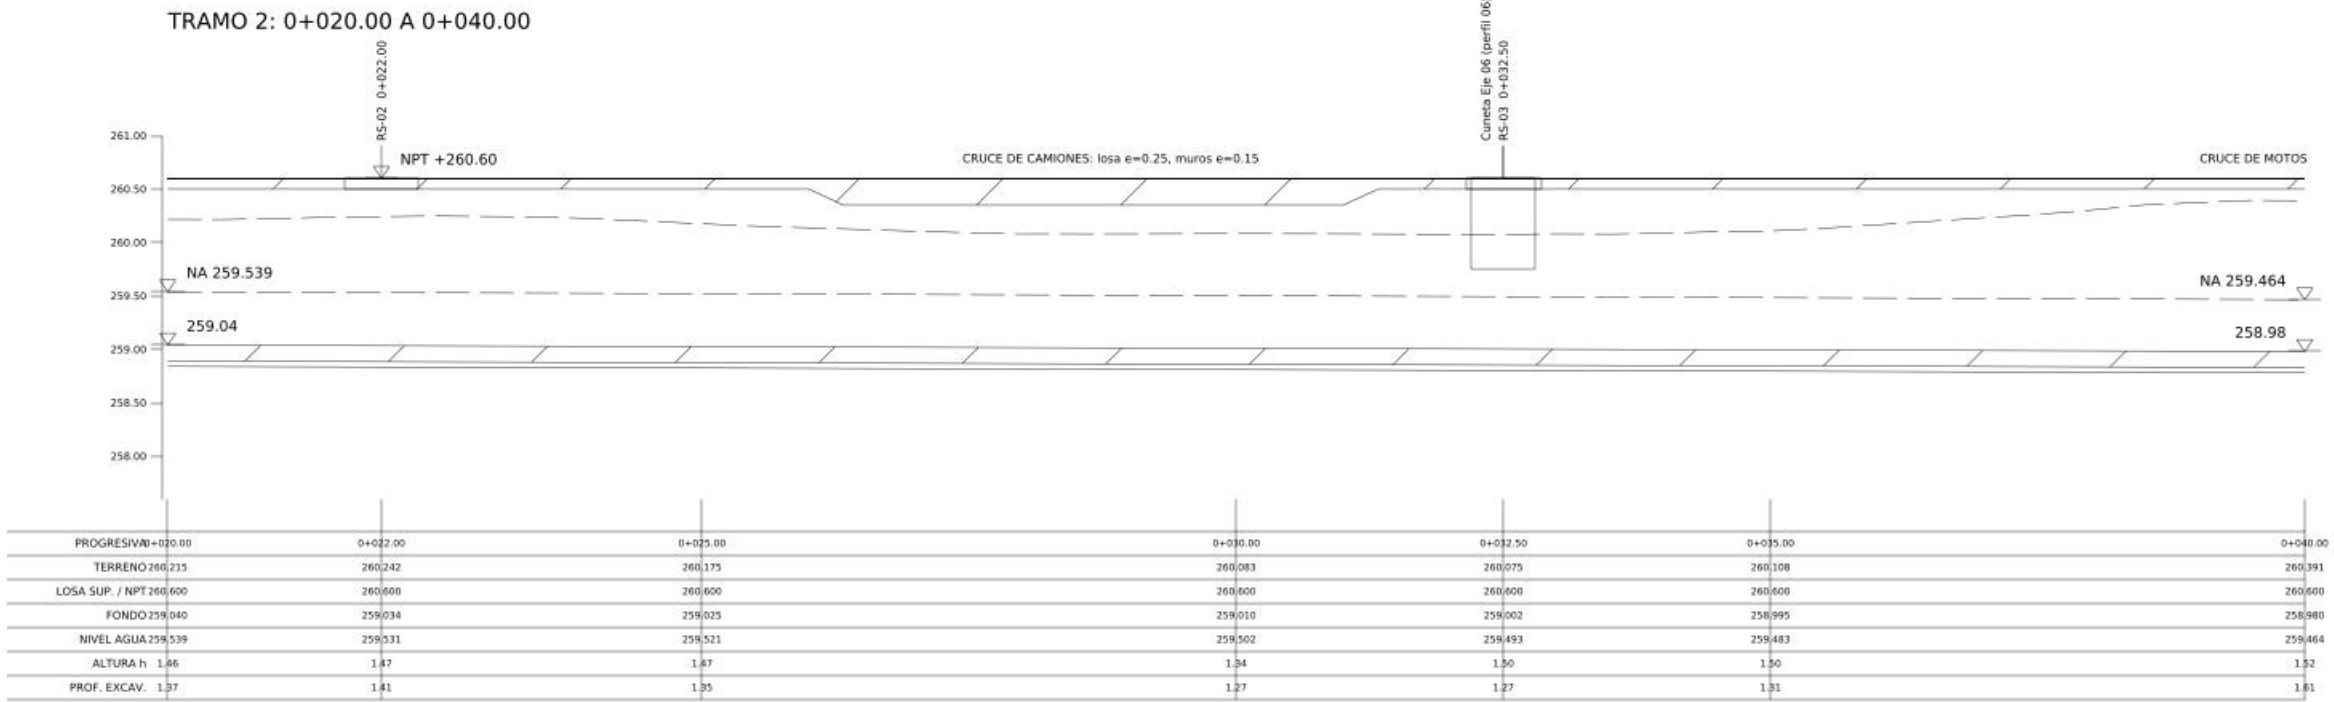

PROYECTO:
CREACION DEL SERVICIO DE ATENCION INTEGRAL A MUJERES VICTIMAS DE VIOLENCIA EN EL HOGAR DE REFUGIO TEMPORAL
MUJERES VIOLENTADAS, DISTRITO DE MORALES, PROVINCIA Y DEPARTAMENTO DE SAN MARTIN - CUI N. 2675514
ENTIDAD: GERENCIA TERRITORIAL BAJO MAYO - TARAPOTO

UBICACION: PREDIO RURAL LOS MANGOS - MORALES - SAN MARTIN - SAN MARTIN
ESPECIALIDAD: INSTALACIONES SANITARIAS - DRENAJE PLUVIAL

PLANO: PERFIL LONGITUDINAL DETALLADO DEL COLECTOR
TRAMOS 1 Y 2 (0+000.00 - 0+040.00) - ESCALA REAL 1/50 (H = V)

PROYECTISTA: _____ CIP: _____

ELABORADO: HIDROCONSULT


ESCALA: 1/50

REVISADO: _____

FECHA: OCT. 2026 LAMINA:


FIRMA Y SELLO:

REVISION: 00

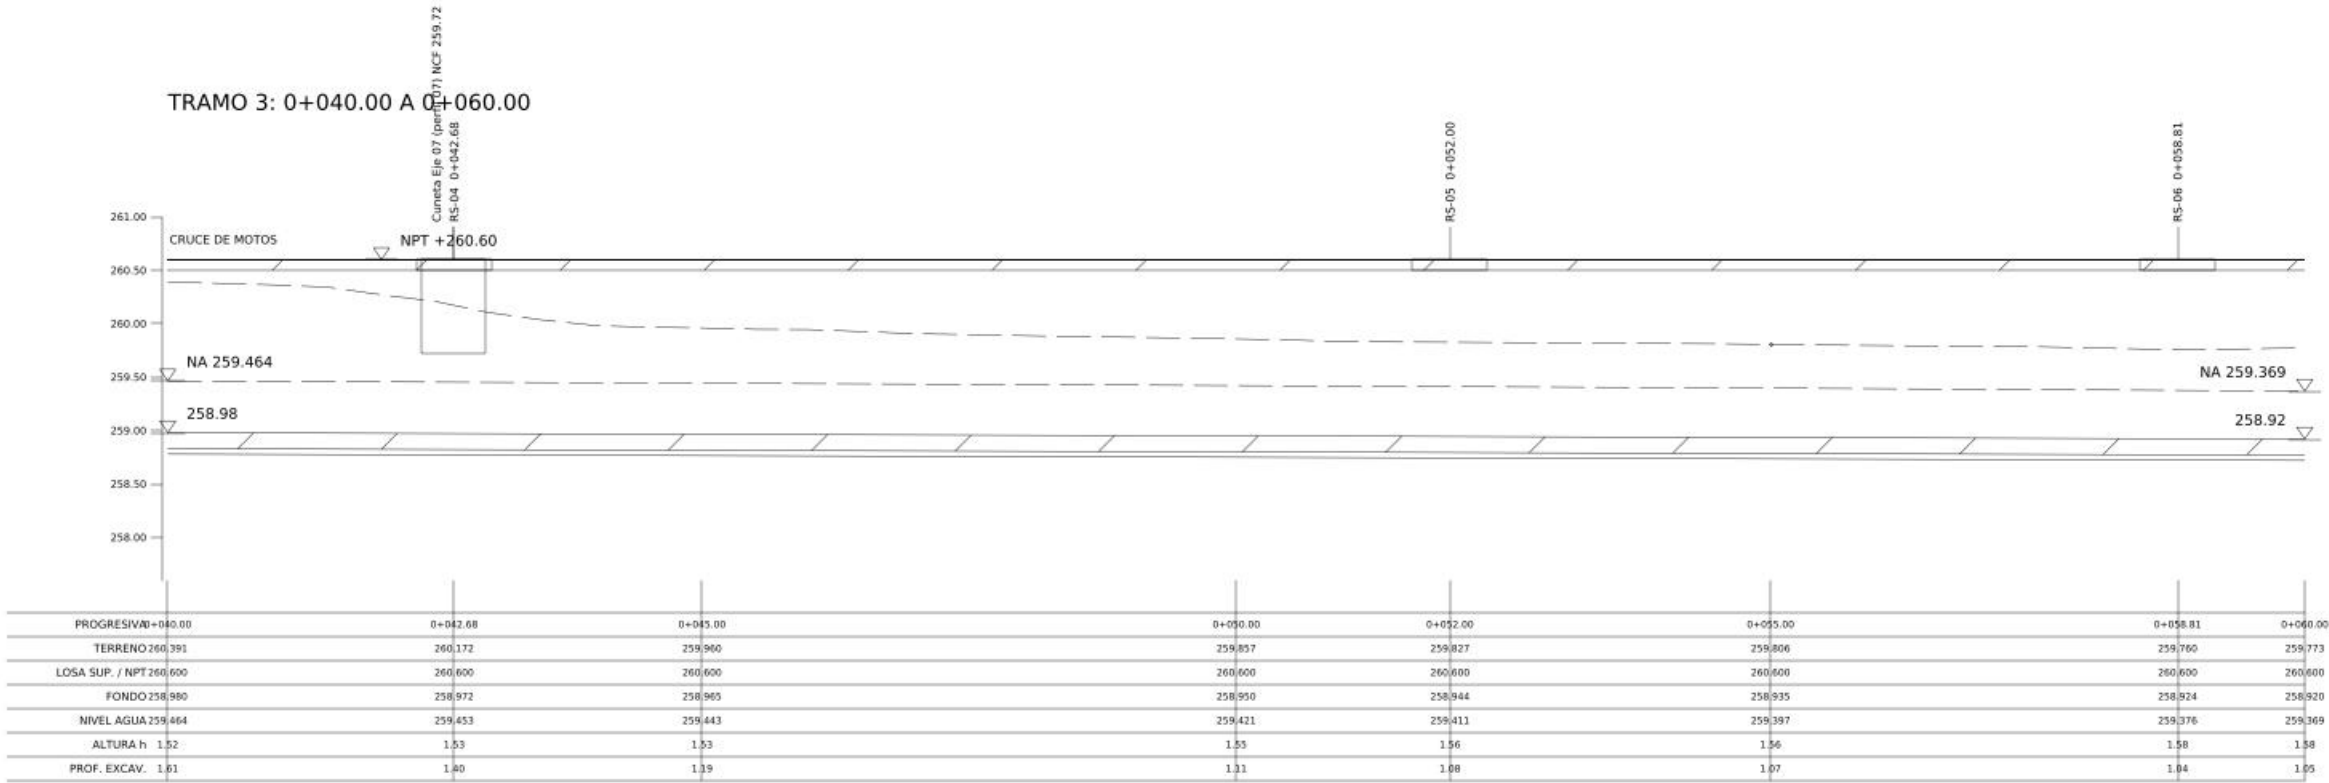


- LEYENDA
- concreto armado del colector
 - solado e=0.05
 - tapa de registro
 - nivel de agua de diseño
 - piso terminado +260.60
 - terreno existente
 - llegada de cuneta

- NOTAS
- Escala real: horizontal = vertical.
 - Cotas en m.s.n.m.; progresivas desde la caja CL.
 - Prof. excav. medida desde el terreno existente al fondo del solado.

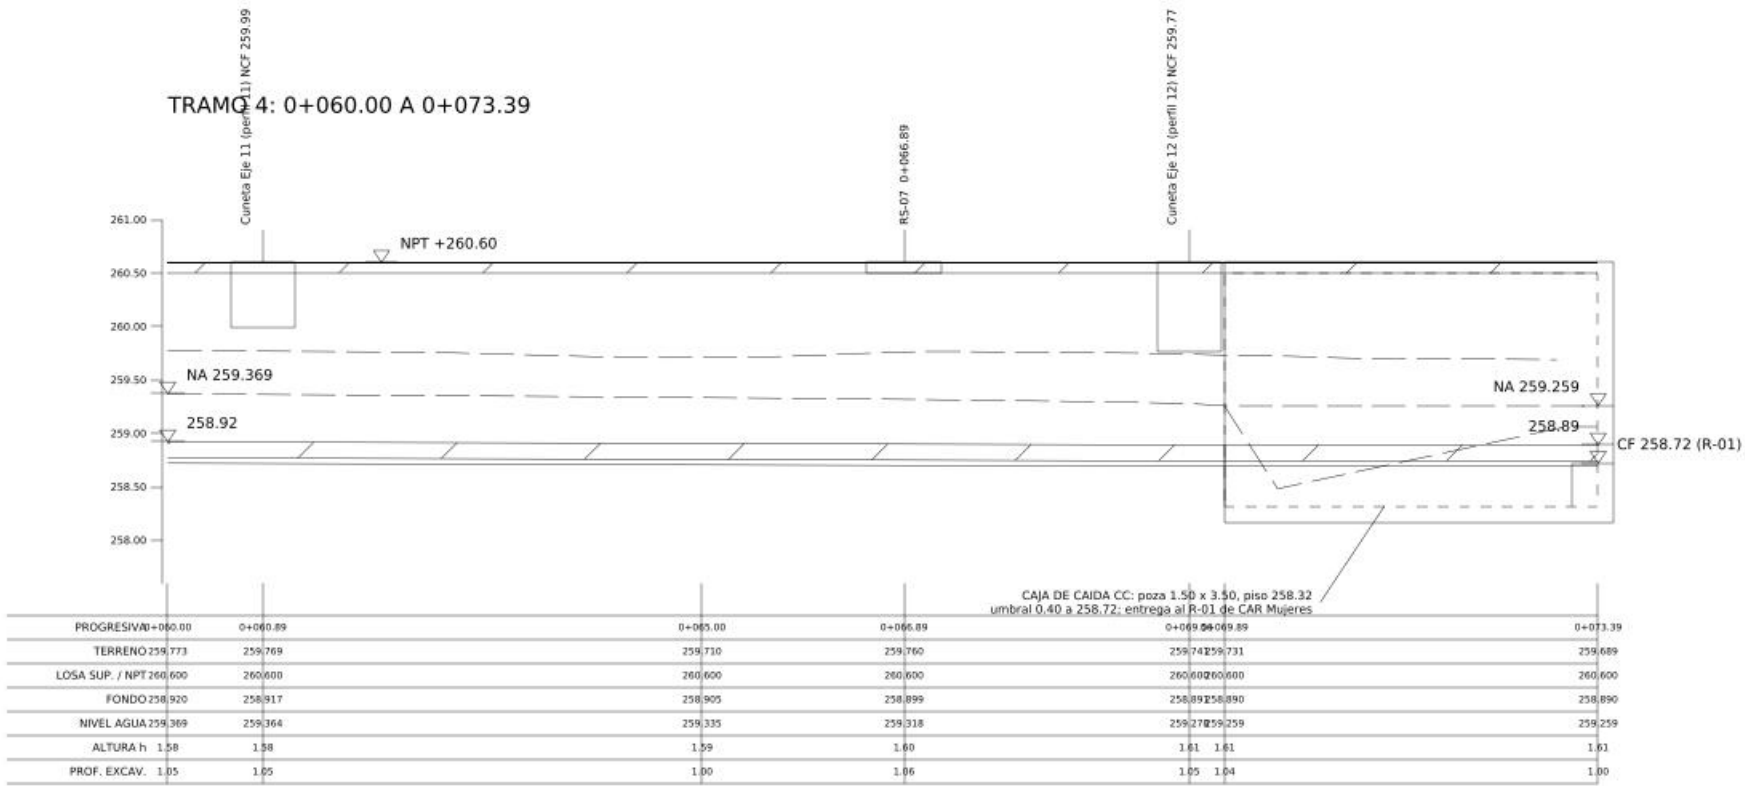


PROYECTO: CREACIÓN DEL SERVICIO DE ATENCIÓN INTEGRAL A MUJERES VÍCTIMAS DE VIOLENCIA EN EL HOGAR DE REFUGIO TEMPORAL MUJERES VIOLENTADAS, DISTRITO DE MORALES, PROVINCIA Y DEPARTAMENTO DE SAN MARTÍN - CUI N. 2675514 ENTIDAD: GERENCIA TERRITORIAL BAJO MAYO - TARAPOTO		
UBICACION: PREDIO RURAL LOS MANGOS - MORALES - SAN MARTÍN - SAN MARTÍN ESPECIALIDAD: INSTALACIONES SANITARIAS - DRENAJE PLUVIAL		
PLANO: PERFIL LONGITUDINAL DETALLADO DEL COLECTOR TRAMOS 3 Y 4 (0+040.00 - 0+073.39) - ESCALA REAL 1/50 (H = V)		
PROYECTISTA: _____ CIP: _____		
ELABORADO: HIDROCONSULT	ESCALA: 1/50	
REVISADO: _____	FECHA: OCT. 2026	LAMINA: _____
FIRMA Y SELLO: _____	REVISION: 00	DP-03E

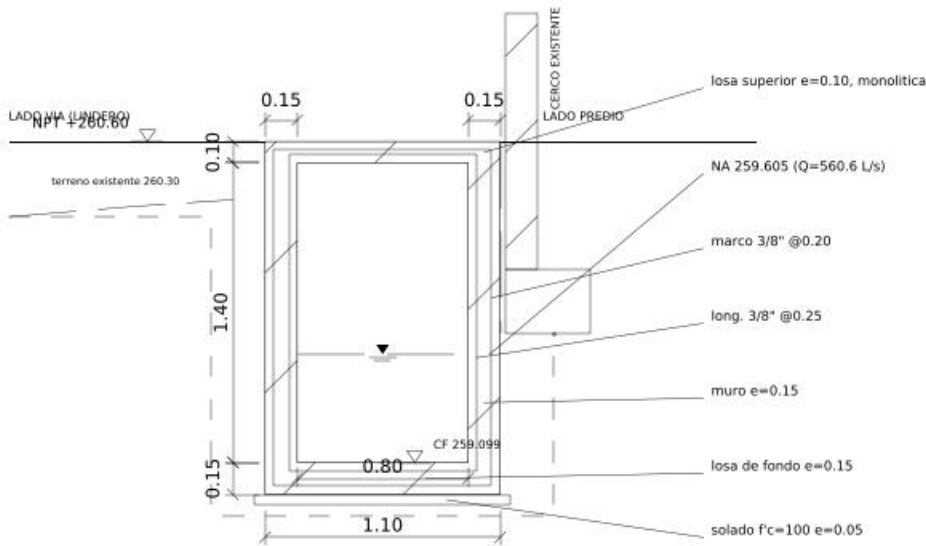


SECCION S-01

PROG. 0+000.50 - CF 259.099 - TRAMO NORMAL - ESC. 1/25

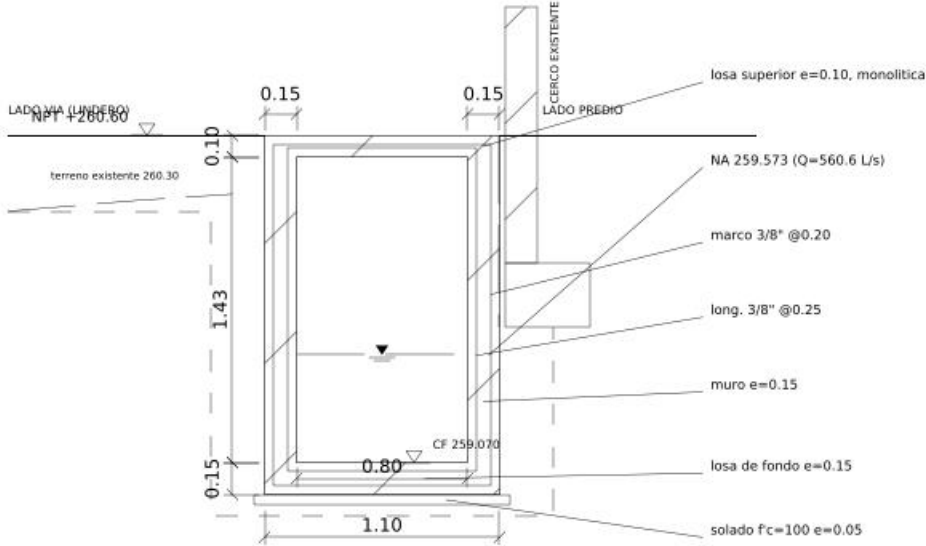


SECCION S-02

PROG. 0+010.00 - CF 259.070 - TRAMO NORMAL - ESC. 1/25

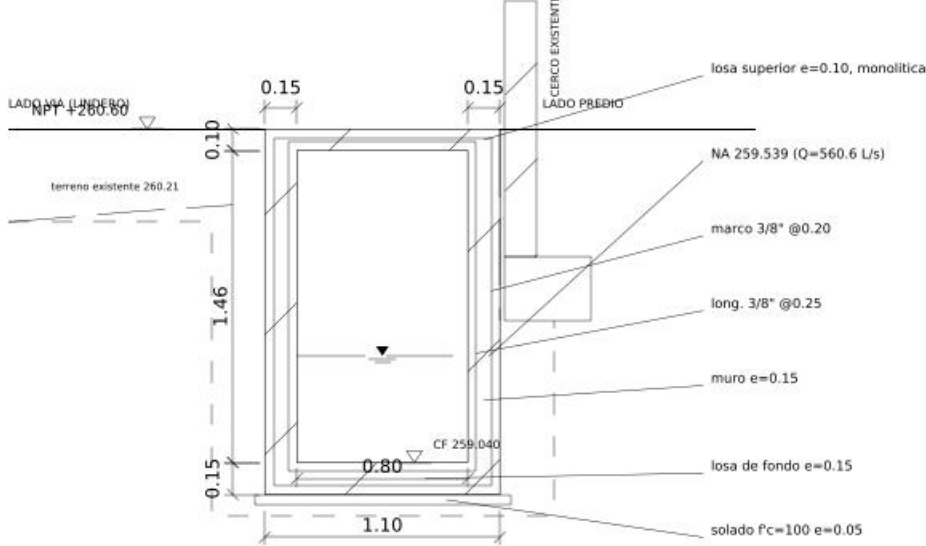

SECCION S-03

PROG. 0+020.00 - CF 259.040 - TRAMO NORMAL - ESC. 1/25

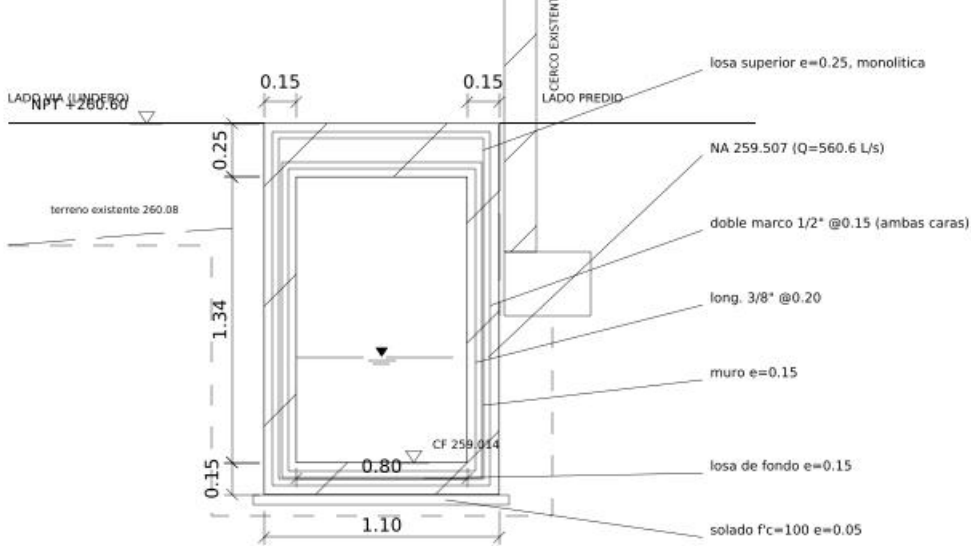

SECCION S-04

PROG. 0+028.80 - CF 259.014 - CRUCE DE CAMIONES - ESC. 1/25

LEYENDA

- concreto armado $f'c=210$ kg/cm²
- solado $f'c=100$ kg/cm²
- acero de refuerzo (marcos)
- acero longitudinal
- nivel de agua de diseño
- piso terminado +260.60
- terreno existente
- límite de excavación
- cercos perimetricos existentes

NOTAS

- Altura interior h según el perfil longitudinal (1.40 m en 0+000 a 1.61 m en el brink).
- Recubrimiento 0.04 m en muros y losa de fondo; 0.025 m en la losa superior del tramo normal; 0.04 m en el cruce de camiones.
- Junta de tecnopor de 1" entre el muro lado predio y el cimiento del cerco; junta de 1" entre la losa superior y el piso adyacente.
- El cruce de camiones (S-04) lleva losa superior $e=0.25$ y doble marco de 1/2"; el cruce de motos (S-05) marco de 3/8" @0.15.
- Los registros no se ubican dentro de los cruces vehiculares.

PROYECTO:
CREACIÓN DEL SERVICIO DE ATENCIÓN INTEGRAL A MUJERES VÍCTIMAS DE VIOLENCIA EN EL HOGAR DE REFUGIO TEMPORAL
MUJERES VIOLENTADAS, DISTRITO DE MORALES, PROVINCIA Y DEPARTAMENTO DE SAN MARTÍN - CUI N. 2675514
ENTIDAD: GERENCIA TERRITORIAL BAJO MAYO - TARAPOTO

UBICACIÓN: PREDIO RURAL LOS MANGOS - MORALES - SAN MARTÍN - SAN MARTÍN
ESPECIALIDAD: INSTALACIONES SANITARIAS - DRENAJE PLUVIAL

PLANO: SECCIONES TRANSVERSALES DEL COLECTOR
SECCIONES S-01 A S-04 CON DISTRIBUCIÓN DE ACERO - ESC. 1/25

PROYECTISTA: _____ CIP: _____

ELABORADO: HIDROCONSULT

ESCALA: 1/25


REVISADO: _____

FECHA: OCT. 2026

LAMINA:


FIRMA Y SELLO:

REVISION: 00

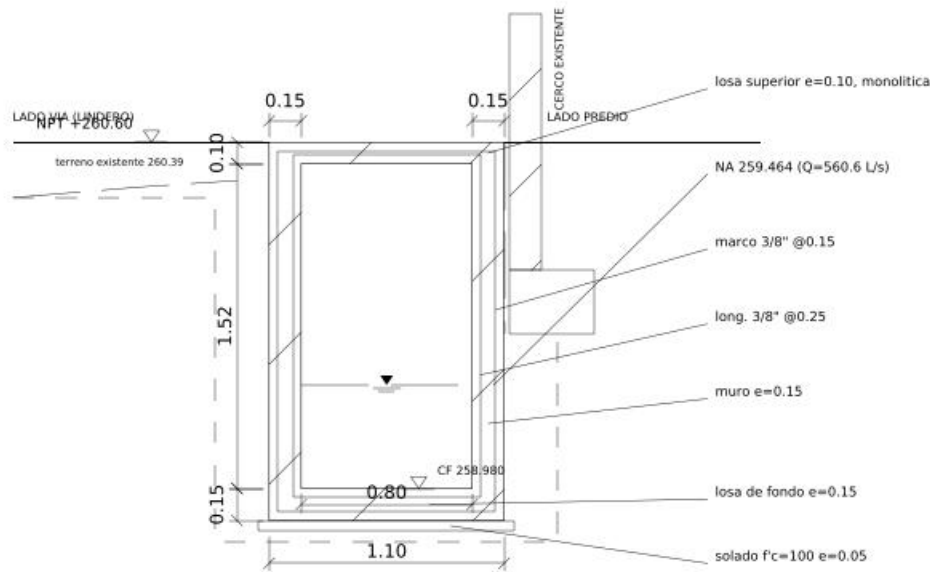


SECCION S-05

PROG. 0+040.00 - CF 258.980 - CRUCE DE MOTOS - ESC. 1/25

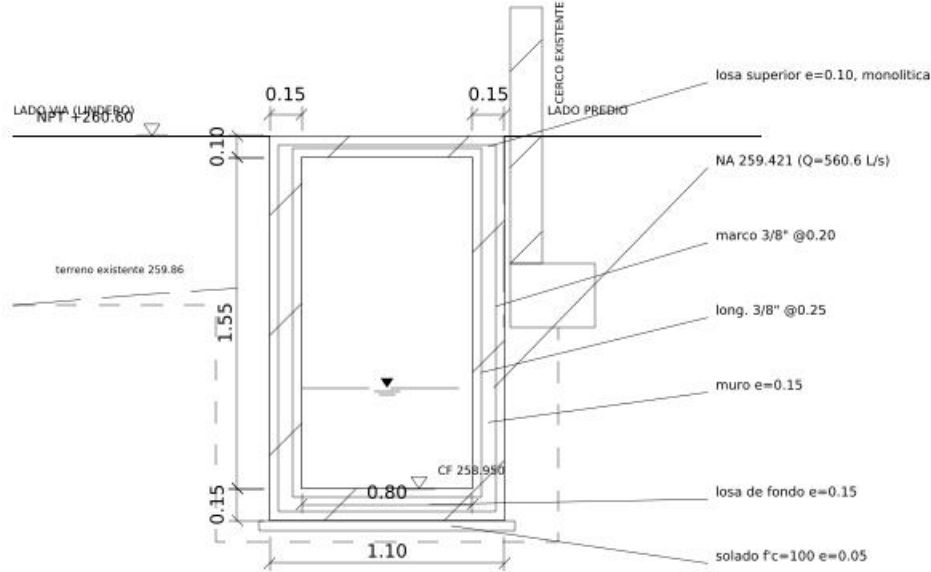


SECCION S-06

PROG. 0+050.00 - CF 258.950 - TRAMO NORMAL - ESC. 1/25

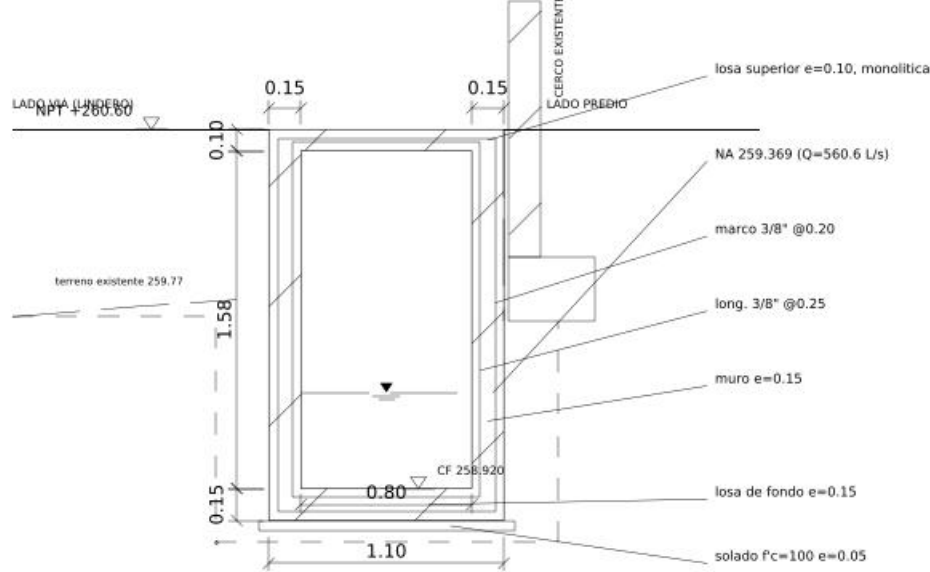

SECCION S-07

PROG. 0+060.00 - CF 258.920 - TRAMO NORMAL - ESC. 1/25

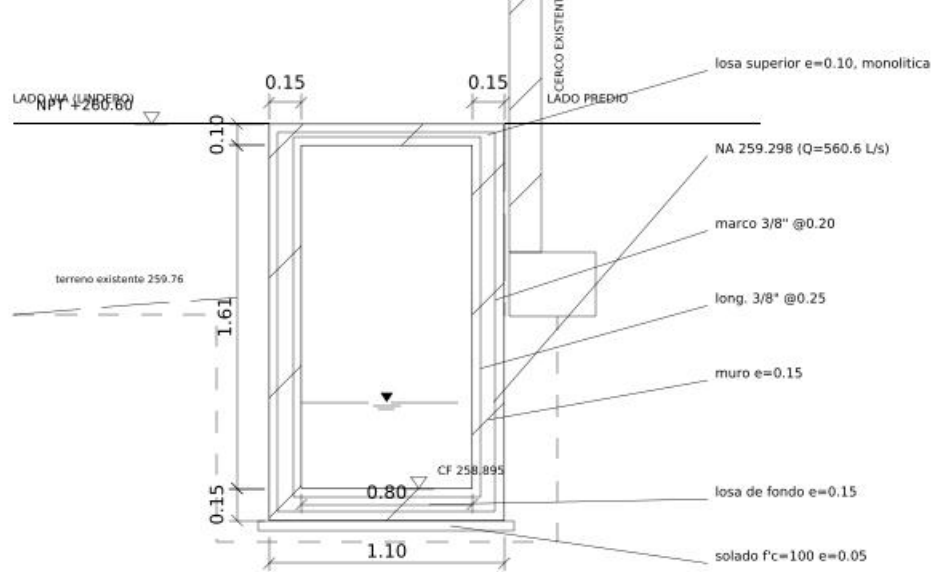

SECCION S-08

PROG. 0+068.50 - CF 258.895 - TRAMO NORMAL - ESC. 1/25


LEYENDA

- concreto armado f'c=210 kg/cm²
- solado f'c=100 kg/cm²
- acero de refuerzo (marcos)
- acero longitudinal
- nivel de agua de diseno
- piso terminado +260.60
- terreno existente
- limite de excavacion
- cerco perimetrico existente

NOTAS

- Altura interior h segun el perfil longitudinal (1.40 m en 0+000 a 1.61 m en el brink).
- Recubrimiento 0.04 m en muros y losa de fondo; 0.025 m en la losa superior del tramo normal; 0.04 m en el cruce de camiones.
- Junta de tecnopor de 1" entre el muro lado predio y el cimiento del cerco; junta de 1" entre la losa superior y el piso adyacente.
- El cruce de camiones (S-04) lleva losa superior e=0.25 y doble marco de 1/2"; el cruce de motos (S-05) marco de 3/8" @0.15.
- Los registros no se ubican dentro de los cruces vehiculares.


PROYECTO: CREACION DEL SERVICIO DE ATENCION INTEGRAL A MUJERES VICTIMAS DE VIOLENCIA EN EL HOGAR DE REFUGIO TEMPORAL MUJERES VIOLENTADAS, DISTRITO DE MORALES, PROVINCIA Y DEPARTAMENTO DE SAN MARTIN - CUI N. 2675514 ENTIDAD: GERENCIA TERRITORIAL BAJO MAYO - TARAPOTO		
UBICACION: PREDIO RURAL LOS MANGOS - MORALES - SAN MARTIN - SAN MARTIN ESPECIALIDAD: INSTALACIONES SANITARIAS - DRENAJE PLUVIAL		
PLANO: SECCIONES TRANSVERSALES DEL COLECTOR SECCIONES S-05 A S-08 CON DISTRIBUCION DE ACERO - ESC. 1/25		
PROYECTISTA: _____ CIP: _____		
ELABORADO: HIDROCONSULT	ESCALA: 1/25	
REVISADO: _____	FECHA: OCT. 2026	LAMINA:
FIRMA Y SELLO:	REVISION: 00	

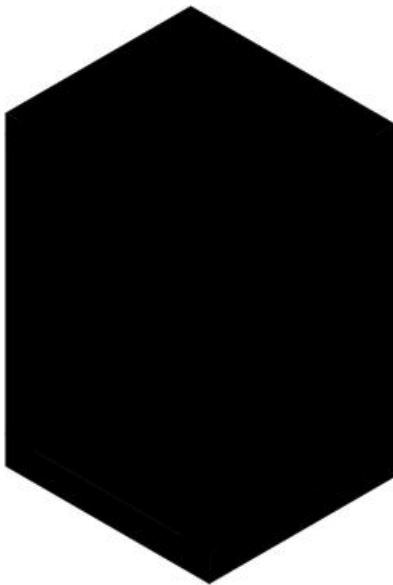

CF 259.099
losa superior 260.60
NA 259.605
marco 3/8" @0.20
long. 3/8" @0.25
registro: tapa 0.68 x 0.68, luz 0.60
h interior 1.40 m

ISOMETRICO S-01


PROG. 0+000.50 - interior 0.80 x 1.40 m - TRAMO NORMAL

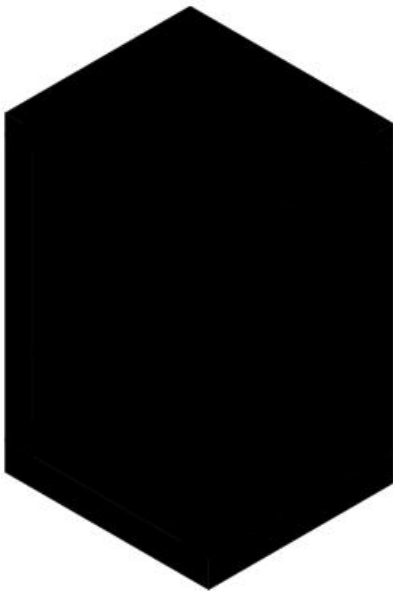

CF 259.070
losa superior 260.60
NA 259.573
marco 3/8" @0.20
long. 3/8" @0.25
registro: tapa 0.68 x 0.68, luz 0.60
h interior 1.43 m

ISOMETRICO S-02


PROG. 0+010.00 - interior 0.80 x 1.43 m - TRAMO NORMAL

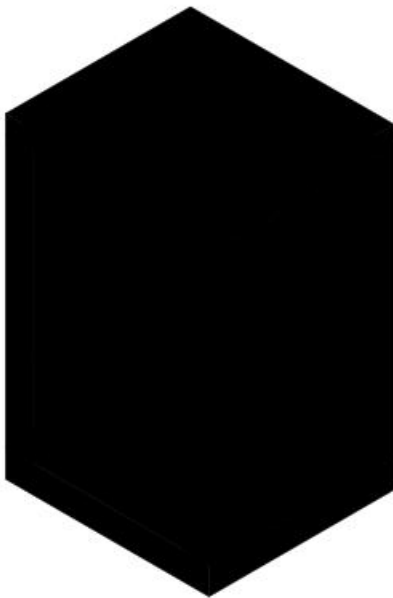

CF 259.040
losa superior 260.60
NA 259.539
marco 3/8" @0.20
long. 3/8" @0.25
registro: tapa 0.68 x 0.68, luz 0.60
h interior 1.46 m

ISOMETRICO S-03

PROG. 0+020.00 - interior 0.80 x 1.46 m - TRAMO NORMAL

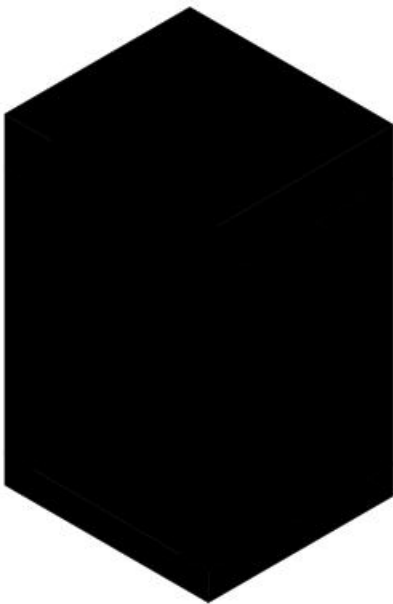

CF 259.014
losa superior 260.60
NA 259.507
doble marco 1/2" @0.15
long. 3/8" @0.20
registro: tapa 0.68 x 0.68, luz 0.60
h interior 1.34 m

ISOMETRICO S-04

PROG. 0+028.80 - interior 0.80 x 1.34 m - CRUCE DE CAMIONES


LEYENDA

- concreto armado (cara superior)
- concreto armado (cara frontal / corte)
- concreto armado (cara lateral)
- tapa de registro removible
- agua (nivel de diseno)
- acero en la cara de corte

NOTAS

- 1. Vistas isometricas sin escala; medidas reales en las laminas DP-04 y DP-06.
- 2. Se muestra 1.00 m de colector cortado en la progresiva indicada.


PROYECTO: CREACION DEL SERVICIO DE ATENCION INTEGRAL A MUJERES VICTIMAS DE VIOLENCIA EN EL HOGAR DE REFUGIO TEMPORAL MUJERES VIOLENTADAS, DISTRITO DE MORALES, PROVINCIA Y DEPARTAMENTO DE SAN MARTIN - CUI N. 2675514 ENTIDAD: GERENCIA TERRITORIAL BAJO MAYO - TARAPOTO		
UBICACION: PREDIO RURAL LOS MANGOS - MORALES - SAN MARTIN - SAN MARTIN ESPECIALIDAD: INSTALACIONES SANITARIAS - DRENAJE PLUVIAL		
PLANO: ISOMETRICOS DE LAS SECCIONES TRANSVERSALES SECCIONES S-01 A S-04 - TRAMOS DE 1.00 m CON REGISTRO Y ACERO EN LA CARA DE CORTE		
PROYECTISTA: _____ CIP: _____		
ELABORADO: HIDROCONSULT	ESCALA: 1/25	
REVISADO: _____	FECHA: OCT. 2026	LAMINA:
FIRMA Y SELLO:	REVISION: 00	

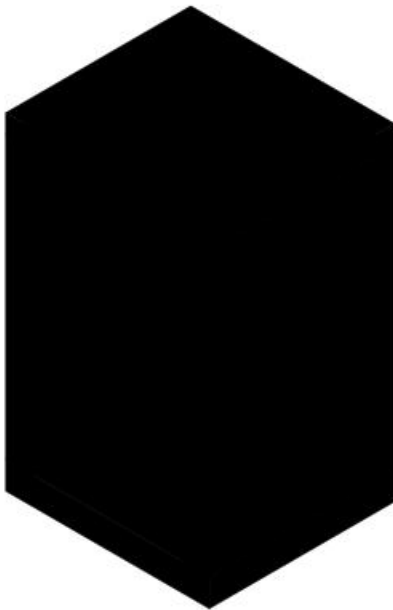

CF 258.980
losa superior 260.60
NA 259.464
marco 3/8" @0.15
long. 3/8" @0.25
registro: tapa 0.68 x 0.68, luz 0.60
h interior 1.52 m

ISOMETRICO S-05


PROG. 0+040.00 - interior 0.80 x 1.52 m - CRUCE DE MOTOS

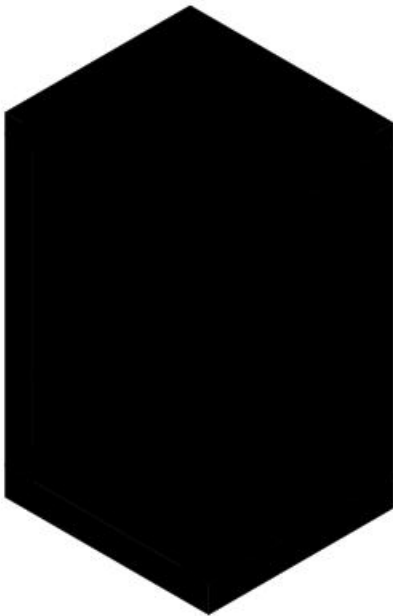

CF 258.950
losa superior 260.60
NA 259.421
marco 3/8" @0.20
long. 3/8" @0.25
registro: tapa 0.68 x 0.68, luz 0.60
h interior 1.55 m

ISOMETRICO S-06


PROG. 0+050.00 - interior 0.80 x 1.55 m - TRAMO NORMAL

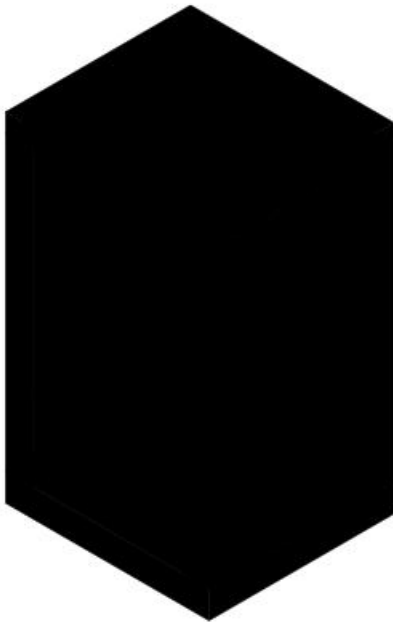

CF 258.920
losa superior 260.60
NA 259.369
marco 3/8" @0.20
long. 3/8" @0.25
registro: tapa 0.68 x 0.68, luz 0.60
h interior 1.58 m

ISOMETRICO S-07

PROG. 0+060.00 - interior 0.80 x 1.58 m - TRAMO NORMAL

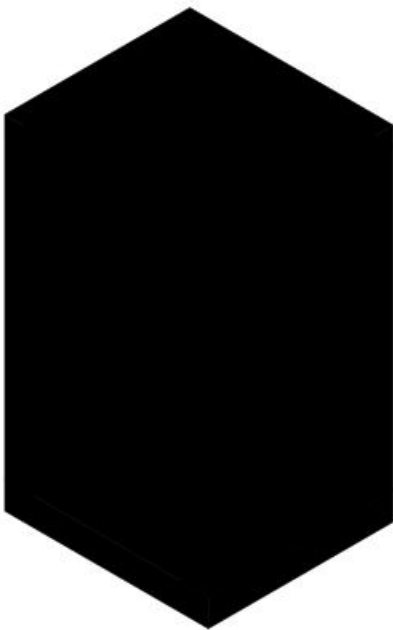

CF 258.895
losa superior 260.60
NA 259.298
marco 3/8" @0.20
long. 3/8" @0.25
registro: tapa 0.68 x 0.68, luz 0.60
h interior 1.61 m

ISOMETRICO S-08

PROG. 0+068.50 - interior 0.80 x 1.61 m - TRAMO NORMAL


LEYENDA

- concreto armado (cara superior)
- concreto armado (cara frontal / corte)
- concreto armado (cara lateral)
- tapa de registro removible
- agua (nivel de diseno)
- acero en la cara de corte

NOTAS

- Vistas isometricas sin escala; medidas reales en las laminas DP-04 y DP-06.
- Se muestra 1.00 m de colector cortado en la progresiva indicada.

PROYECTO: CREACION DEL SERVICIO DE ATENCION INTEGRAL A MUJERES VICTIMAS DE VIOLENCIA EN EL HOGAR DE REFUGIO TEMPORAL MUJERES VIOLENTADAS, DISTRITO DE MORALES, PROVINCIA Y DEPARTAMENTO DE SAN MARTIN - CUI N. 2675514 ENTIDAD: GERENCIA TERRITORIAL BAJO MAYO - TARAPOTO		
UBICACION: PREDIO RURAL LOS MANGOS - MORALES - SAN MARTIN - SAN MARTIN ESPECIALIDAD: INSTALACIONES SANITARIAS - DRENAJE PLUVIAL		
PLANO: ISOMETRICOS DE LAS SECCIONES TRANSVERSALES SECCIONES S-05 A S-08 - TRAMOS DE 1.00 m CON REGISTRO Y ACERO EN LA CARA DE CORTE		
PROYECTISTA: _____ CIP: _____		
ELABORADO: HIDROCONSULT	ESCALA: 1/25	
REVISADO: _____	FECHA: OCT. 2026	LAMINA:
FIRMA Y SELLO:	REVISION: 00	

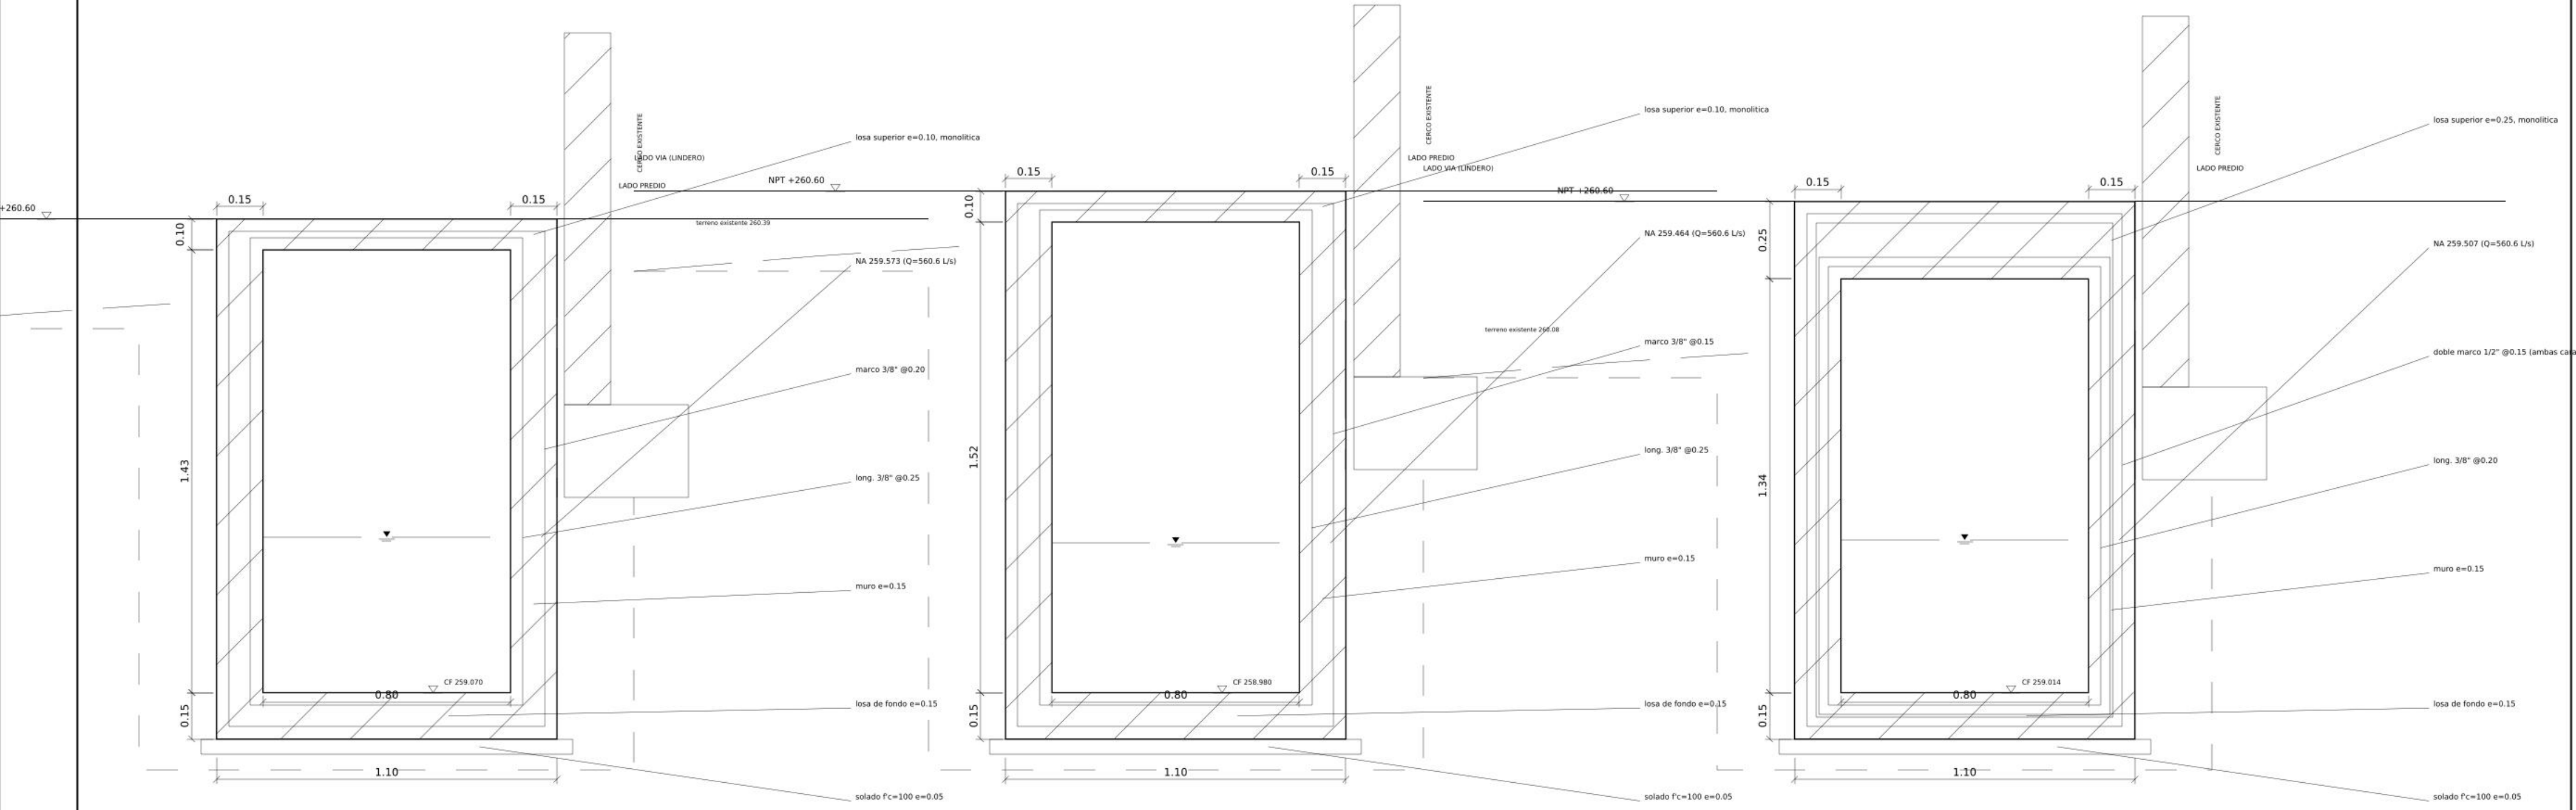

SECCION TIPICA A-A: TRAMO NORMAL

ESC. 1/10 - h segun perfil (aqui 1.43 m, prog. 0+010.00)

SECCION TIPICA B-B: CRUCE DE MOTOS

ESC. 1/10 - h segun perfil (aqui 1.52 m, prog. 0+040.00)

SECCION TIPICA C-C: CRUCE DE CAMIONES

ESC. 1/10 - h segun perfil (aqui 1.34 m, prog. 0+028.80)


LEYENDA

- concreto armado $f_c=210$ kg/cm²
- solado $f_c=100$ kg/cm² $e=0.05$
- marco de acero (barra cerrada)
- acero longitudinal
- nivel de agua de diseno
- cercos perimetricos existentes
- jointa de tecnopor 1"

NOTAS


- Muros $e=0.15$ en todo el tramo; losa de fondo $e=0.15$; losa superior $e=0.10$ ($e=0.25$ en el cruce de camiones).
- En el cruce de camiones el acero de muros y losas va en ambas caras (doble marco 1/2" @0.15); losa de fondo tambien $e=0.25$ en ese tramo.
- El tramo diagonal (quiebres a 45 grados) tiene la seccion tipica A-A; en las esquinas las barras llevan ganchos de 0.40 m (ver DP-09).
- Empalme de las cunetas: ver DP-06C. Registro, tapa y junta: ver DP-06B.

PROYECTO: CREACION DEL SERVICIO DE ATENCION INTEGRAL A MUJERES VICTIMAS DE VIOLENCIA EN EL HOGAR DE REFUGIO TEMPORAL MUJERES VIOLENTADAS, DISTRITO DE MORALES, PROVINCIA Y DEPARTAMENTO DE SAN MARTIN - CUI N. 2675514 ENTIDAD: GERENCIA TERRITORIAL BAJO MAYO - TARAPOTO		
UBICACION: PREDIO RURAL LOS MANGOS - MORALES - SAN MARTIN - SAN MARTIN ESPECIALIDAD: INSTALACIONES SANITARIAS - DRENAJE PLUVIAL		
PLANO: DETALLES TIPICOS DEL COLECTOR SECCIONES TIPICAS: TRAMO NORMAL, CRUCE DE MOTOS, CRUCE DE CAMIONES Y TRAMO DIAGONAL - ESC. 1/10		
PROYECTISTA: _____ CIP: _____		
ELABORADO: HIDROCONSULT	ESCALA: 1/10	
REVISADO: _____	FECHA: OCT. 2026	LAMINA:
FIRMA Y SELLO:	REVISION: 00	

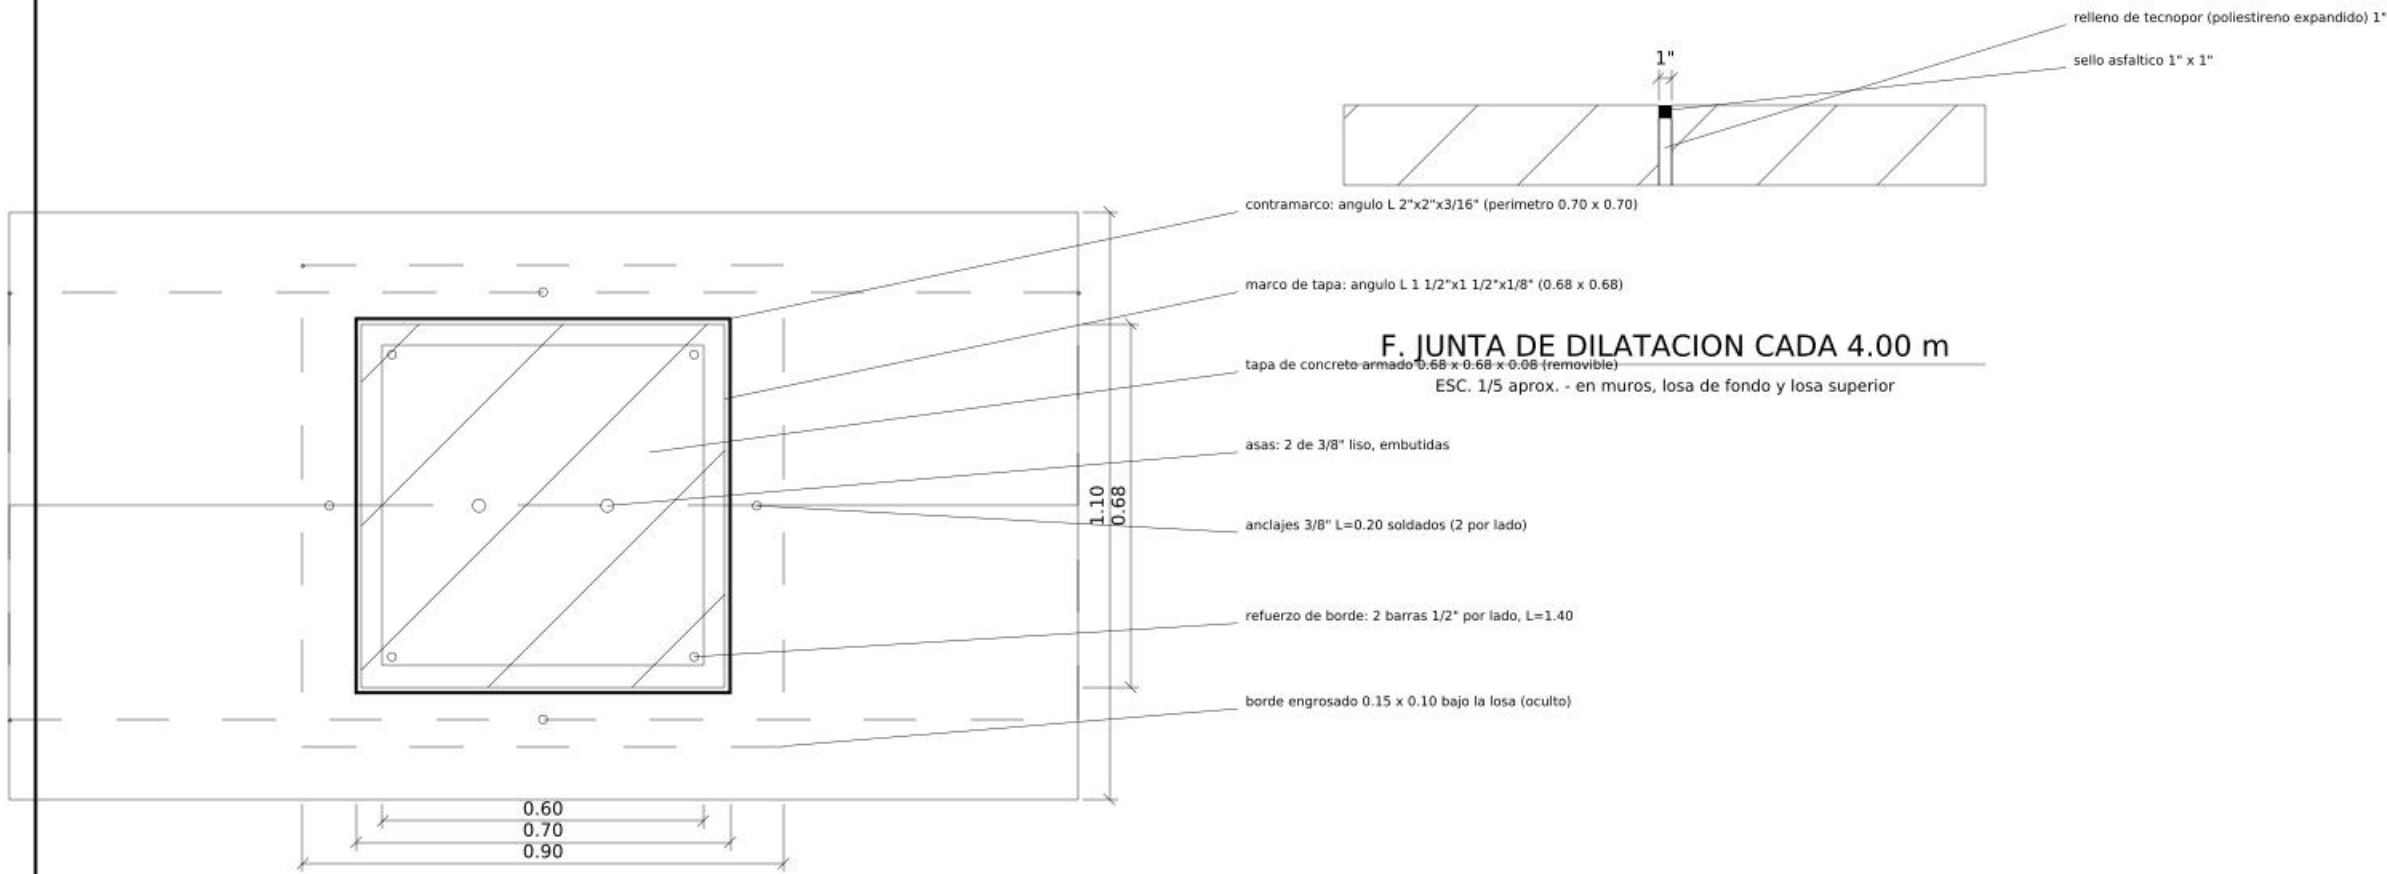


A. REGISTRO DE LIMPIEZA - PLANTA

ESC. 1/10 - 7 und (RS-01 a RS-07) + 3 en las cajas CL y CC

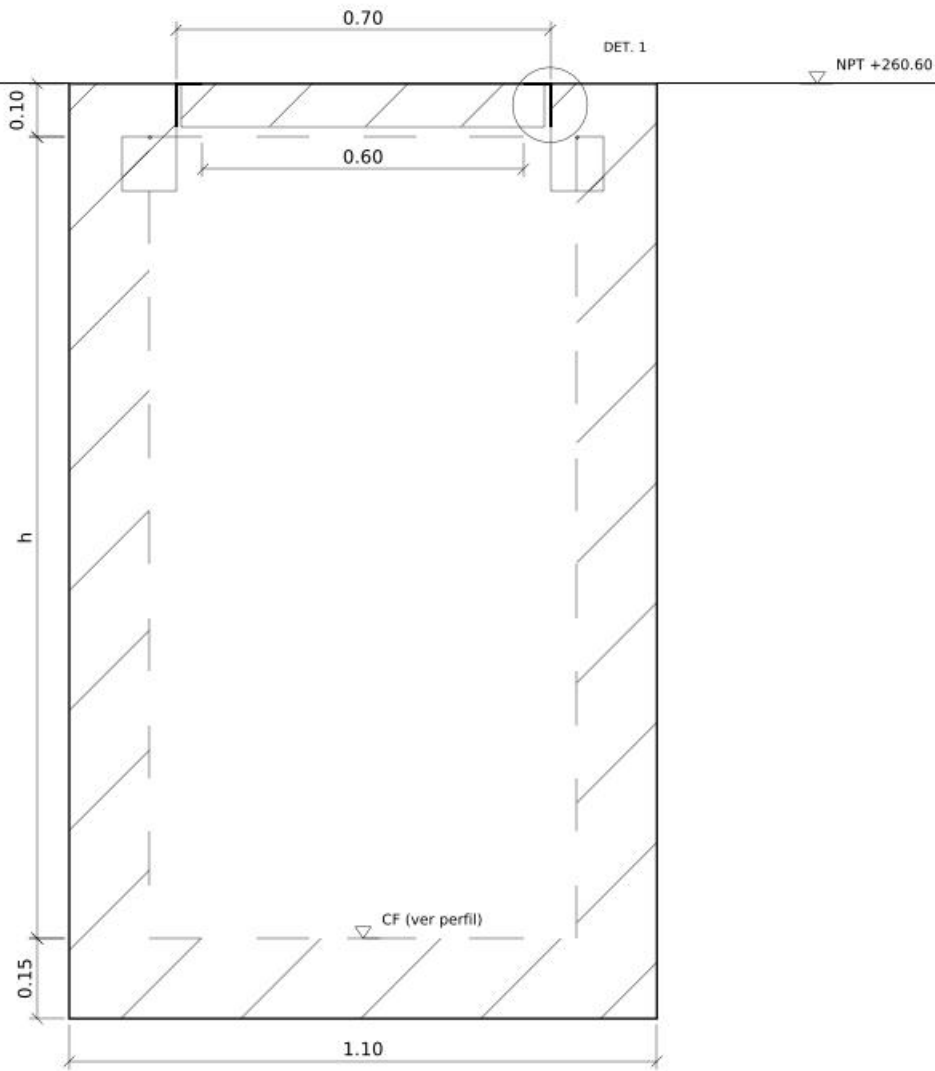


B. CORTE A-A POR EL REGISTRO

ESC. 1/10

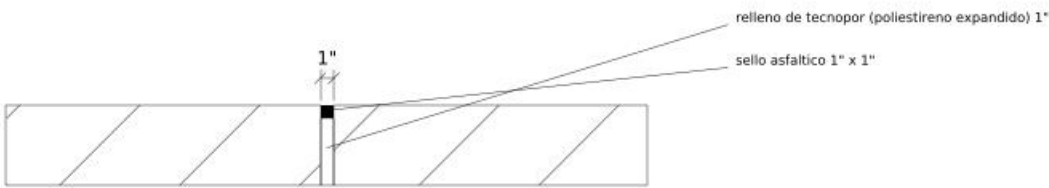


F. JUNTA DE DILATACION CADA 4.00 m

ESC. 1/5 aprox. - en muros, losa de fondo y losa superior

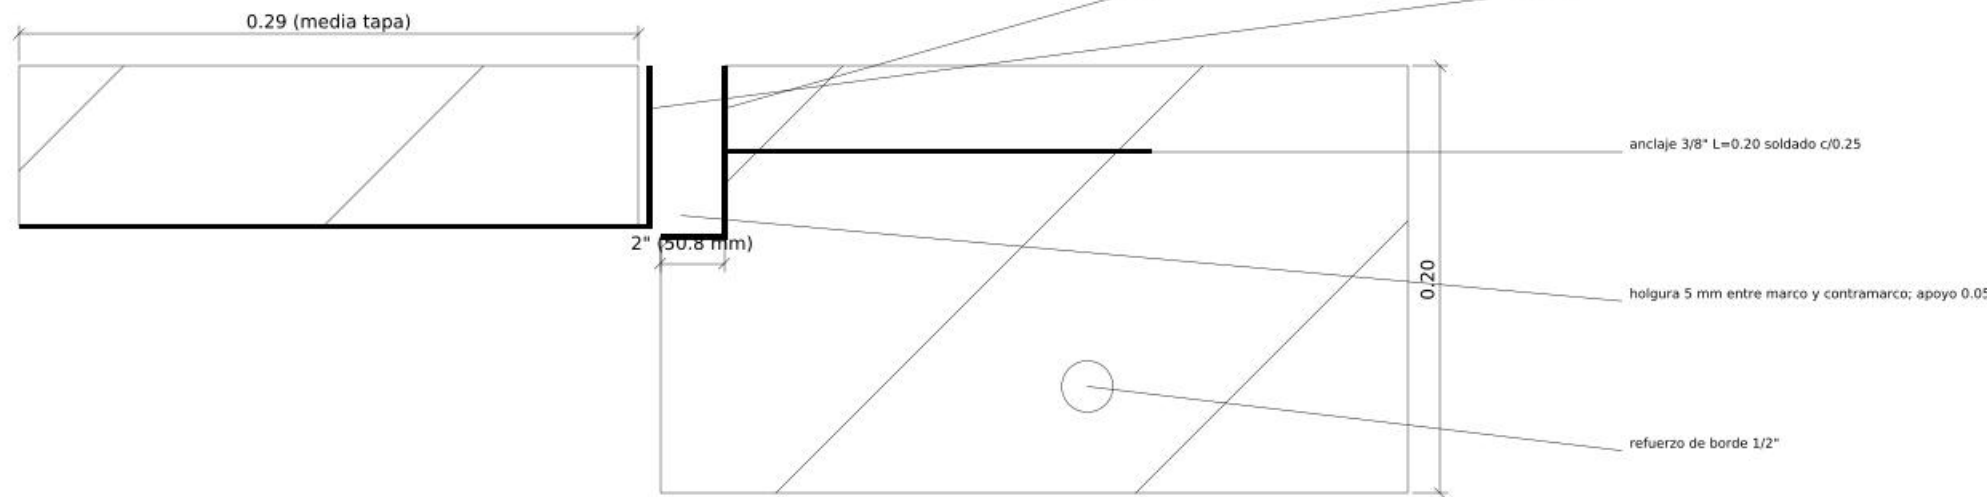


C. DETALLE 1: APOYO DE TAPA

ESC. 1/2.5

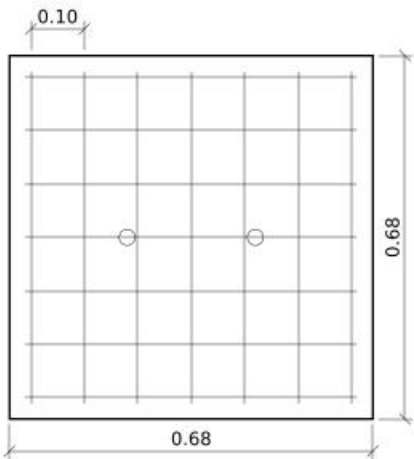

D. TAPA - ARMADO

7 + 7 barras 3/8" @0.10, L=0.62; asas 3/8" liso

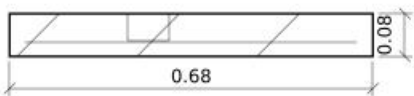

D. TAPA - CORTE

concreto f'c=210 kg/cm2 - peso aprox. 95 kg


MATERIALES POR REGISTRO

Contramarco angulo L 2"x2"x3/16": 4 x 0.70 = 2.80 m (10.2 kg); anclajes 3/8" L=0.20: 8 und
Marco de tapa angulo L 1 1/2"x1 1/2"x1/8": 4 x 0.68 = 2.72 m (5.0 kg)
Acero tapa 3/8" @0.10: 14 x 0.62 = 8.68 m (4.9 kg); asas 3/8" liso: 2 x 0.40 m
Concreto tapa f'c=210: 0.68 x 0.68 x 0.08 = 0.037 m3
Refuerzo de borde 1/2": 8 x 1.40 = 11.20 m (11.1 kg); borde engrosado: perimetro 3.00 x 0.15 x 0.10 = 0.045 m3

LEYENDA

concreto armado f'c=210 kg/cm2
angulos metalicos (marco y contramarco)
tapa removible
acero de refuerzo
junta de dilatacion / tecnopor

PROYECTO: CREACION DEL SERVICIO DE ATENCION INTEGRAL A MUJERES VICTIMAS DE VIOLENCIA EN EL HOGAR DE REFUGIO TEMPORAL MUJERES VIOLENTADAS, DISTRITO DE MORALES, PROVINCIA Y DEPARTAMENTO DE SAN MARTIN - CUI N. 2675514 ENTIDAD: GERENCIA TERRITORIAL BAJO MAYO - TARAPOTO		
UBICACION: PREDIO RURAL LOS MANGOS - MORALES - SAN MARTIN - SAN MARTIN ESPECIALIDAD: INSTALACIONES SANITARIAS - DRENAJE PLUVIAL		
PLANO: DETALLES DE REGISTRO DE LIMPIEZA, TAPA, MARCO Y CONTRAMARCO REGISTRO CON TAPA REMOVIBLE, ANGULOS METALICOS, EMPALME DE CUNETA Y JUNTA DE DILATACION		
PROYECTISTA: _____ CIP: _____		
ELABORADO: HIDROCONSULT	ESCALA: 1/10	
REVISADO: _____	FECHA: OCT. 2026	LAMINA: _____
FIRMA Y SELLO: _____	REVISION: 00	DP-06E

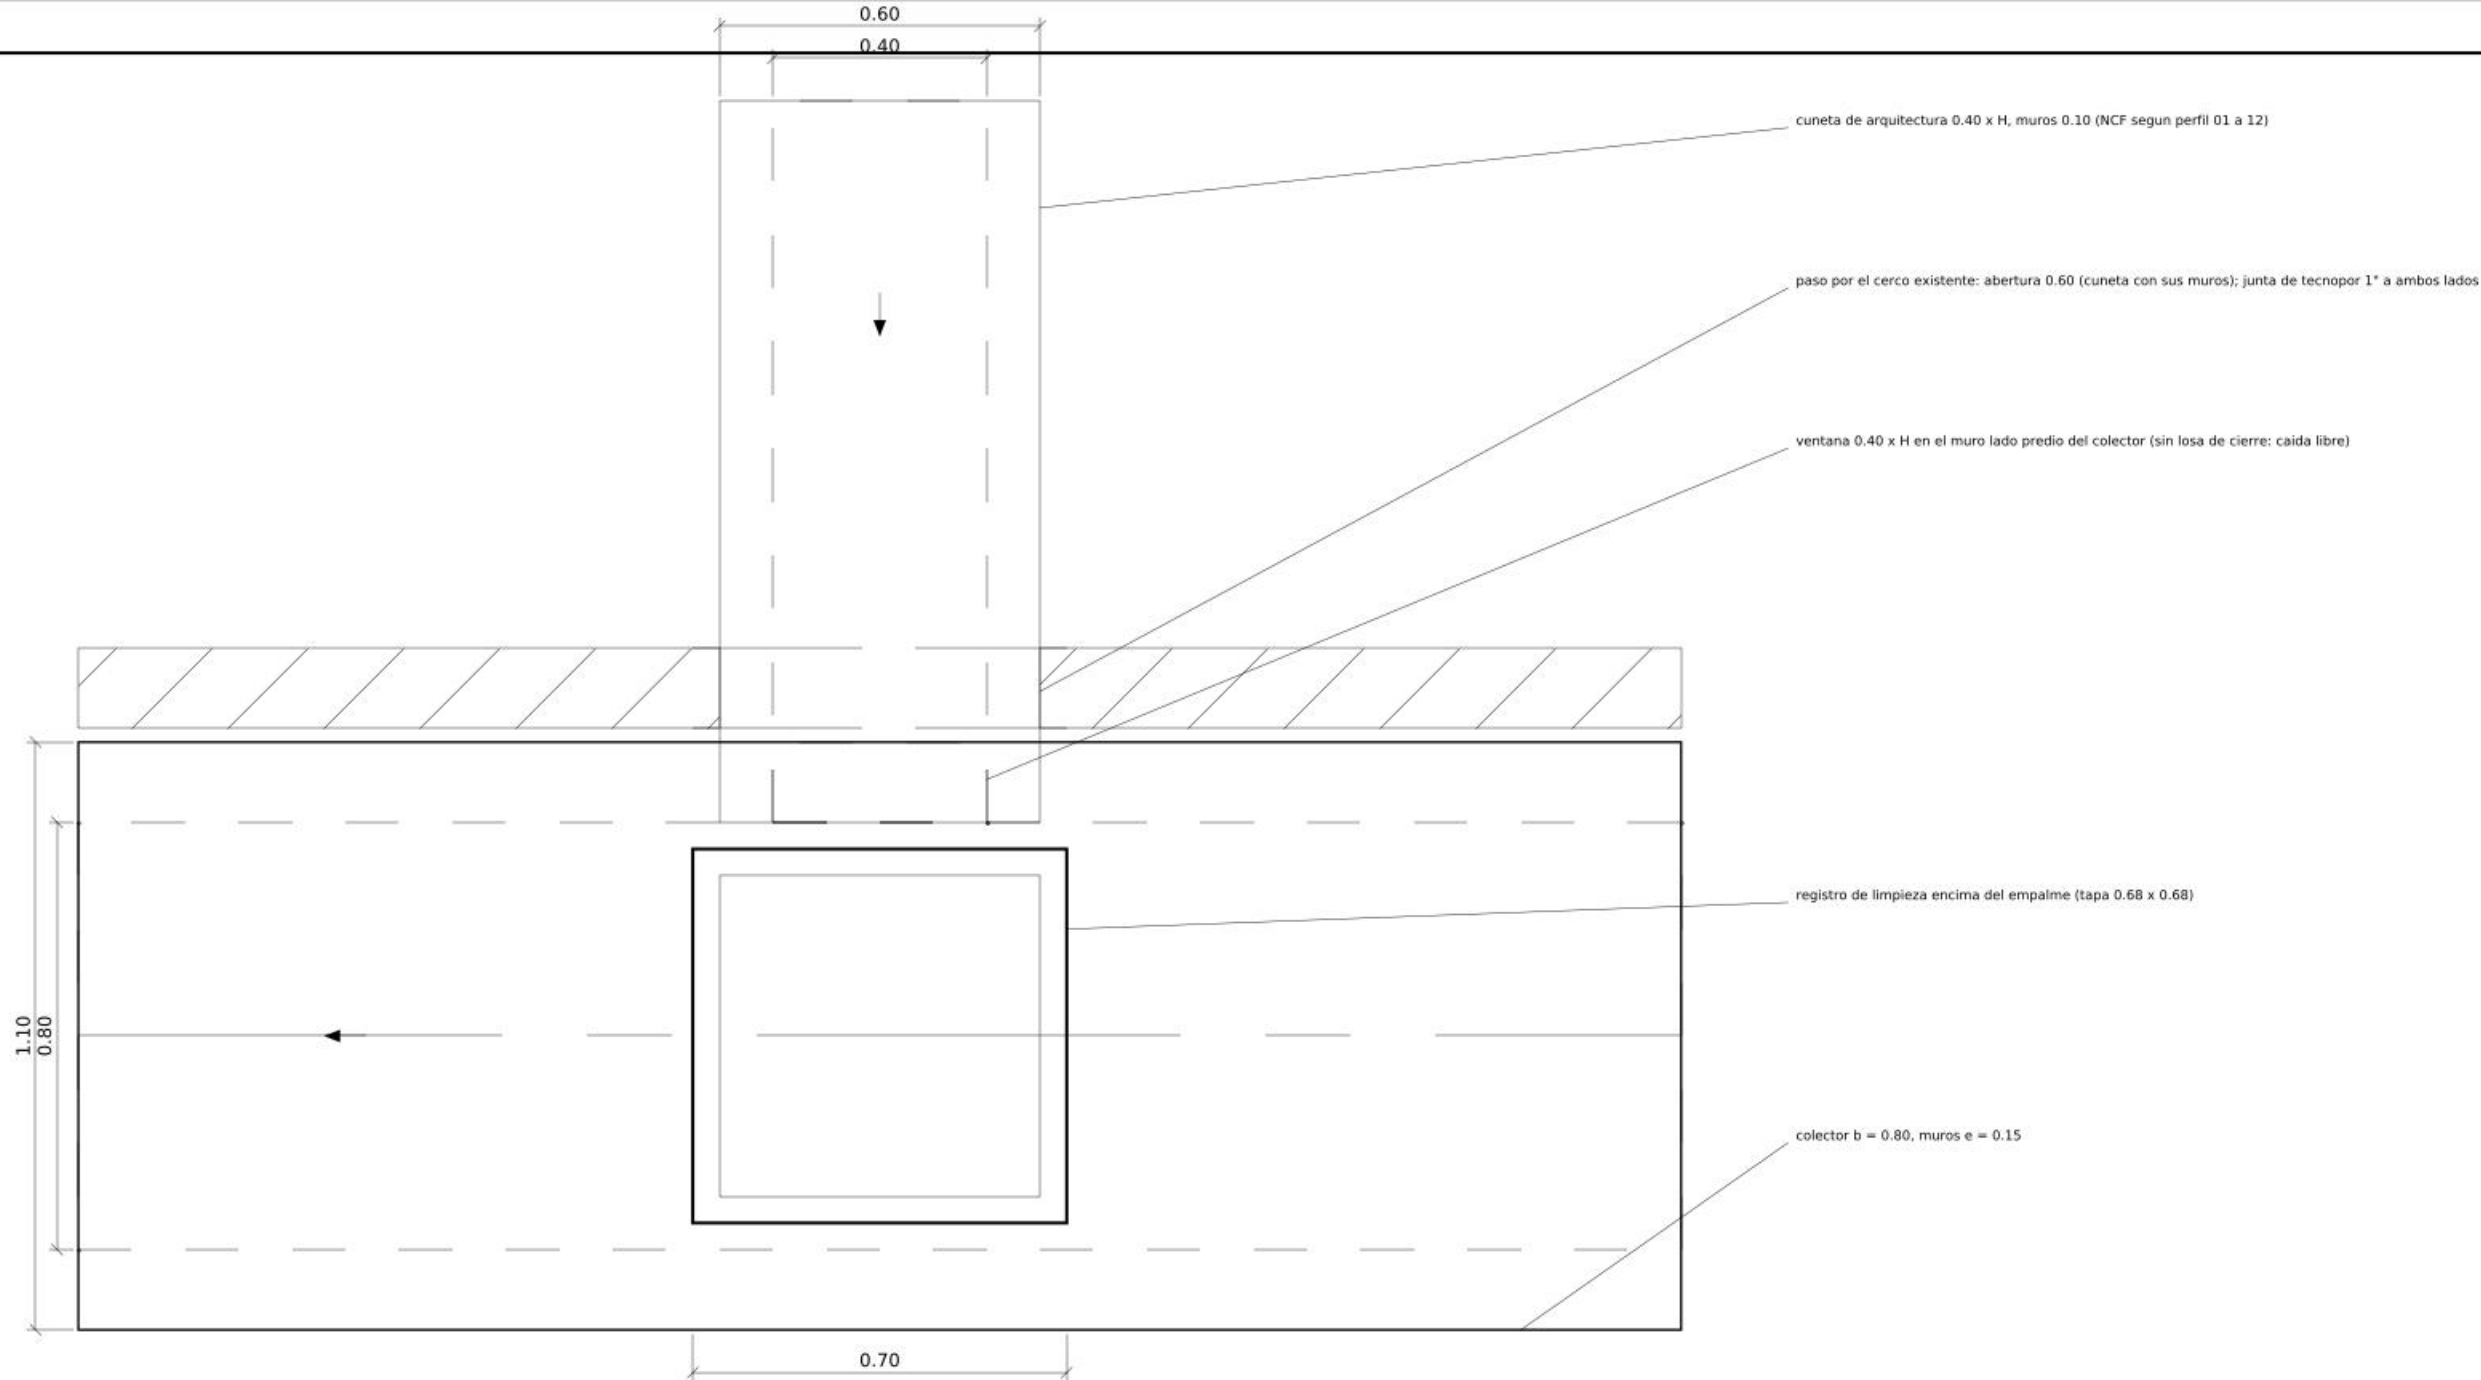


E1. EMPALME DE CUNETA - PLANTA

ESC. 1/10 - losa superior retirada para mostrar la ventana

LEYENDA

- concreto armado del colector $f_c=210$
- cuneta y cerco existentes (arquitectura)
- cuneta de arquitectura
- junta de tecnopor 1"
- nivel de agua
- sentido del flujo

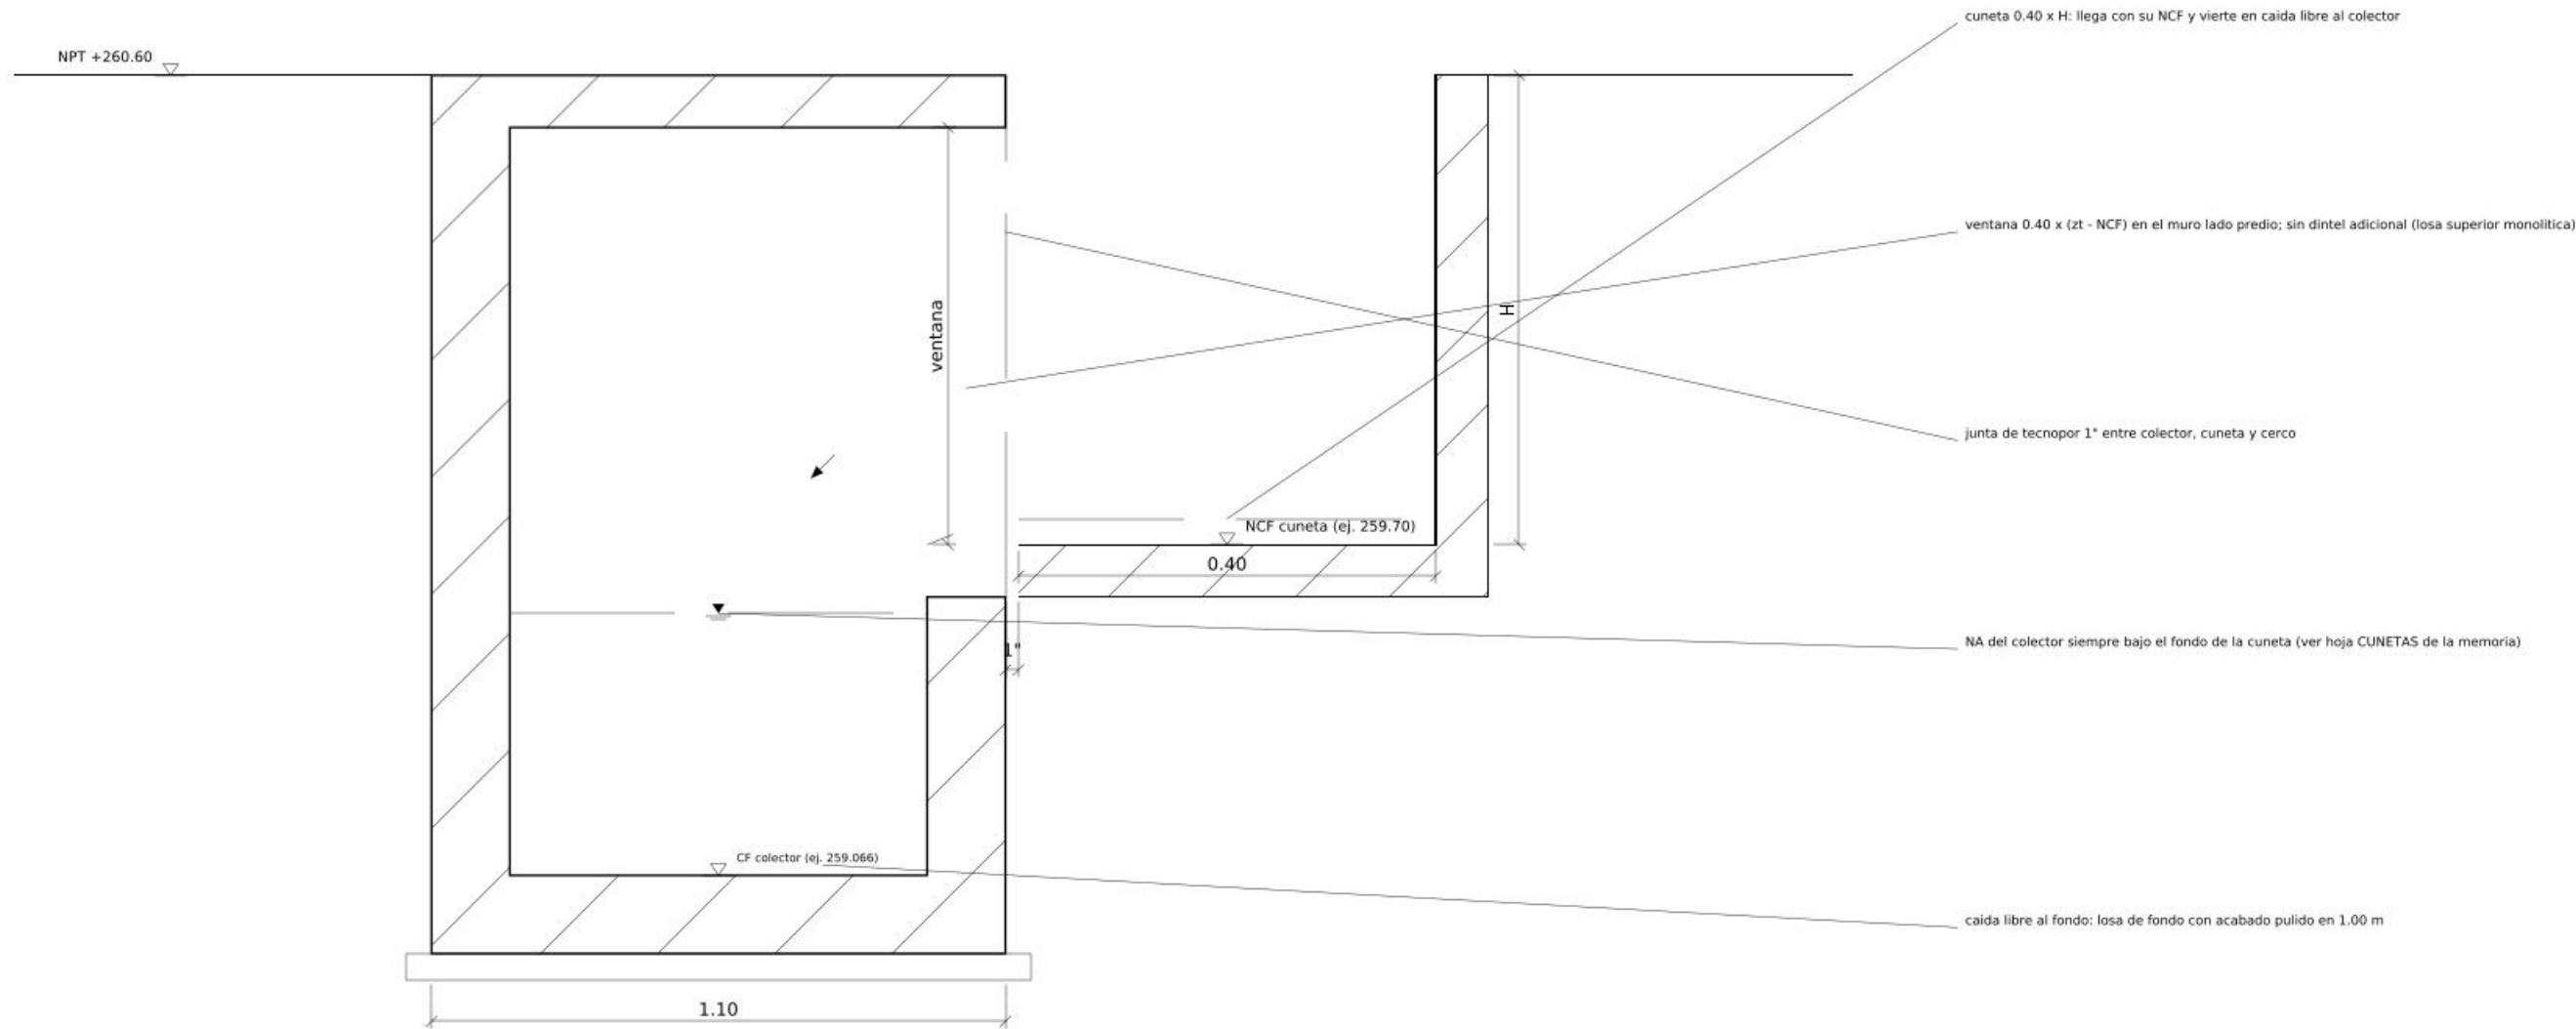

E2. EMPALME DE CUNETA - CORTE TRANSVERSAL (MIRANDO AGUAS ABAJO)

ESC. 1/10 - ejemplo cuneta Eje 02 (0+011.27); en las demas varía H y la cota de fondo

CUADRO DE EMPALMES

CUNETA	PROG.	NCF LLEGA	H VENTANA	REGISTRO
Eje 01	0+001.07	260.12	0.38	CL
Eje 02	0+011.27	259.70	0.80	RS-01
Eje 06	0+032.50	259.75	0.75	RS-03
Eje 07	0+042.68	259.72	0.78	RS-04
Eje 11	0+060.89	259.99	0.51	RS-06*
Eje 12	0+068.56	259.77	0.73	CC

* cuneta Eje 11: entra al tramo diagonal junto al registro RS-06; cuneta Eje 12: entra a la caja de caída CC.

PROYECTO:
CREACIÓN DEL SERVICIO DE ATENCIÓN INTEGRAL A MUJERES VÍCTIMAS DE VIOLENCIA EN EL HOGAR DE REFUGIO TEMPORAL
MUJERES VIOLENTADAS, DISTRITO DE MORALES, PROVINCIA Y DEPARTAMENTO DE SAN MARTÍN - CUI N. 2675514
ENTIDAD: GERENCIA TERRITORIAL BAJO MAYO - TARAPOTO

UBICACION: PREDIO RURAL LOS MANGOS - MORALES - SAN MARTÍN - SAN MARTÍN
ESPECIALIDAD: INSTALACIONES SANITARIAS - DRENAJE PLUVIAL


PLANO: DETALLE DEL EMPALME DE CUNETA AL COLECTOR
VENTANA EN EL MURO LADO PREDIO, CAIDA AL FONDO, JUNTAS Y REGISTRO - CUNETAS EJES 01, 02, 06, 07, 11 Y 12 - ESC. 1/10

PROYECTISTA: _____ CIP: _____

ELABORADO: HIDROCONSULT ESCALA: 1/10

REVISADO: _____ FECHA: OCT. 2026 LAMINA:

FIRMA Y SELLO: _____ REVISION: 00

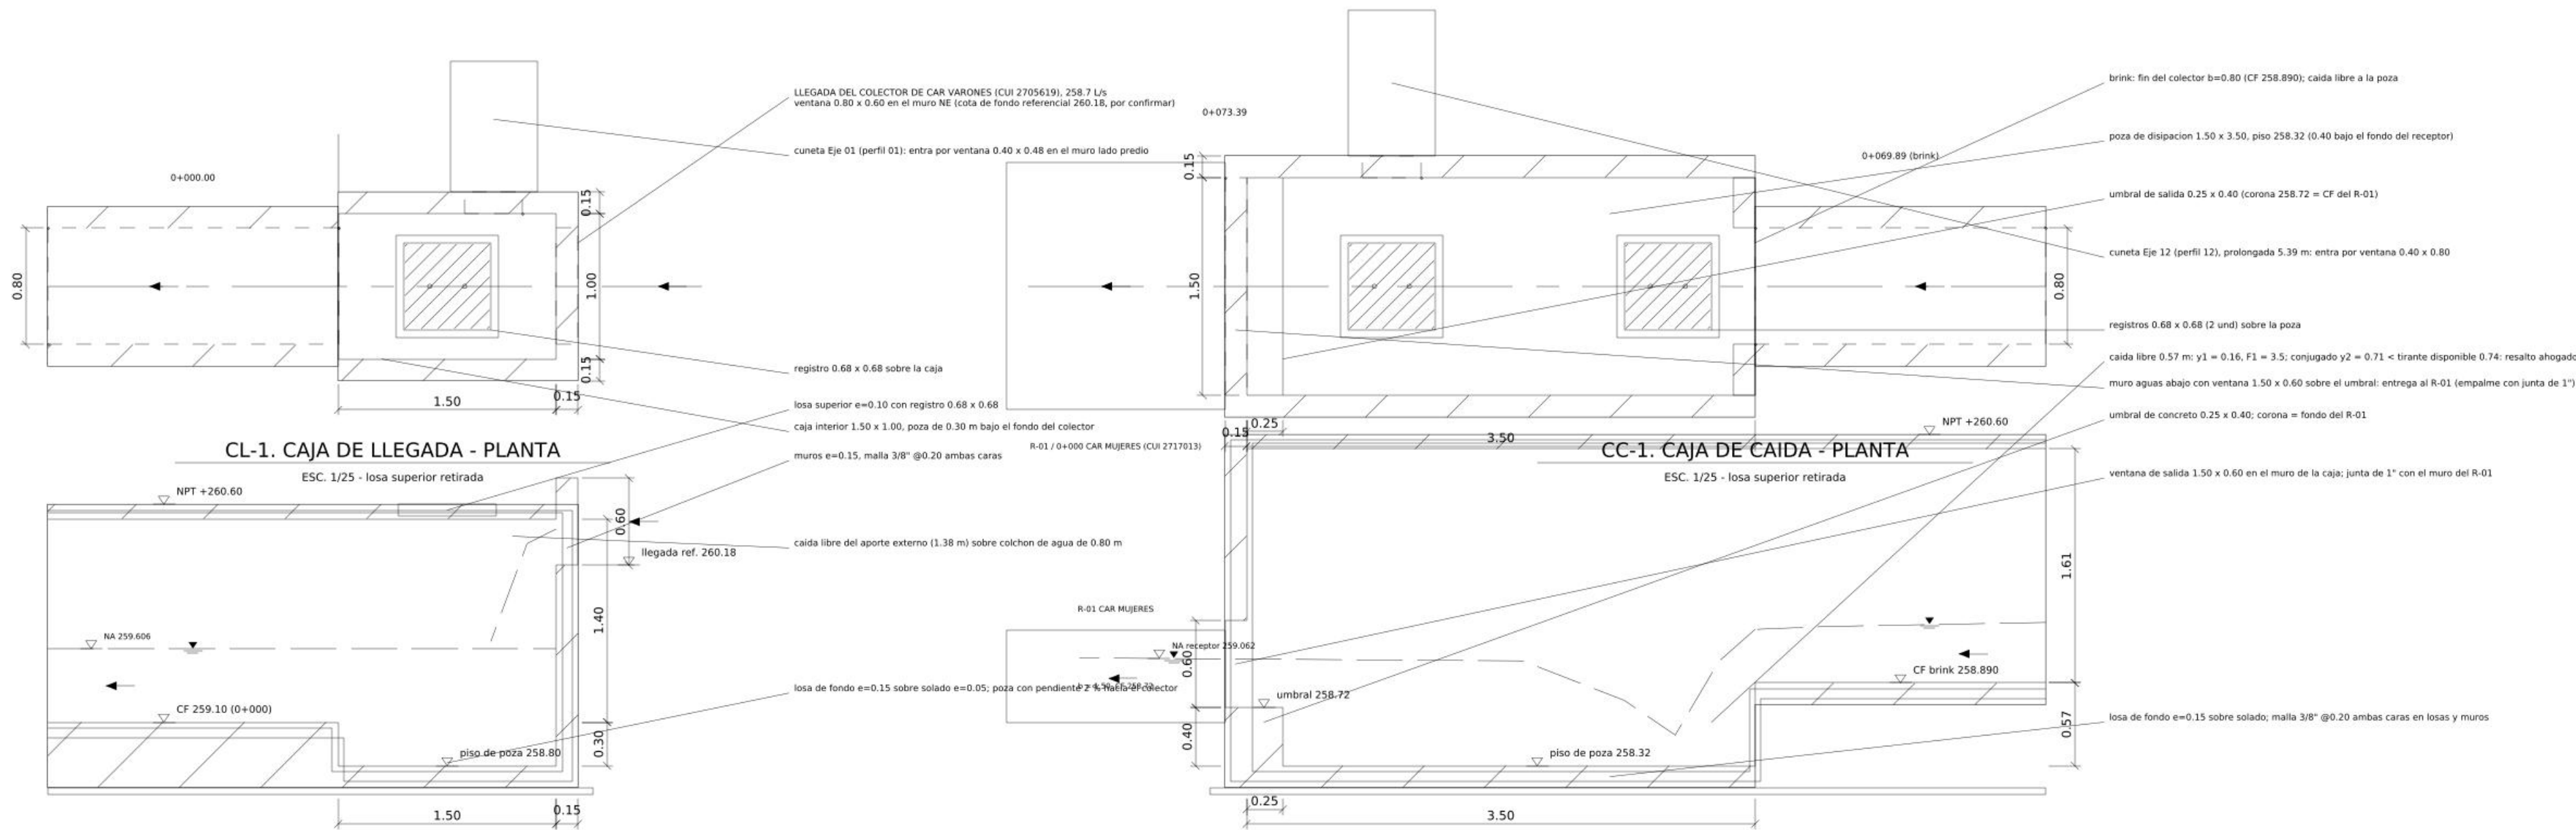

CL-2. CAJA DE LLEGADA - CORTE LONGITUDINAL POR EL EJE
ESC. 1/25

CC-2. CAJA DE CAIDA - CORTE LONGITUDINAL POR EL EJE
ESC. 1/25

CUADRO DE MATERIALES DE LAS CAJAS

CAJA	PARTIDA	CANTIDAD	UND.
Caja de llegada CL	concreto f'c=210 (losas + muros)	1.80	m3
	encofrado	18.50	m2
	acero 3/8" @0.20	82.6	kg
Caja de caída CC	excavacion / solado	7.05 / 2.66	m3 / m2
	concreto f'c=210 (losas + muros)	4.38	m3
	encofrado	50.05	m2
	acero 3/8" @0.20	206.8	kg
	excavacion / solado	15.04 / 7.13	m3 / m2

LEYENDA

- concreto armado f'c=210 kg/cm2
- solado f'c=100 e=0.05
- acero de refuerzo
- nivel de agua / chorro
- poza de disipacion y umbral
- receptor (CAR Mujeres), referencia
- cuneta que llega

NOTAS

- Ambas cajas quedan dentro del predio, cubiertas con losa e=0.10 y registros de 0.68 x 0.68.
- La caja de llegada recibe el colector de CAR Varones (CUI 2705619) como aporte externo; su cota y ancho de llegada (ventana 0.80 x 0.60) son referenciales y se ajustaran a su proyecto.
- La caja de caída entrega al R-01 del colector del CAR Mujeres (CUI 2717013) con fondo del umbral 258.72; el resalto queda ahogado por el tirante del receptor (memoria, hoja EMPALME).
- Secciones transversales de las cajas: muros e=0.15, losa de fondo e=0.15, malla 3/8" @0.20 en ambas caras; esquinas con ganchos de 0.40 m.
- Junta de tecnopor 1" + sello entre la caja CC y el muro del R-01, y entre la caja CL y el colector de llegada.

PROYECTO: CREACION DEL SERVICIO DE ATENCION INTEGRAL A MUJERES VICTIMAS DE VIOLENCIA EN EL HOGAR DE REFUGIO TEMPORAL MUJERES VIOLENTADAS, DISTRITO DE MORALES, PROVINCIA Y DEPARTAMENTO DE SAN MARTIN - CUI N. 2675514 ENTIDAD: GERENCIA TERRITORIAL BAJO MAYO - TARAPOTO		
UBICACION: PREDIO RURAL LOS MANGOS - MORALES - SAN MARTIN - SAN MARTIN ESPECIALIDAD: INSTALACIONES SANITARIAS - DRENAJE PLUVIAL		
PLANO: CAJA DE LLEGADA (0+000) Y CAJA DE CAIDA CON POZA DE DISIPACION (ENTREGA AL CAR MUJERES) PLANTAS, CORTES, ARMADO Y CUADRO DE MATERIALES - ESC. 1/25		
PROYECTISTA: _____ CIP: _____		
ELABORADO: HIDROCONSULT	ESCALA: 1/25	
REVISADO: _____	FECHA: OCT. 2026	LAMINA:
FIRMA Y SELLO:	REVISION: 00	DP-07

CUADRO DE DOBLADO DE ACERO

ELEMENTO	FORMA	DIAMETRO	ESPACIAM.	LONGITUD (m)	LONG. TOTAL (m)	PESO (kg)
Colector: marcos tramo normal	marco cerrado doble (ext. + int.)	3/8"	0.20	ver figura, h + 0.70	3628.8	2032.1
Colector: marcos cruce de motos	marco cerrado doble (ext. + int.)	3/8"	0.15	ver figura	161.6	90.5
Colector: marcos cruce de camiones (2 capas)	marco cerrado doble (ext. + int.)	1/2"	0.15	ver figura	755.1	750.5
Colector: barras longitudinales	recta con traslape 0.40	3/8"	0.25 / 0.20	continua	3410.7	1910.0
Cajas CL y CC: muros y losas	mallá 3/8" @0.20 ambas caras	3/8"	0.20	ver DP-07	516.6	289.3
Registros: refuerzo de borde de abertura	recta	1/2"	2 por lado	1.40	112.0	111.3
Tapas de registro (incluye asas)	recta / U	3/8"	0.10	0.62 / 0.40	94.8	53.1
Anciajes de contramarco		3/8"	8 por registro	0.20	16.0	9.0
Prolongacion de cunetas Ejes 11 y 12	U + rectas	3/8"	0.20	ver DP-06C	175.2	98.1
TOTAL						5343.9



Resumen: acero 3/8" = 4482.1 kg ; acero 1/2" = 861.9 kg ; total = 5343.9 kg (incluye traslapes y ganchos). Angulos metalicos: 151.4 kg.

ESPECIFICACIONES TECNICAS

CONCRETO ARMADO: f'c = 210 kg/cm2 (colector, cajas, tapas, prolongacion de cunetas). Cemento tipo I; agregados limpios; slump 3" a 4".
CONCRETO SIMPLE: solado f'c = 100 kg/cm2, e = 0.05 m; umbral de la poza f'c = 210 kg/cm2 vaciado con la losa de fondo.
ACERO DE REFUERZO: fy = 4200 kg/cm2 (grado 60), corrugado. Ganchos de 0.30 m en marcos y 0.40 m en esquinas de cajas.
RECUBRIMIENTOS: 0.04 m en muros y losa de fondo; 0.025 m en losa superior del tramo normal; 0.04 m en el cruce de camiones; 0.025 m en tapas.
TRASLAPES: 3/8" = 0.40 m ; 1/2" = 0.50 m, alternados. Barras longitudinales de 9.00 m.
LOSA SUPERIOR: vaciada monoliticamente con los muros en todo el colector; acabado frotachado y brunado (a nivel del piso terminado +260.60).
REGISTROS: marco y contramarco de angulo 2"x2"x3/16" y 1 1/2"x1 1/2"x1/8" con anclajes, pintura anticorrosiva y esmalte; tapas de concreto 0.68 x 0.68 x 0.08 con asas.
JUNTAS: cada 4.00 m, e = 1", relleno de poliestireno expandido y sello elastomerico de poliuretano. Tecnopor de 1" entre el colector y el cerco, las cunetas y el piso adyacente.
CAJAS: muros e = 0.15 y losa de fondo e = 0.15 con mallá 3/8" @0.20 en ambas caras; umbral 0.25 x 0.40 en la caja de calda.
CURADO: humedo mínimo 7 dias; no transitar sobre la losa antes de 14 dias; no cargar con camiones antes de 28 dias.
RELLENO: material propio seleccionado, capas de 0.15 m, 95 % del Proctor modificado; incluye la nivelacion del retro hasta la cota de la losa.
EXCAVACION: zanja de 1.60 m de ancho (0.25 m a cada lado del muro); entibar si la profundidad supera 1.50 m o el suelo lo requiere.
VERIFICAR la cota de llegada del colector de CAR Varones (CUI 2705619) antes de vaciar la caja de llegada; verificar en campo la ubicacion del R-01 del CAR Mujeres (CUI 2717013).

GROSOR DE PLUMILLA POR COLOR (CTB)

color 4 concreto 0.40 mm
color 5 muros en planta / marcos metalicos 0.35 mm
color 1 acero de refuerzo 0.30 mm
color 6 registros, cortes, lindero, cerco 0.30 mm
color 3 terreno y cunetas 0.25 mm
color 7 textos y marcos de lamina 0.20 mm
color 30 tapas, cruces vehiculares, relleno 0.18 mm
color 34 poza y umbral 0.18 mm
color 2 cotas y progresivas 0.15 mm
color 140 agua y flujo 0.13 mm
color 8 achurados, auxiliares y arq. base 0.09 mm
color 9 grillas 0.05 mm
color 252-255 caras de isometricos (solidos) 0.05 mm

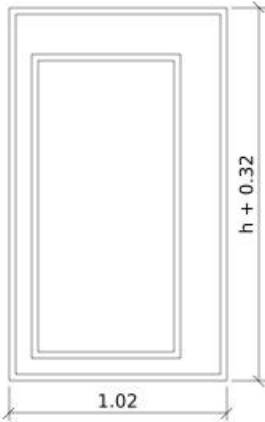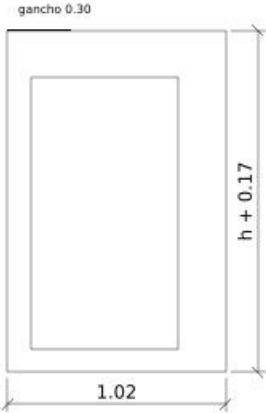

MARCOS CERRADOS 3/8" (tramo normal @0.20, motos @0.15)

marco exterior 1.02 x (h+0.17) y marco interior 0.80+0.22 x (h+0.22); ganchos de 0.30 m


MARCOS DOBLES 1/2" @0.15 (cruce de camiones)

dos capas en muros y losas; losa superior e=0.25

NOTAS GENERALES


- Dimensiones en metros y cotas en m.s.n.m., salvo indicacion.
- El colector esta dimensionado para 560.6 L/s (CAR Varones 258.7 + Hogar de Refugio 301.9; TR 25 años).
- Verificaciones hidraulica y estructural segun memoria de calculo del proyecto (RNE CE.040, E.020, E.060; AASHTO LRFD HL-93).
- Las cunetas de arquitectura (perfiles 01 a 12) y sus cotas de fondo son datos del plano PLANTA GENERAL REFUGIO (03-10-2026).
- Confirmar la capacidad portante con el estudio de mecanica de suelos antes del vaciado (presion de contacto 0.33 kg/cm2).

PROYECTO: CREACION DEL SERVICIO DE ATENCION INTEGRAL A MUJERES VICTIMAS DE VIOLENCIA EN EL HOGAR DE REFUGIO TEMPORAL MUJERES VIOLENTADAS, DISTRITO DE MORALES, PROVINCIA Y DEPARTAMENTO DE SAN MARTIN - CUI N. 2675514 ENTIDAD: GERENCIA TERRITORIAL BAJO MAYO - TARAPOTO		
UBICACION: PREDIO RURAL LOS MANGOS - MORALES - SAN MARTIN - SAN MARTIN ESPECIALIDAD: INSTALACIONES SANITARIAS - DRENAJE PLUVIAL		
PLANO: CUADROS DE ACERO, ESPECIFICACIONES TECNICAS Y NOTAS CUADRO DE DOBLADO Y RESUMEN DE ACERO, ESPECIFICACIONES DE MATERIALES Y GROSORES DE IMPRESION		
PROYECTISTA: _____ CIP: _____		
ELABORADO: HIDROCONSULT	ESCALA: 1/25	
REVISADO: _____	FECHA: OCT. 2026	LAMINA:
FIRMA Y SELLO:	REVISION: 00	DP-08

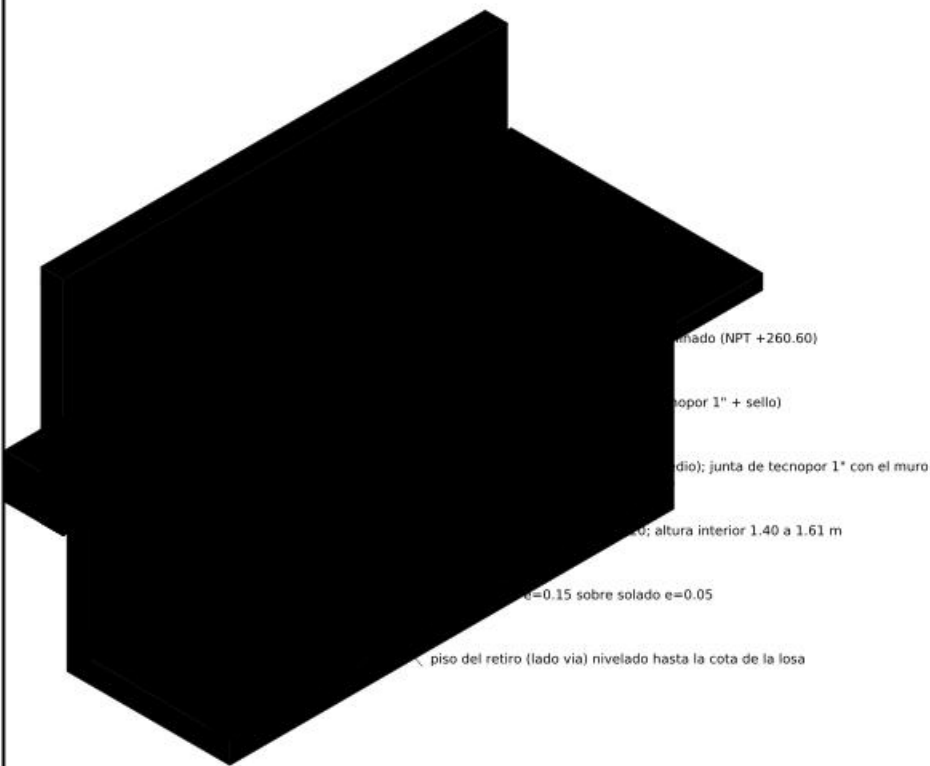

ISOMETRICO 1: COLECTOR JUNTO AL CERCO

tramo típico de 3.00 m - sin escala

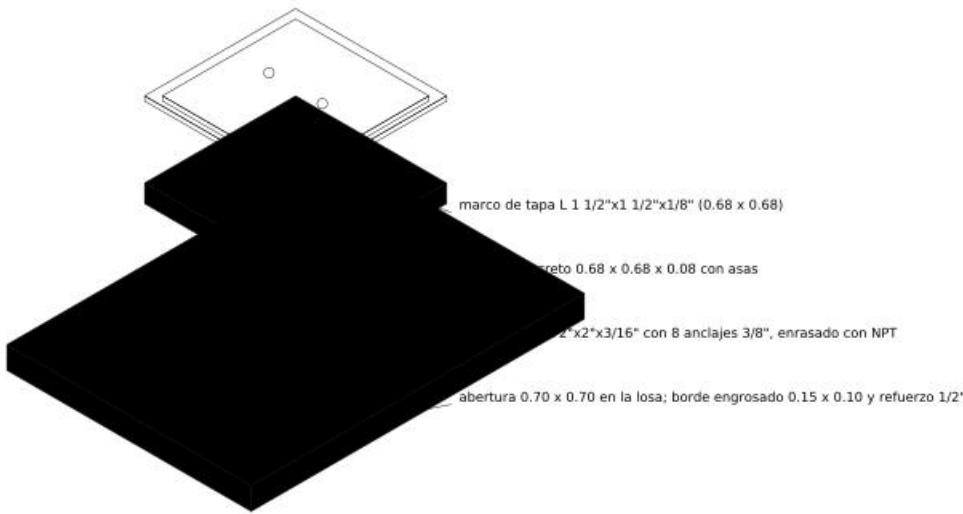


ISOMETRICO 2: REGISTRO DE LIMPIEZA

vista explotada: contramarco, tapa y marco - sin escala


LEYENDA

- concreto armado
- tapa de registro
- agua
- cuneta que llega
- cerco perimétrico existente
- piso / relleno del retiro
- umbral de la poza
- marco y contramarco metálico

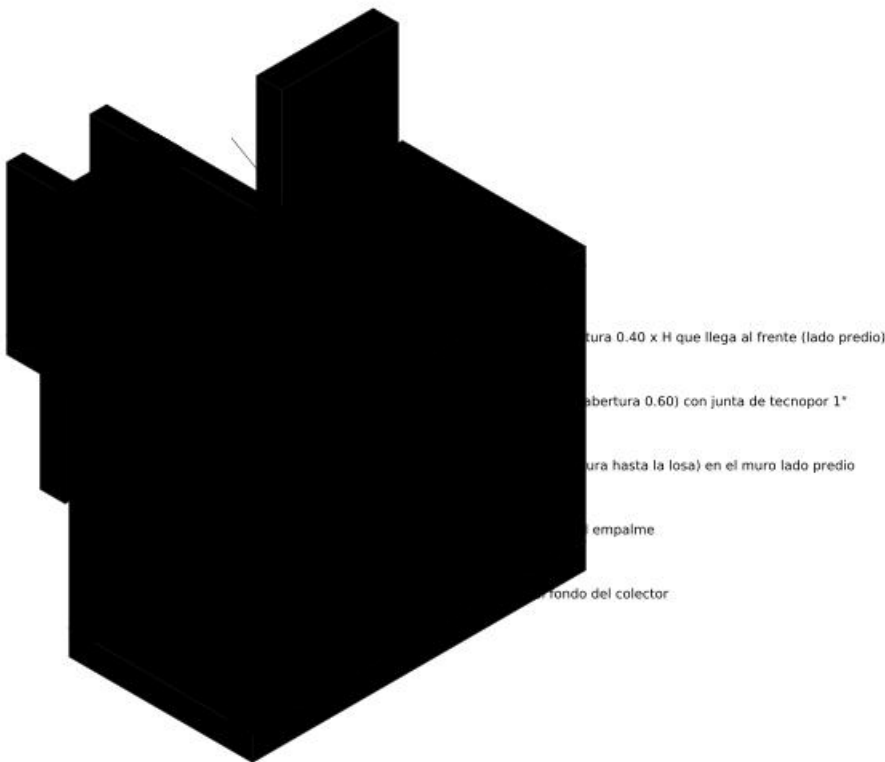

ISOMETRICO 3: EMPALME DE CUNETA

cunetas Ejes 01, 02, 06, 07, 11 y 12 - losa superior cortada - sin escala

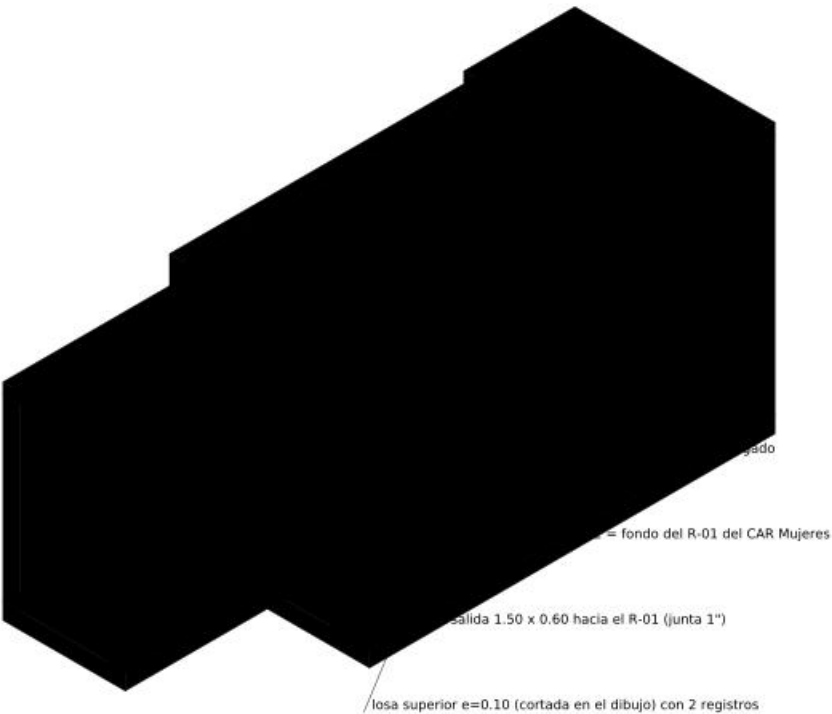

ISOMETRICO 4: CAJA DE CAIDA CON POZA


entrega al R-01 del CAR Mujeres - losa superior cortada - sin escala

PROYECTO: CREACION DEL SERVICIO DE ATENCION INTEGRAL A MUJERES VICTIMAS DE VIOLENCIA EN EL HOGAR DE REFUGIO TEMPORAL MUJERES VIOLENTADAS, DISTRITO DE MORALES, PROVINCIA Y DEPARTAMENTO DE SAN MARTIN - CUI N. 2675514 ENTIDAD: GERENCIA TERRITORIAL BAJO MAYO - TARAPOTO		
UBICACION: PREDIO RURAL LOS MANGOS - MORALES - SAN MARTIN - SAN MARTIN ESPECIALIDAD: INSTALACIONES SANITARIAS - DRENAJE PLUVIAL		
PLANO: ISOMETRICOS CONSTRUCTIVOS COLECTOR JUNTO AL CERCO, REGISTRO DE LIMPIEZA, EMPALME DE CUNETA Y CAJA DE CAIDA		
PROYECTISTA: _____ CIP: _____		
ELABORADO: HIDROCONSULT	ESCALA: 1/25	
REVISADO: _____	FECHA: OCT. 2026	LAMINA:
FIRMA Y SELLO:	REVISION: 00	DP-09


LEYENDA

- colector y cajas de concreto armado (losa superior)
- tapa de registro
- cuneta que llega
- colector receptor (CAR Mujeres), referencia

Vista isométrica de conjunto con el eje desarrollado (los quiebres a 45 grados se indican en su progresiva); escala vertical ampliada x3 para mayor claridad del relieve. Medidas reales en las laminas DP-01 a DP-09.

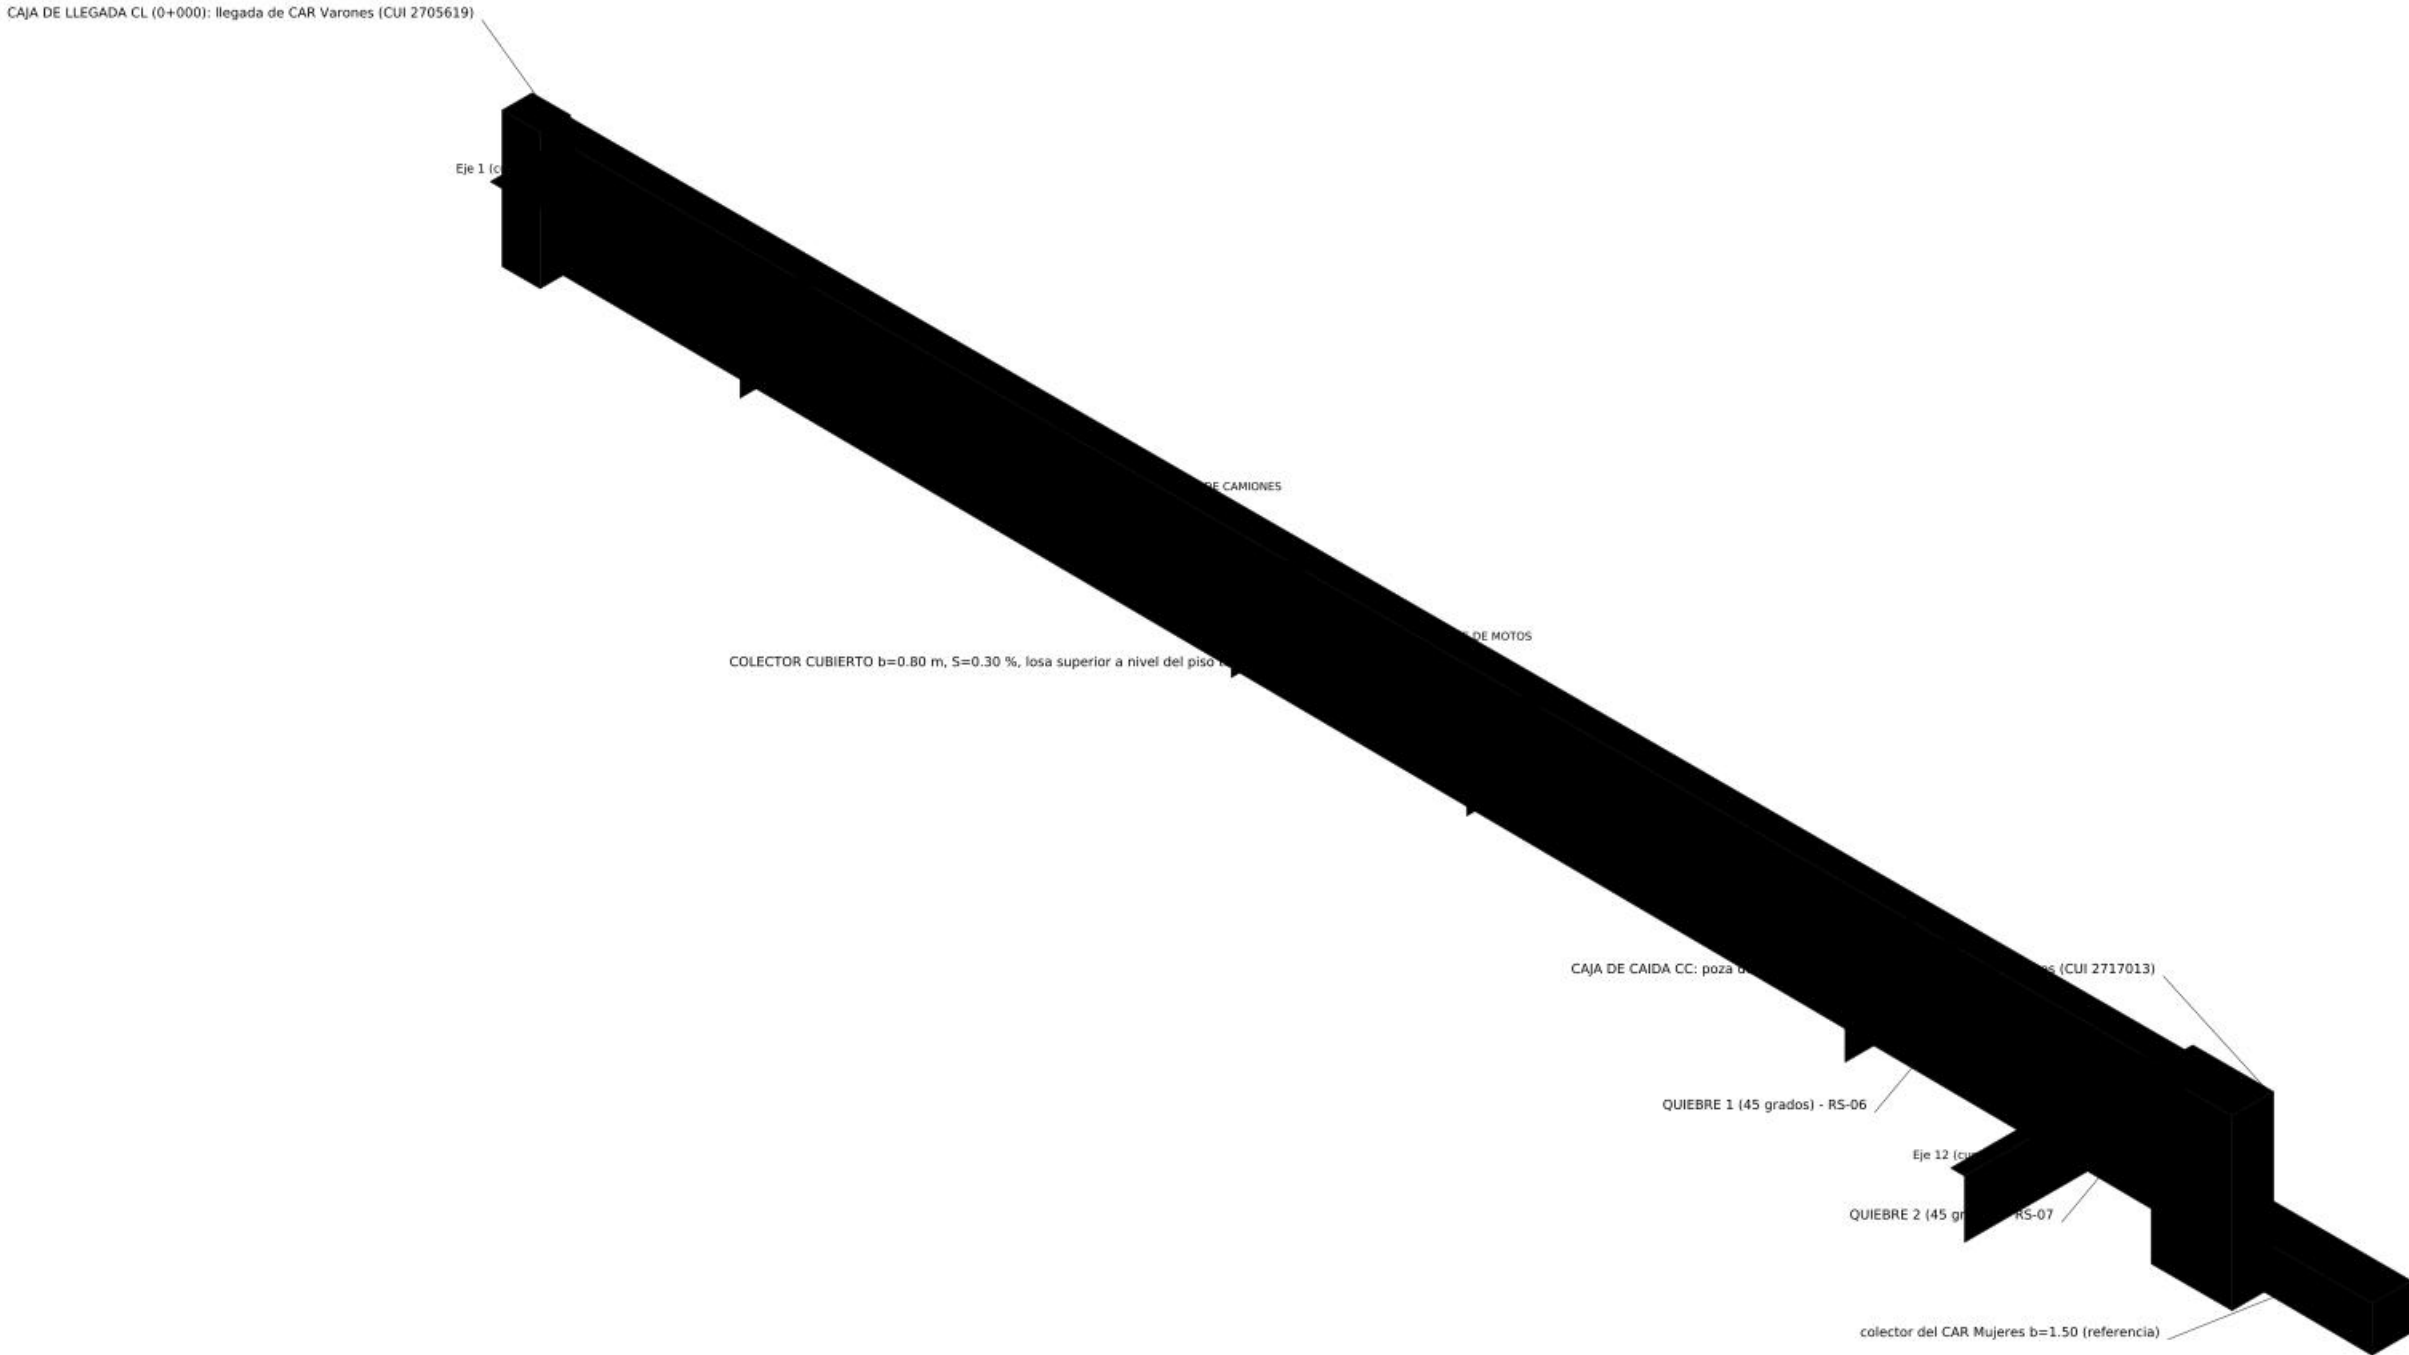


PROYECTO: CREACION DEL SERVICIO DE ATENCION INTEGRAL A MUJERES VICTIMAS DE VIOLENCIA EN EL HOGAR DE REFUGIO TEMPORAL MUJERES VIOLENTADAS, DISTRITO DE MORALES, PROVINCIA Y DEPARTAMENTO DE SAN MARTIN - CUI N. 2675514 ENTIDAD: GERENCIA TERRITORIAL BAJO MAYO - TARAPOTO		
UBICACION: PREDIO RURAL LOS MANGOS - MORALES - SAN MARTIN - SAN MARTIN ESPECIALIDAD: INSTALACIONES SANITARIAS - DRENAJE PLUVIAL		
PLANO: ISOMETRICO GENERAL DEL COLECTOR PLUVIAL VISTA DE CONJUNTO: CAJA DE LLEGADA, COLECTOR CUBIERTO, REGISTROS, EMPALMES DE CUNETAS, QUIEBRES Y CAJA DE CAIDA		
PROYECTISTA: _____ CIP: _____		
ELABORADO: HIDROCONSULT	ESCALA: 1/200	
REVISADO: _____	FECHA: OCT. 2026	LAMINA:
FIRMA Y SELLO:	REVISION: 00	DP-10

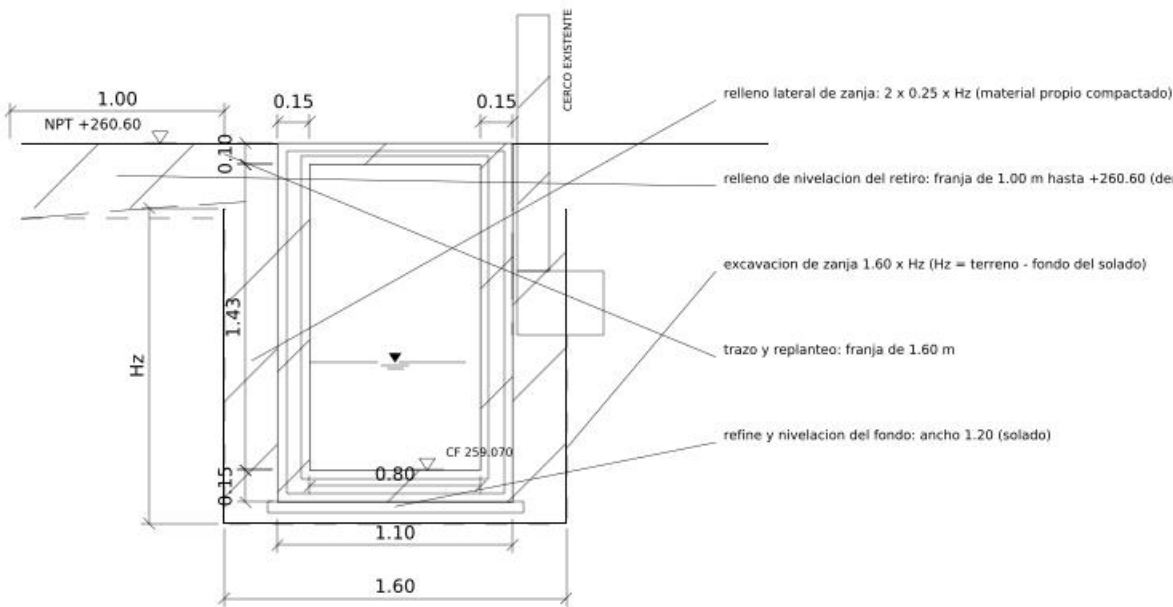


ZANJA TIPICA - TRAMO NORMAL

PROG. 0+010.00 - ESC. 1/25

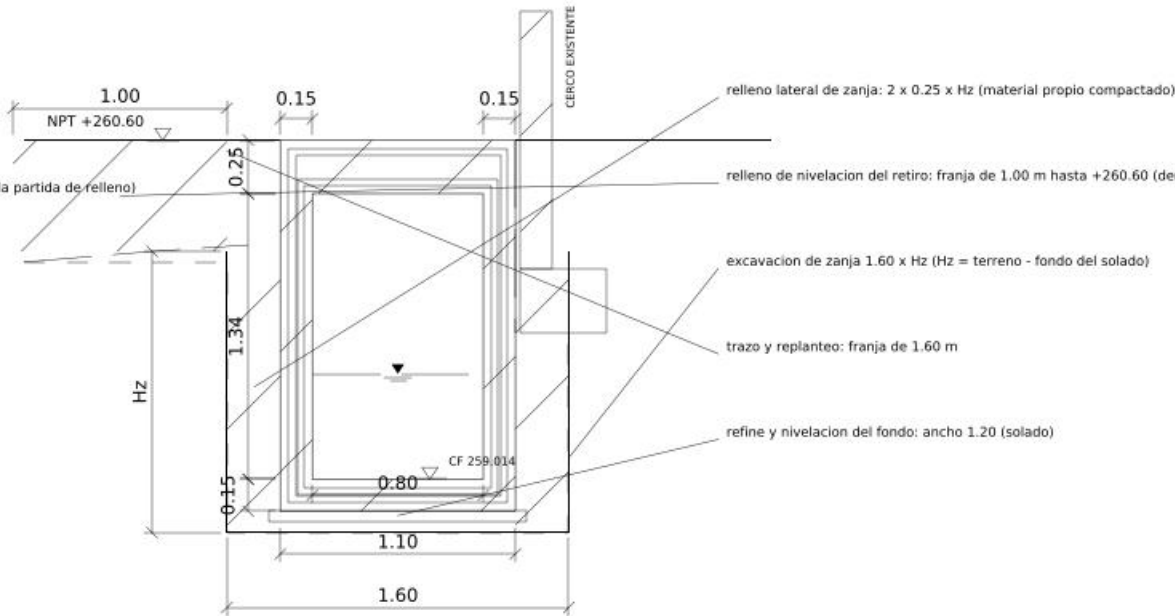

ZANJA - CRUCE DE CAMIONES

PROG. 0+028.80 - ESC. 1/25

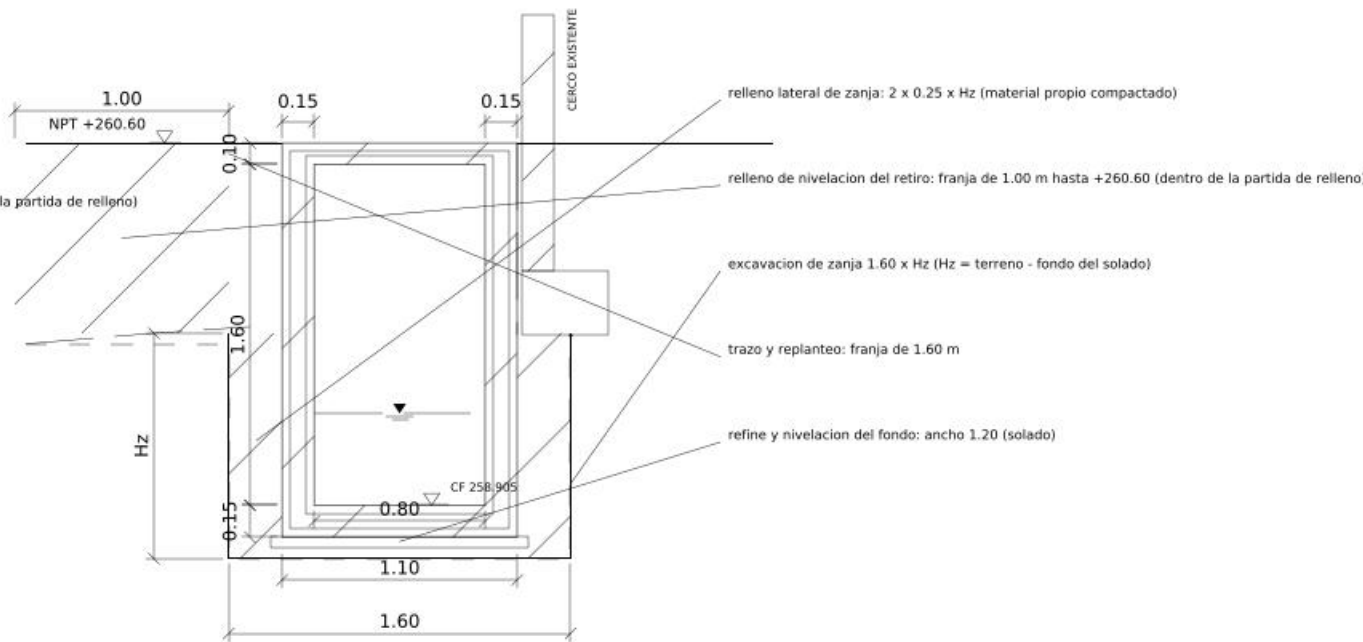

ZANJA - TRAMO DIAGONAL

PROG. 0+065.00 - ESC. 1/25


RESUMEN DE MOVIMIENTO DE TIERRAS

PARTIDA	UND	METRADO	CRITERIO
Trazo, niveles y replanteo	m2	126.69	franja de 1.60 m x L + cajas + prolongaciones de cuneta
Excavacion de zanja	m3	170.86	1.60 x Hz x L por tramo (Hz desde el terreno existente), cajas y cunetas
Refine y nivelacion de fondo	m2	93.65	1.20 x L + cajas
Relleno compactado con material propio	m3	84.28	relleno lateral de zanja + franja de nivelacion del retiro (1.00 m) + cajas
Eliminacion de material excedente	m3	103.90	(excavacion - relleno) x 1.25

NOTAS


- Hz varia con el terreno existente (superficie topografica) y la cota de fondo del colector; ver tabla de tramos en la planilla de metrados.
- Criterio: los rellenos menores (nivelacion de la franja adyacente, base de las cajas) van dentro de la partida de relleno, no como partida aparte.
- Donde el terreno existente queda por debajo de la losa, el muro lado via se vacia con encofrado exterior y luego se rellena.

PROYECTO: CREACION DEL SERVICIO DE ATENCION INTEGRAL A MUJERES VICTIMAS DE VIOLENCIA EN EL HOGAR DE REFUGIO TEMPORAL MUJERES VIOLENTADAS, DISTRITO DE MORALES, PROVINCIA Y DEPARTAMENTO DE SAN MARTIN - CUI N. 2675514 ENTIDAD: GERENCIA TERRITORIAL BAJO MAYO - TARAPOTO		
UBICACION: PREDIO RURAL LOS MANGOS - MORALES - SAN MARTIN - SAN MARTIN ESPECIALIDAD: INSTALACIONES SANITARIAS - DRENAJE PLUVIAL		
PLANO: DETALLE DE PARTIDAS: TRAZO, EXCAVACION, RELLENO Y ELIMINACION SECCION TIPICA DE ZANJA POR ZONA Y RESUMEN DE METRADO - ESC. 1/25		
PROYECTISTA: _____ CIP: _____		
ELABORADO: HIDROCONSULT	ESCALA: 1/25	
REVISADO: _____	FECHA: OCT. 2026	LAMINA:
FIRMA Y SELLO:	REVISION: 00	

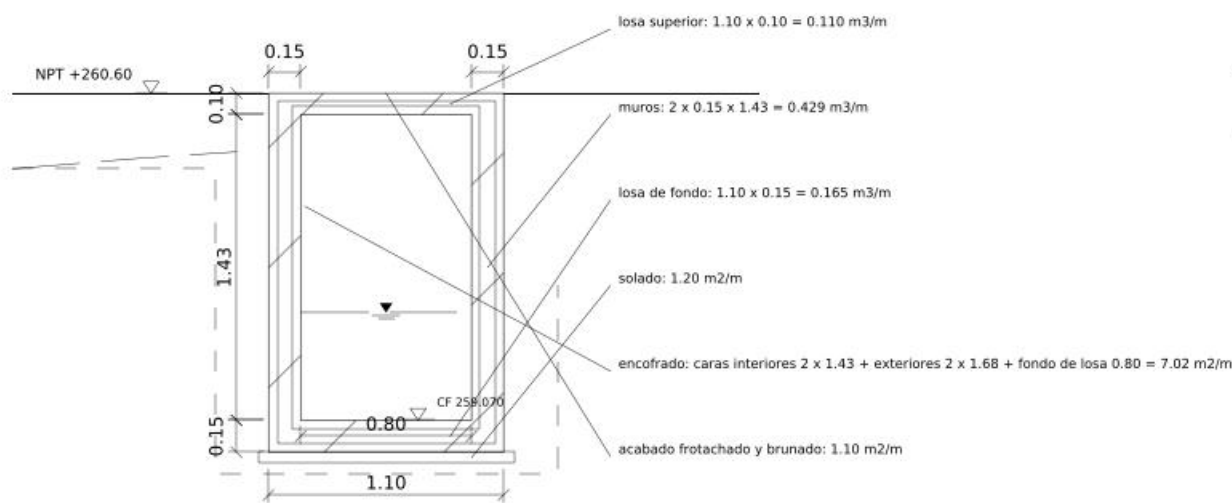


TRAMO NORMAL

PROG. 0+010.00 - h = 1.43 m - ESC. 1/25

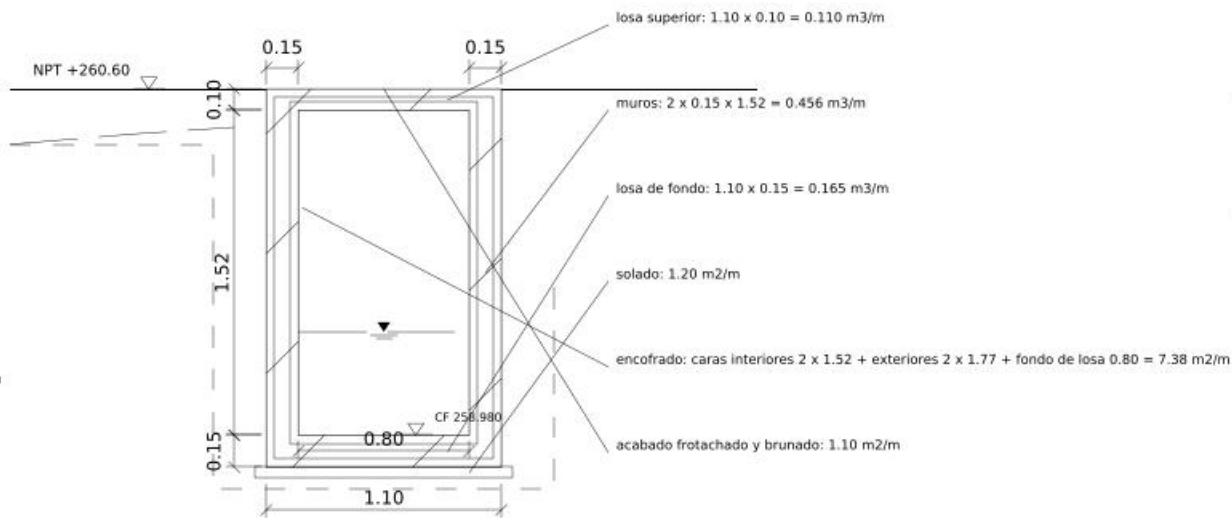

CRUCE DE MOTOS

PROG. 0+040.00 - h = 1.52 m - ESC. 1/25

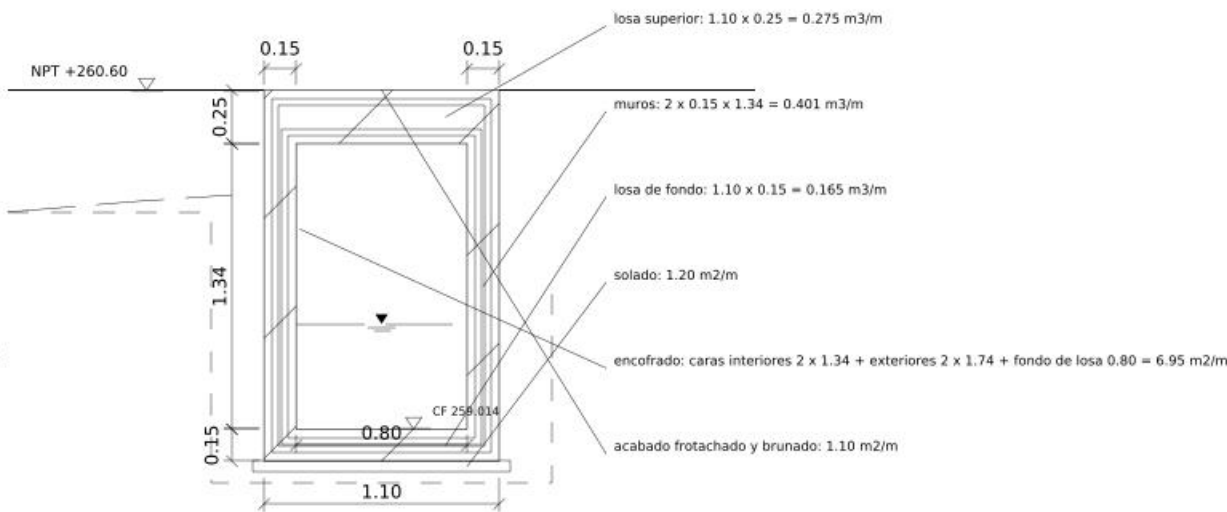


CRUCE DE CAMIONES

PROG. 0+028.80 - h = 1.34 m - ESC. 1/25

RESUMEN DE CONCRETO Y ENCOFRADO (colector + cajas)


PARTIDA	UND	METRADO
Solado f'c=100 e=0.05	m2	98.74
Concreto f'c=210 - losa de fondo	m3	13.02
Concreto f'c=210 - muros	m3	35.27
Concreto f'c=210 - losa superior (incluye bordes de registro)	m3	9.22
Encofrado y desencofrado	m2	578.57
Acabado frotachado y brunado de losa superior	m2	85.79
Prolongacion de cumetas: concreto / encofrado	m3 / m2	1.52 / 23.21

PROYECTO: CREACION DEL SERVICIO DE ATENCION INTEGRAL A MUJERES VICTIMAS DE VIOLENCIA EN EL HOGAR DE REFUGIO TEMPORAL MUJERES VIOLENTADAS, DISTRITO DE MORALES, PROVINCIA Y DEPARTAMENTO DE SAN MARTIN - CUI N. 2675514 ENTIDAD: GERENCIA TERRITORIAL BAJO MAYO - TARAPOTO		
UBICACION: PREDIO RURAL LOS MANGOS - MORALES - SAN MARTIN - SAN MARTIN ESPECIALIDAD: INSTALACIONES SANITARIAS - DRENAJE PLUVIAL		
PLANO: DETALLE DE PARTIDAS: SOLADO, CONCRETO ARMADO Y ENCOFRADO AREAS Y VOLUMENES POR METRO LINEAL EN CADA ZONA - ESC. 1/25		
PROYECTISTA: _____ CIP: _____		
ELABORADO: HIDROCONSULT	ESCALA: 1/25	
REVISADO: _____	FECHA: OCT. 2026	LAMINA:
FIRMA Y SELLO:	REVISION: 00	

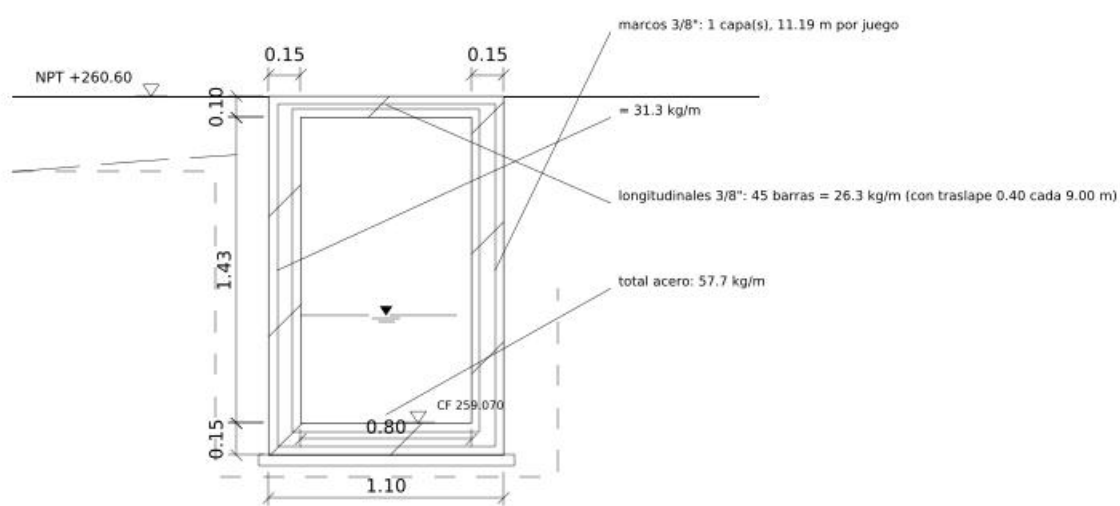


TRAMO NORMAL @0.20

PROG. 0+010.00 - ESC. 1/25

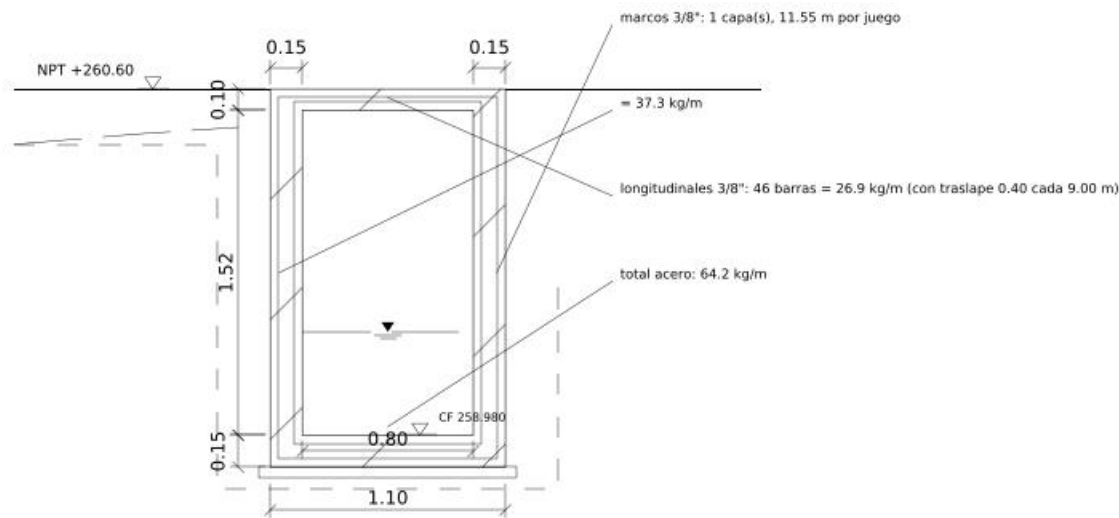

CRUCE DE MOTOS @0.15

PROG. 0+040.00 - ESC. 1/25

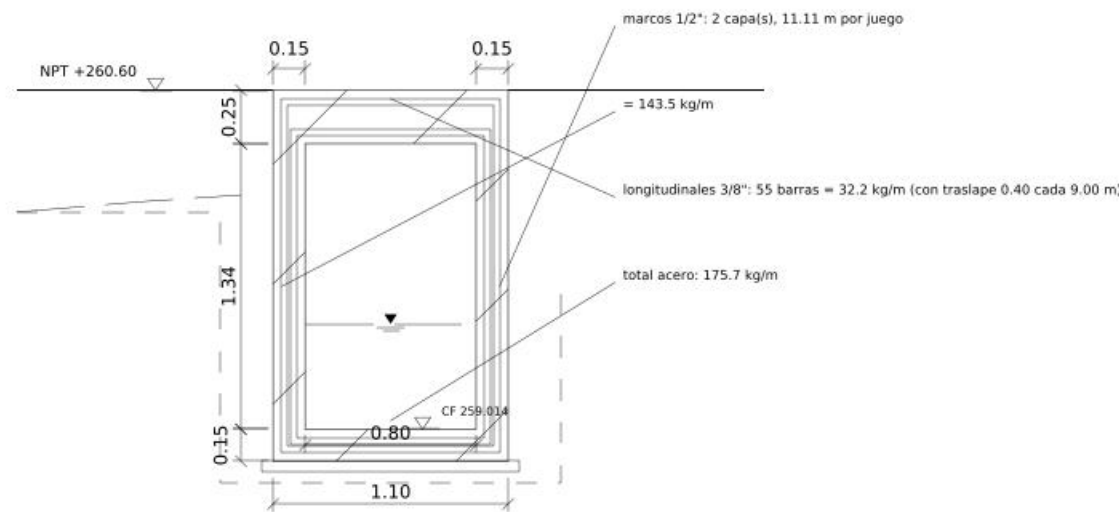

CRUCE DE CAMIONES 1/2" @0.15 DOBLE

PROG. 0+028.80 - ESC. 1/25

RESUMEN DE ACERO, REGISTROS, JUNTAS Y EMPALMES

PARTIDA	UND	METRADO
Acero fy=4200 colector y cajas - 3/8"	kg	4321.9
Acero fy=4200 colector - 1/2" (cruce de camiones)	kg	750.5
Acero en prolongacion de cunetas 3/8"	kg	98.1
Registros: contramarco L 2"x2"x3/16" (10 und)	kg	101.6
Registros: marco de tapa L 1 1/2"x1 1/2"x1/8"	kg	49.8
Tapas de concreto 0.68 x 0.68 x 0.08	und / m3	10 / 0.37
Acero en tapas, bordes, asas y anclajes	kg	173.4
Pintura anticorrosiva y esmalte en angulos	m2	9.82
Junta de dilatacion e=1" con sello (17 und x 5.90 m)	m	100.30
Junta de tecnopor e=1" con el cerco (muro)	m	58.81
Junta de tecnopor e=1" con el piso adyacente	m	150.97
Empalme de cuneta al colector (ventana + calida)	und	6

PROYECTO: CREACION DEL SERVICIO DE ATENCION INTEGRAL A MUJERES VICTIMAS DE VIOLENCIA EN EL HOGAR DE REFUGIO TEMPORAL MUJERES VIOLENTADAS, DISTRITO DE MORALES, PROVINCIA Y DEPARTAMENTO DE SAN MARTIN - CUI N. 2675514 ENTIDAD: GERENCIA TERRITORIAL BAJO MAYO - TARAPOTO		
UBICACION: PREDIO RURAL LOS MANGOS - MORALES - SAN MARTIN - SAN MARTIN ESPECIALIDAD: INSTALACIONES SANITARIAS - DRENAJE PLUVIAL		
PLANO: DETALLE DE PARTIDAS: ACERO, REGISTROS, JUNTAS Y EMPALMES DESPIECE POR METRO, INSUMOS POR REGISTRO Y LONGITUDES DE JUNTA - ESC. 1/25		
PROYECTISTA: _____ CIP: _____		
ELABORADO: HIDROCONSULT	ESCALA: 1/25	
REVISADO: _____	FECHA: OCT. 2026	LAMINA:
FIRMA Y SELLO:	REVISION: 00	