


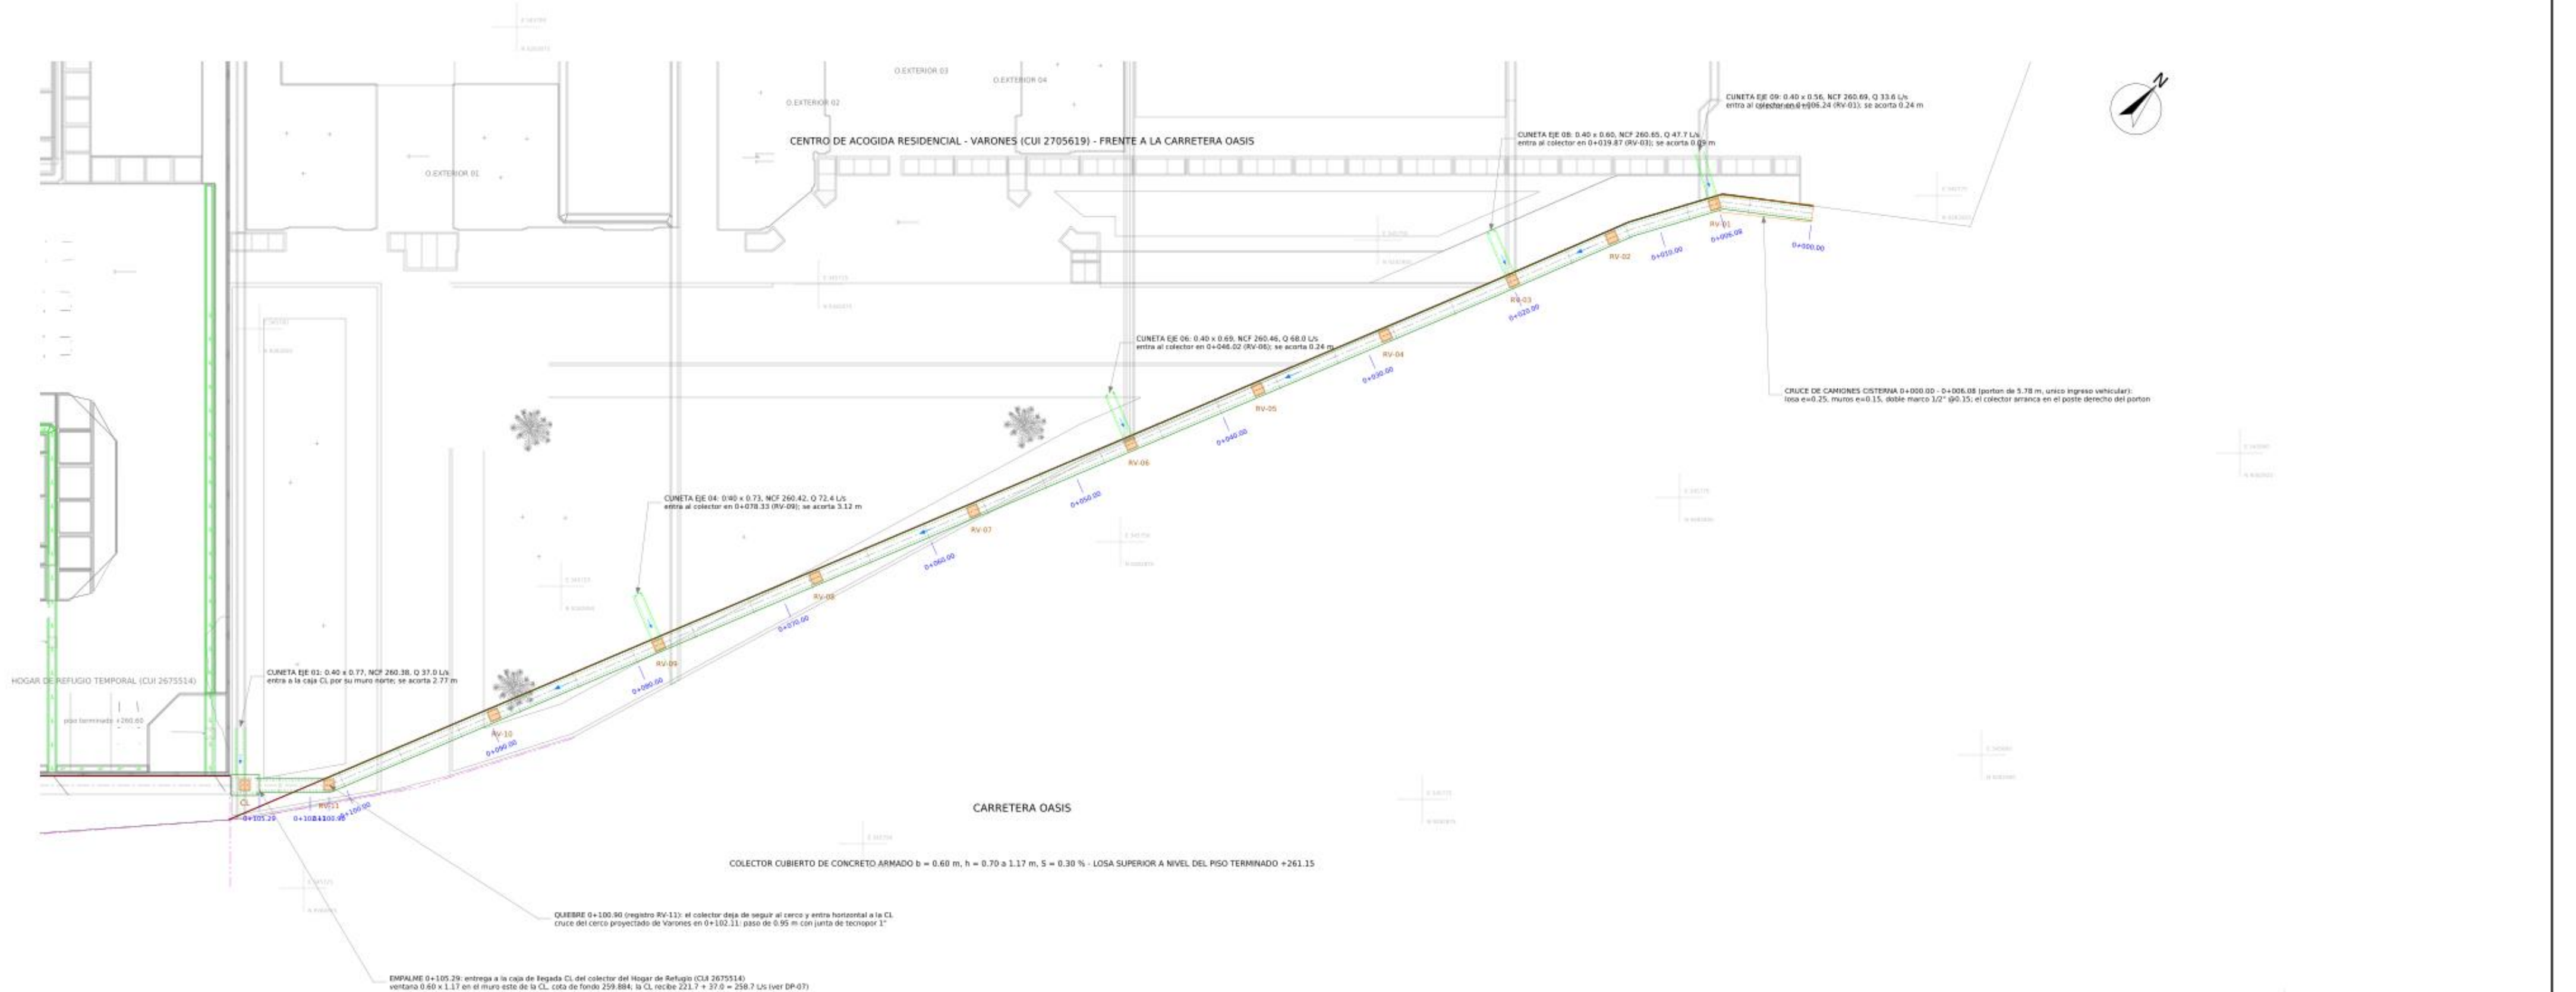

CUADRO DE COORDENADAS DE REGISTROS Y EMPALME

PUNTO	PROGRESIVA	ESTE	NORTE	COTA FONDO	COTA TAPA	OBSERVACION
D+000	0+000.00	345769.744	9282919.037	260.200	261.150	inicio: poste derecho del porton de camiones
RV-01	0+006.24	345764.674	9282915.475	260.382	261.150	empalme cuneta Eje 09
RV-02	0+013.05	345763.115	9282909.679	260.361	261.150	limpieza
RV-03	0+019.87	345758.131	9282903.546	260.340	261.150	empalme cuneta Eje 08
RV-04	0+028.59	345754.254	9282895.735	260.314	261.150	limpieza
RV-05	0+037.30	345750.371	9282887.939	260.088	261.150	limpieza
RV-06	0+046.02	345746.483	9282880.134	260.062	261.150	empalme cuneta Eje 06
RV-07	0+056.79	345742.680	9282870.494	260.030	261.150	limpieza
RV-08	0+067.56	345738.878	9282860.854	259.997	261.150	limpieza
RV-09	0+078.33	345733.076	9282851.234	259.965	261.150	empalme cuneta Eje 04
RV-10	0+089.61	345727.046	9282841.117	259.931	261.150	limpieza
RV-11	0+100.90	345722.012	9282831.012	259.897	261.150	quiebre: inicio del tramo de empalme con la CL
CL	0+105.29	345718.672	9282828.163	259.884	261.150	quiebre: inicio de la caja de llegada CL del colector del Hogar de Refugio (CUA 2675514); recibe tambien la cuneta Eje 01

Coordenadas UTM WGS84 - Zona 18 Sur; en el mismo sistema del tramo del Hogar de Refugio (ignorreferenciado con el R-02 del CAR Mujeres y el admet 46.34 del linderos). Verificar en campo.

LEYENDA


- muro exterior del colector
- cara interior (bajo losa superior)
- eje del colector
- registro de limpieza con tapa removible
- junta de dilatacion cada 4.00 m
- cruce de camiones cisterna (portón)
- cuneta de arquitectura (tramo que se construye)
- tramo de cuneta que se descuenta
- cercos perimetricos (proyectado / existente)
- linderos
- arquitectura (referencia)
- sentido del flujo

NOTAS

- Colector de concreto armado $f'c=210 \text{ kg/cm}^2$. Cubierto, losa superior monolitica con los muros y al ras del piso terminado +261.15.
- Via por fuera del cerco proyectado, dentro del predio: muro lado predio a 0.025 m del cerco (hacropor 1"); eje a 0.475 m del cerco.
- Progresivas desde el poste derecho del porton de camiones (0+000, junto al Eje 09) crecientes hacia la caja CL del Hogar de Refugio.
- Registros con tapa removible al ras, en cada empalme de cuneta, en el quiebre y cada 32.00 m como maximo (11 und).
- Cotas en m.s.n.m. Fondo 260.20 (0+000) a 259.884 (llegada a la CL), $S = 0.30 \text{ ‰}$; fondo de la CL 258.80 (cota 1.08 m).
- Las cunetas de los Ejes 09, 08, 06 y 04 entran por ventana en el muro lado predio; la del Eje 01 cae a la caja CL. El tramo de cada cuneta que cae dentro del colector se descuenta en la partida de cunetas (0.24, 0.09, 0.24, 3.32 y 2.77 m).
- La caja CL es parte del expediente del Hogar de Refugio (CUA 2675514); su tapa queda en +261.15 (piso del CAR Varones).
- Perfil en DP-02, secciones en DP-04, registro en DP-06B, empalme de cunetas en DP-06C, empalme con la CL en DP-07, acero y especificaciones en DP-08.

PROYECTO: CREACION DEL SERVICIO DE PROTECCION INTEGRAL A NIÑAS, NIÑOS Y ADOLESCENTES SIN CUIDADOS PARENTALES O EN RIESGO DE PERDERLOS EN CENTRO DE ACOGIDA RESIDENCIAL - VARONES, DISTRITO DE MORALES, PROVINCIA Y DEPARTAMENTO DE SAN MARTIN - CU N. 2705619 ENTIDAD: GERENCIA TERRITORIAL BAJO MAYO - TARAPOTO		
UBICACION: PREDIO ALDEA INFANTIL VIRGEN DEL PILAR - MORALES - SAN MARTIN - SAN MARTIN ESPECIALIDAD: INSTALACIONES SANITARIAS - DRENAJE PLUVIAL		
PLANO: PLANTA DEL COLECTOR PLUVIAL TRAMO CAR VARONES (0+000.00 - 0+105.29) - TRAZO, REGISTROS, LLEGADA DE CUNETAS Y EMPALME CON LA CAJA CL DEL HOGAR DE REFUGIO		
PROYECTISTA: _____ CIP: _____		
ELABORADO: HIDROCONSULT	ESCALA: 1/200	
REVISADO: _____	FECHA: OCT. 2026	LAMINA: _____
FIRMA Y SELLO: _____	REVISION: 00	DP-01


FRANJA 1: 0+000.00 A 0+036.00 - CORTE POR EL EJE (ESC. 1/50, H = V)

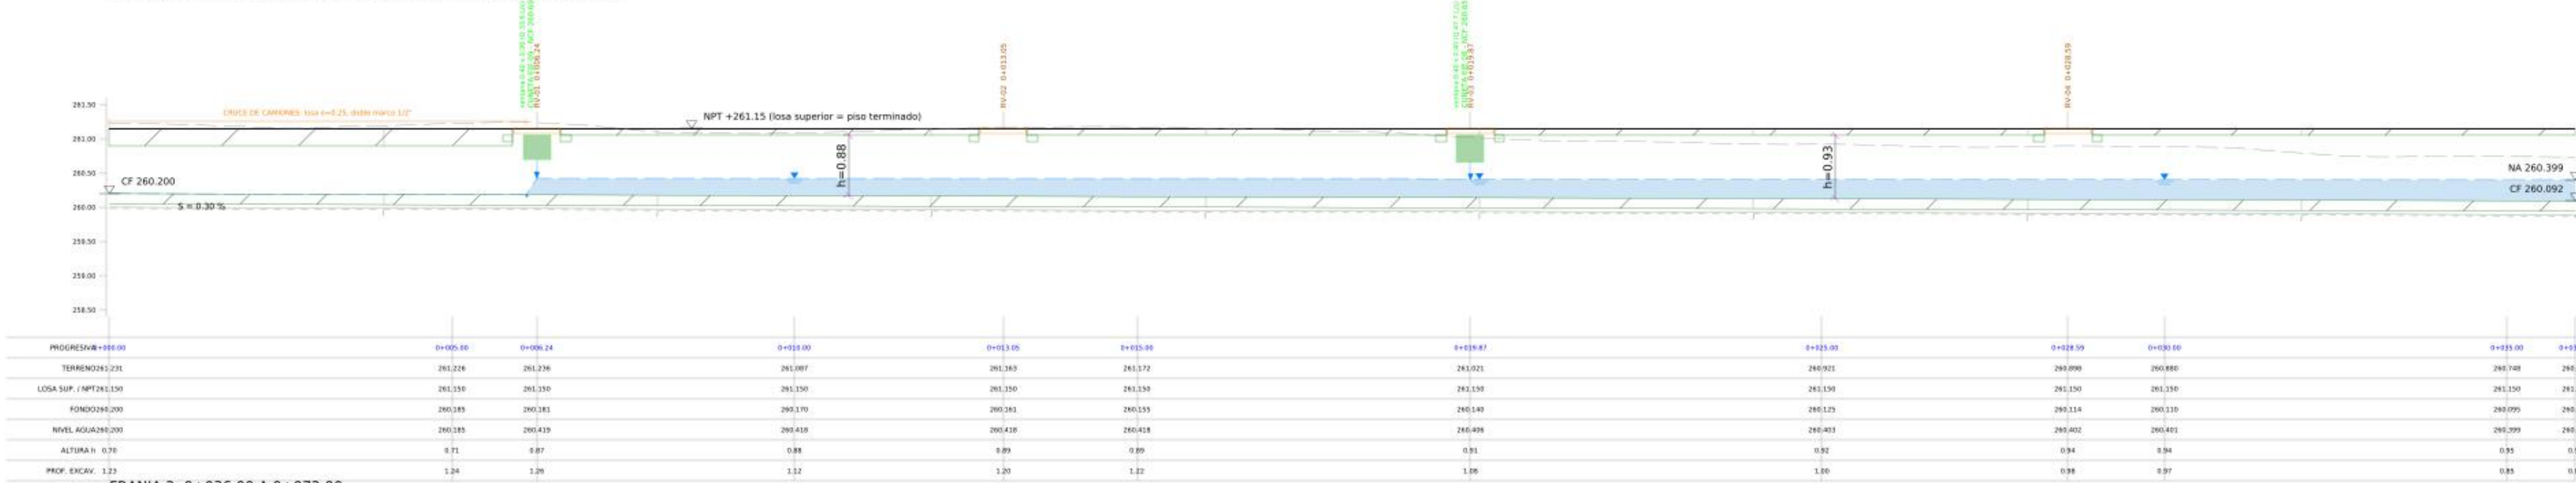

FRANJA 2: 0+036.00 A 0+072.00



FRANJA 3: 0+072.00 A 0+105.29 - LLEGADA A LA CAJA CL DEL HOGAR DE REFUGIO

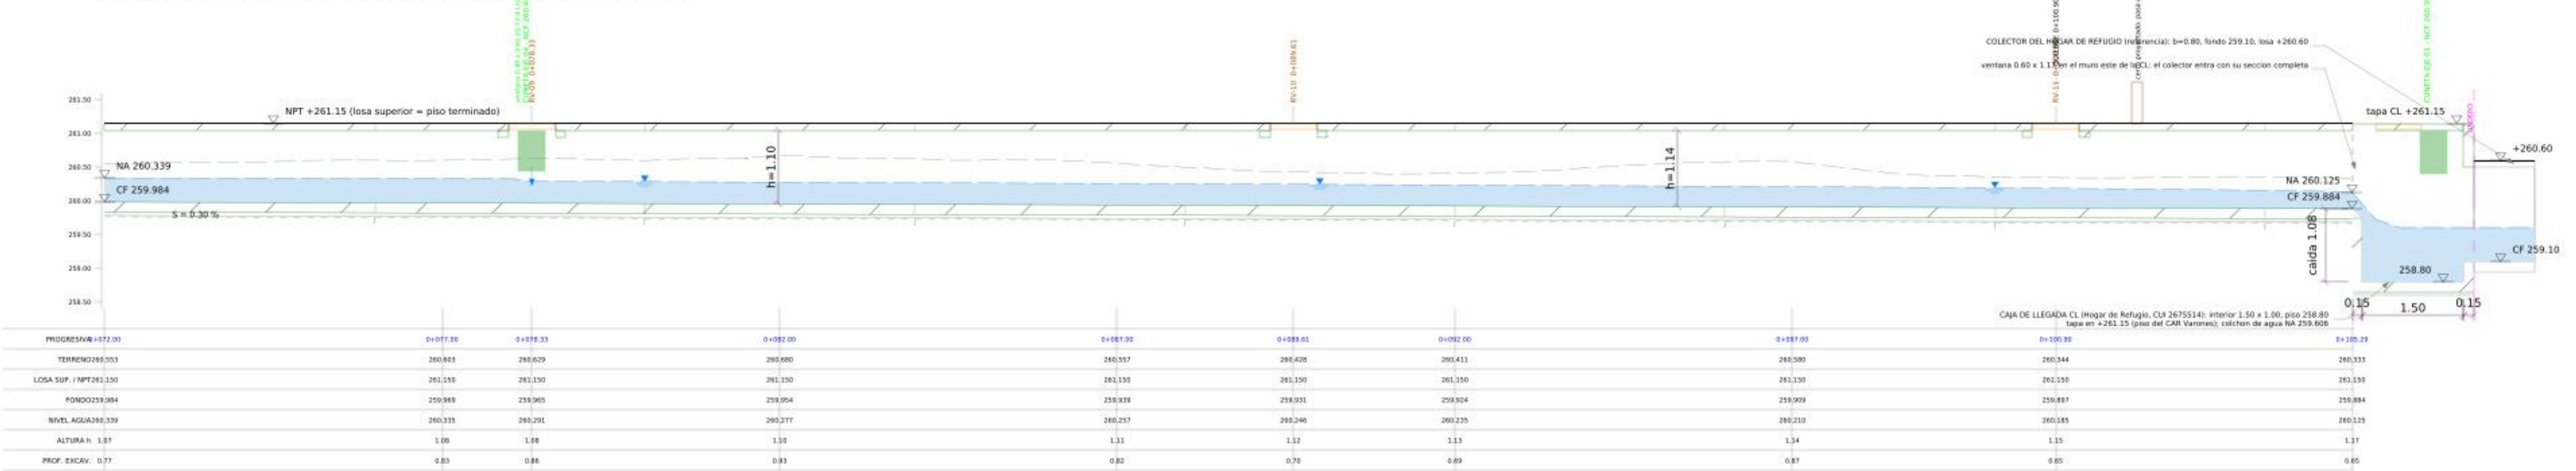


LEYENDA

- piso terminado / losa superior (NPT +261.15)
- terreno existente (superficie topográfica)
- concreto armado cortado (losa, caja CL)
- solado e=0.05 y límite de excavación
- agua: nivel de diseño (Q = 221.7 l/s al final)
- tapa de registro 0.68 x 0.68 x 0.08
- ventana de llegada de cuneta 0.40 x H (cara interior del muro lado predio)
- junta de dilatación cada 4.00 m
- colector del Hogar de Refugio (referencia)

NOTAS


- Corte longitudinal por el eje a escala real 1/50, horizontal = vertical. Cotas en m.s.n.m. Se ve la cara interior del muro lado predio con las ventanas de las cunetas.
- Nivel de agua por flujo gradualmente variado con caudal creciente en cada empalme (memoria, hoja PERFIL FLUJO); control: tramo crítico en la caída libre a la caja CL.
- Caudales: Eje 09 33.6 + Eje 08 47.7 + Eje 06 68.0 + Eje 04 72.4 = 221.7 l/s en el colector; la cuneta del Eje 01 (97.0 l/s) entra directamente a la CL total 258.7 l/s (TR 25 años).
- Registros con tapa de concreto 0.68 x 0.68 x 0.08, borde engrosado y contramarcado metálico (DP-068, DD-01, DD-02). No hay registros dentro del cruce de camiones.
- La caja CL y el colector del Hogar de Refugio (CUI 2675514) se muestran como referencia; la tapa de la CL queda en +261.15 (piso del CAR Varones).
- Prof. excav. medida desde el terreno existente al fondo del solado. Relleno de revelación del retro hasta +261.15 donde el terreno queda por debajo.

PROYECTO: CREACIÓN DEL SERVICIO DE PROTECCIÓN INTEGRAL A NIÑAS, NIÑOS Y ADOLESCENTES SIN CUIDADOS PARENTALES O EN RIESGO DE PERDERLOS EN CENTRO DE ACOGIDA RESIDENCIAL - VARONES, DISTRITO DE MORALES, PROVINCIA Y DEPARTAMENTO DE SAN MARTÍN - CLJ N. 2705639 ENTIDAD: GERENCIA TERRITORIAL BAJO MAYO - TARAPOTO		
UBICACIÓN: PREDIO ALDEA INFANTIL VIRGEN DEL PILAR - MORALES - SAN MARTÍN - SAN MARTÍN ESPECIALIDAD: INSTALACIONES SANITARIAS - DRENAJE PLUVIAL		
PLANO: PERFIL LONGITUDINAL DEL COLECTOR ESCALA REAL 1/50 (H = V) - CORTE POR EL EJE EN TRES FRANJAS: NIVELES DE DISEÑO, PERFIL HIDRAULICO, REGISTROS, ENPALMES Y LLEGADA A LA CAJA CL DEL HOGAR DE REFUGIO		
PROYECTISTA: _____	CIP: _____	
ELABORADO: HIDROCONSULT	ESCALA: 1/50	
REVISADO: _____	FECHA: OCT. 2026	LAMINA: _____
FIRMA Y SELLO: _____	REVISION: 00	DP-02

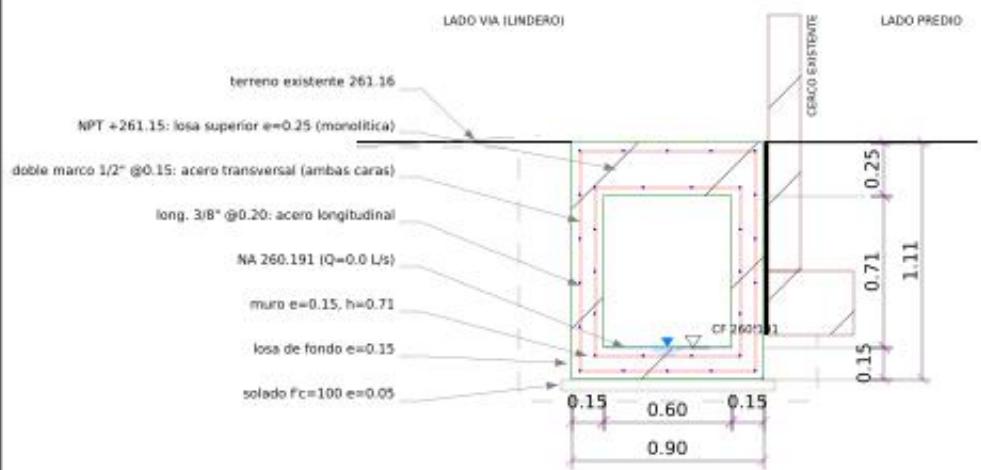


SECCION S-01

PROG. 0+003.00 - CF 260.191 - CRUCE DE CAMIONES - ESC. 1/25

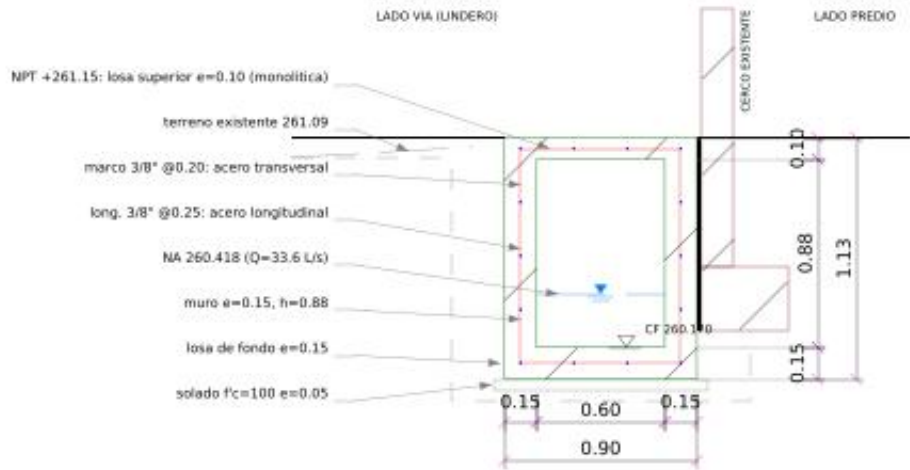


SECCION S-02

PROG. 0+010.00 - CF 260.170 - TRAMO NORMAL - ESC. 1/25

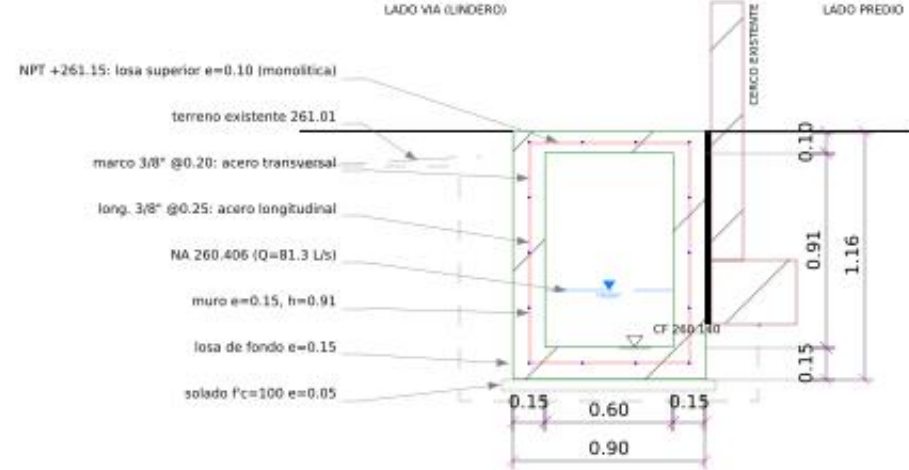

SECCION S-03

PROG. 0+020.00 - CF 260.140 - TRAMO NORMAL - ESC. 1/25

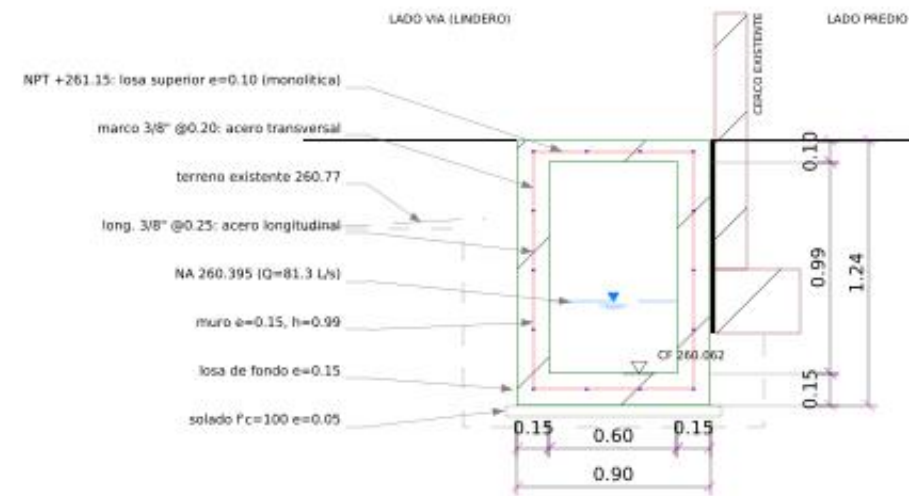

SECCION S-04

PROG. 0+046.00 - CF 260.062 - TRAMO NORMAL - ESC. 1/25


LEYENDA

- concreto armado $f'c=210$ kg/cm²
- solado $f'c=100$ kg/cm²
- acero transversal: marco cerrado (rojo)
- acero longitudinal 3/8" (círculo a diámetro real)
- nivel de agua de diseño
- piso terminado +261.15
- terreno existente
- límite de excavación
- cercos perimetricos existentes

NOTAS


- Altura interior h según el perfil longitudinal: 0.70 m en el cruce de camiones (losa $e=0.25$), 0.85 m en 0+006.08 y 1.17 m en la llegada a la CL.
- Tramo normal: un solo marco cerrado 3/8" @0.20 en el eje de muros y losas (una capa, E.060 14.3.4); recubrimiento 0.04 m en muros y losa de fondo y 0.025 m en la losa superior.
- Junta de techos de 1" entre el muro lado predio y el cimbrado del cerco; junta de 1" entre la losa superior y el piso adyacente (+261.15).
- El cruce de camiones sistema (S-01, 0+000.00 - 0+006.08) lleva losas $e=0.25$ y doble marco de 1/2" @0.15 (marco exterior e interior, recubrimiento 0.04).
- Los registros no se ubican dentro del cruce de camiones. No hay cruce de motos en este tramo.

PROYECTO: CREACIÓN DEL SERVICIO DE PROTECCIÓN INTEGRAL A NIÑAS, NIÑOS Y ADOLESCENTES SIN CUIDADOS PARENTALES O EN RIESGO DE PERDERLOS EN CENTRO DE ACOGIDA RESIDENCIAL - VARONES, DISTRITO DE MORALES, PROVINCIA Y DEPARTAMENTO DE SAN MARTÍN - CLJ N. 2705639 ENTIDAD: GERENCIA TERRITORIAL BAJO MAYO - TARIAPOTO		
UBICACIÓN: PREDIO ALDEA INFANTIL VIRGEN DEL PILAR - MORALES - SAN MARTÍN - SAN MARTÍN ESPECIALIDAD: INSTALACIONES SANITARIAS - DRENAJE PLUVIAL		
PLANO: SECCIONES TRANSVERSALES DEL COLECTOR SECCIONES S-01 A S-04 CON DISTRIBUCIÓN DE ACERO - ESC. 1/25		
PROYECTISTA: _____ CIP: _____		
ELABORADO: HIDROCONSULT	ESCALA: 1/25	
REVISADO: _____	FECHA: OCT. 2026	LÁMINA: _____
FIRMA Y SELLO: _____	REVISIÓN: 00	

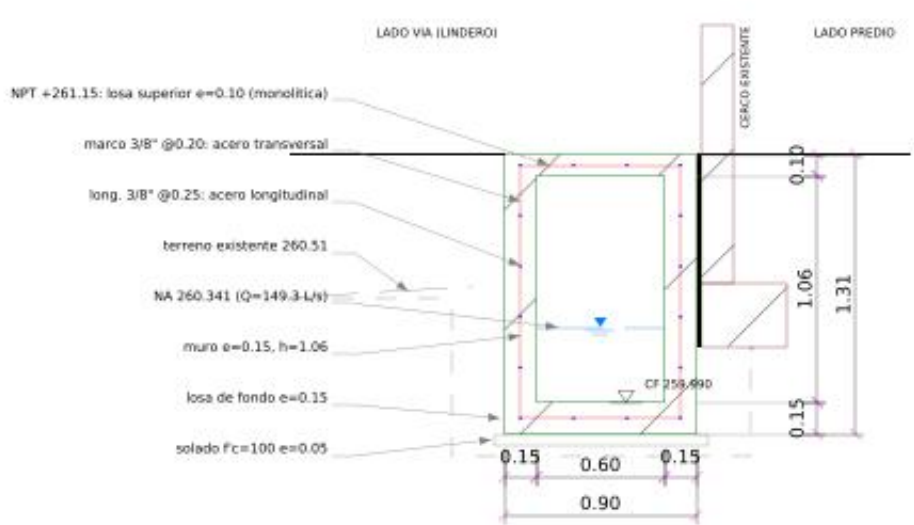


SECCION S-05

PROG. 0+070.00 - CF 259.990 - TRAMO NORMAL - ESC. 1/25

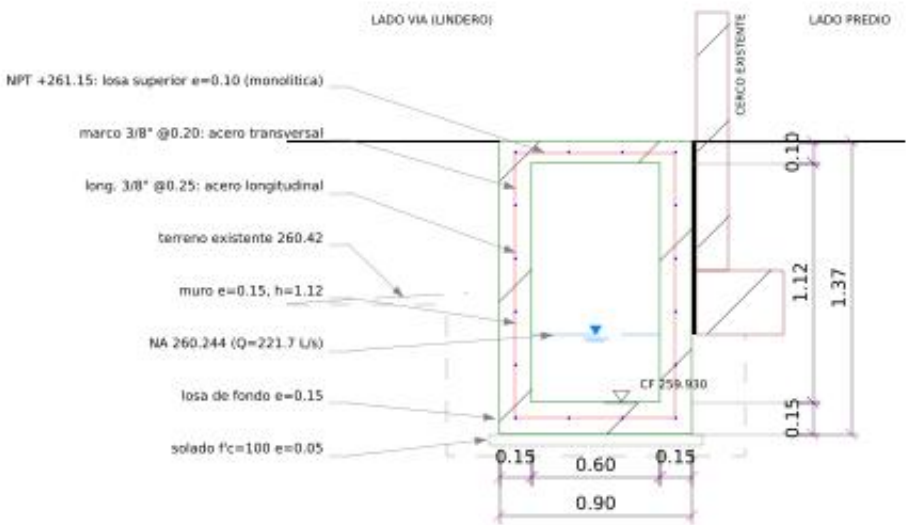


SECCION S-06

PROG. 0+090.00 - CF 259.930 - TRAMO NORMAL - ESC. 1/25

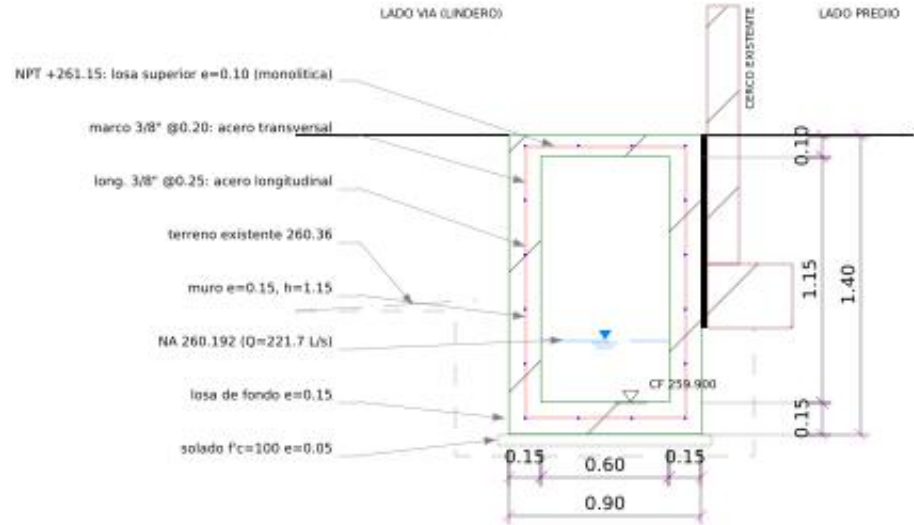

SECCION S-07

PROG. 0+100.00 - CF 259.900 - TRAMO NORMAL - ESC. 1/25

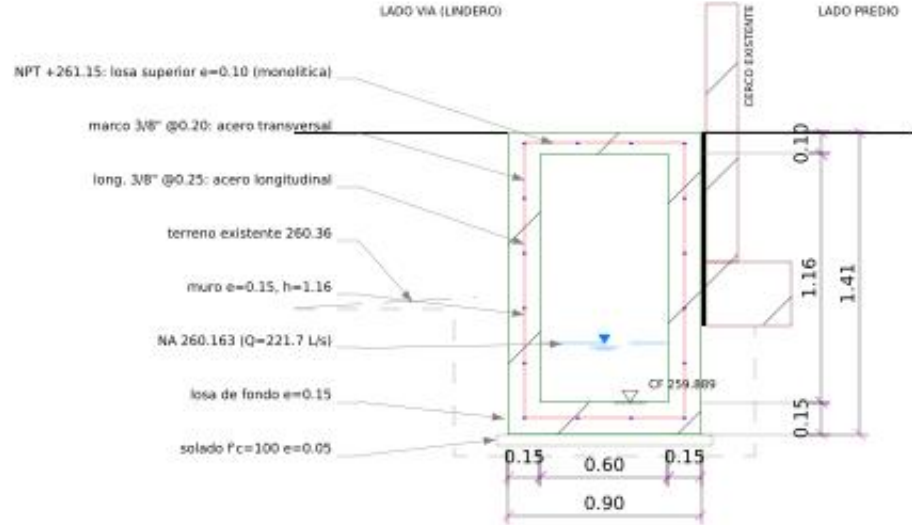

SECCION S-08

PROG. 0+103.50 - CF 259.889 - TRAMO NORMAL - ESC. 1/25


LEYENDA

- concreto armado $f'c=210$ kg/cm²
- solado $f'c=100$ kg/cm²
- acero transversal: marco cerrado (rojo)
- acero longitudinal 3/8" (círculo a diámetro real)
- nivel de agua de diseño
- piso terminado +261.15
- terreno existente
- límite de excavación
- cercos perimetricos existentes

NOTAS


- Altura interior h según el perfil longitudinal: 0.70 m en el cruce de camiones (losa e=0.25), 0.85 m en 0+096.08 y 1.17 m en la llegada a la CL.
- Tramo normal: un solo marco cerrado 3/8" @0.20 en el eje de muros y losas (una capa, E.060 14.3.4); recubrimiento 0.04 m en muros y losa de fondo y 0.025 m en la losa superior.
- Junta de techos de 1" entre el muro lado predio y el cimbrado del cerco; junta de 1" entre la losa superior y el piso adyacente (+261.15).
- El cruce de camiones sistema (S-01, 0+000.00 - 0+006.08) lleva losas e=0.25 y doble marco de 1/2" @0.15 (marco exterior e interior, recubrimiento 0.04).
- Los registros no se ubican dentro del cruce de camiones. No hay cruce de motos en este tramo.

PROYECTO: CREACIÓN DEL SERVICIO DE PROTECCIÓN INTEGRAL A NIÑAS, NIÑOS Y ADOLESCENTES SIN CUIDADOS PARENTALES O EN RIESGO DE PERDERLOS EN CENTRO DE ACOGIDA RESIDENCIAL - VARONES, DISTRITO DE MORALES, PROVINCIA Y DEPARTAMENTO DE SAN MARTÍN - CLJ N. 2705639 ENTIDAD: GERENCIA TERRITORIAL BAJO MAYO - TARAPOTO		
UBICACIÓN: PREDIO ALDEA INFANTIL VIRGEN DEL PILAR - MORALES - SAN MARTÍN - SAN MARTÍN ESPECIALIDAD: INSTALACIONES SANITARIAS - DRENAJE PLUVIAL		
PLANO: SECCIONES TRANSVERSALES DEL COLECTOR SECCIONES S-05 A S-08 CON DISTRIBUCIÓN DE ACERO - ESC. 1/25		
PROYECTISTA: _____ CIP: _____		
ELABORADO: HIDROCONSULT	ESCALA: 1/25	
REVISADO: _____	FECHA: OCT. 2026	LÁMINA: _____
FIRMA Y SELLO: _____	REVISIÓN: 00	

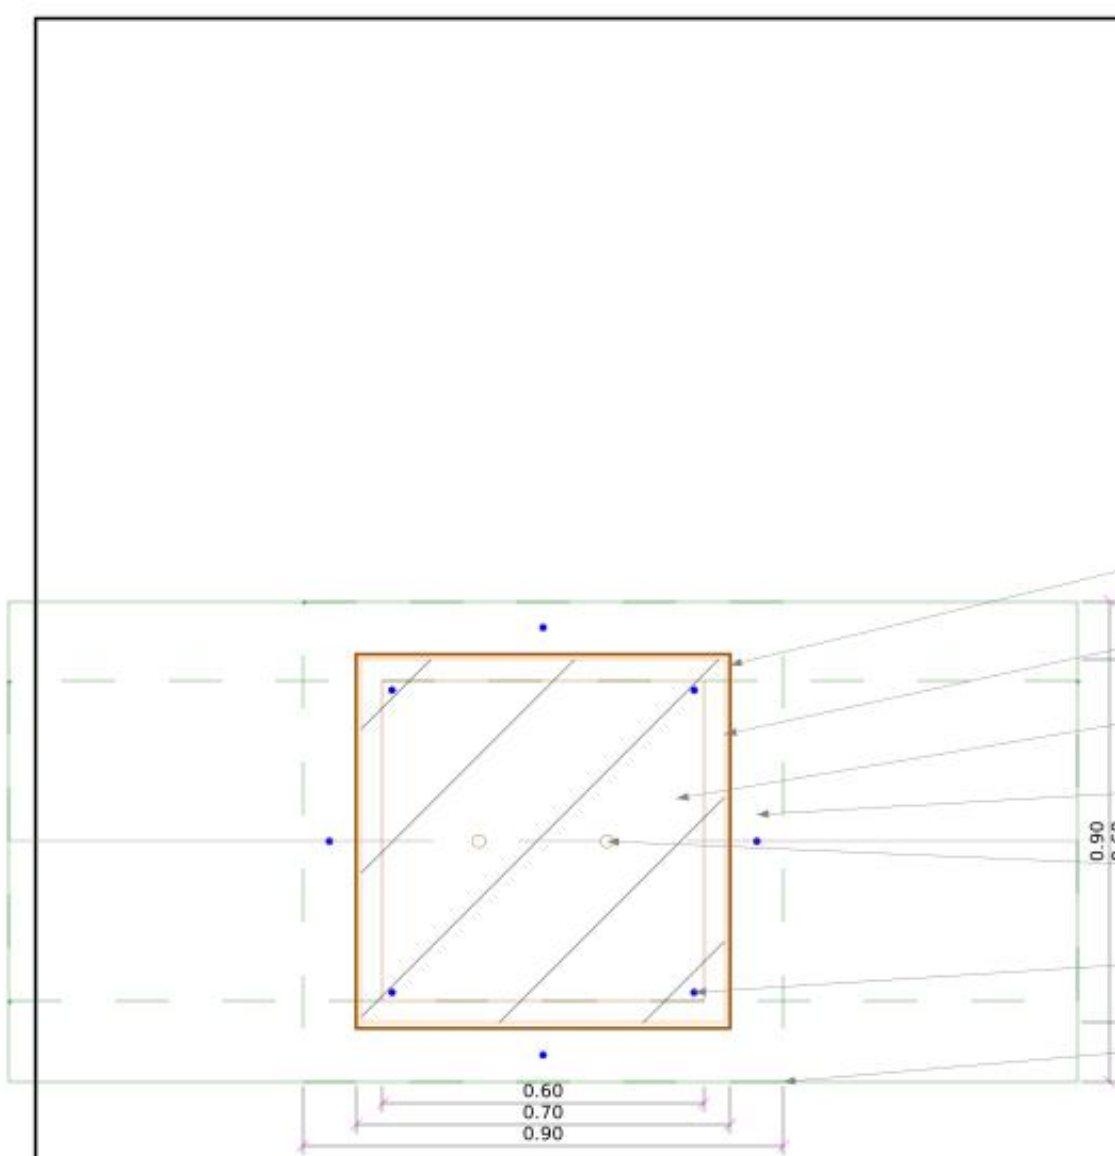


A. REGISTRO DE LIMPIEZA - PLANTA

ESC. 1/10 - 11 und (RV-01 a RV-11), todos en la losa del colector

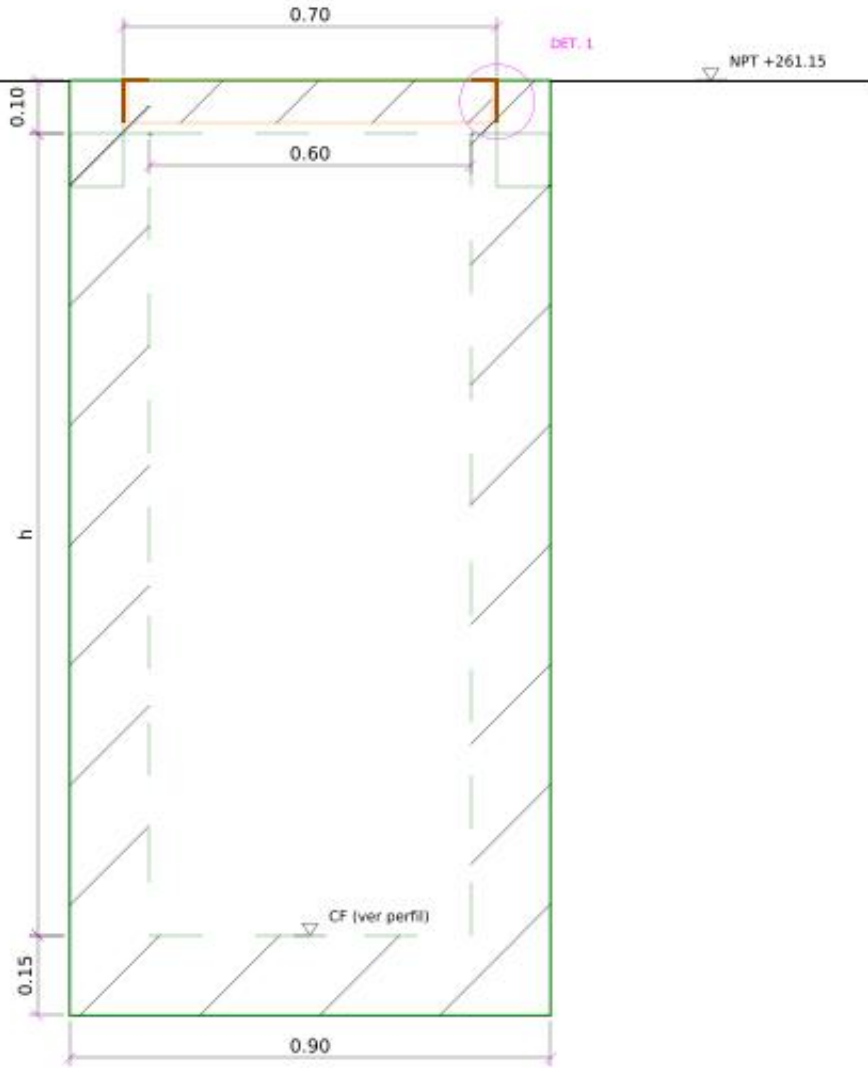

B. CORTE A-A POR EL REGISTRO


ESC. 1/10

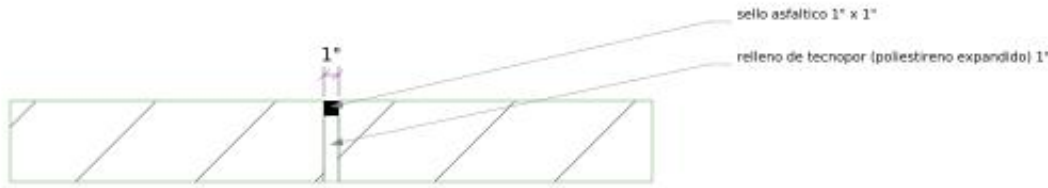

F. JUNTA DE DILATACION CADA 4.00 m


ESC. 1/5 aprox. - en muros, losa de fondo y losa superior

- contramarco: angulo L 2"x2"x3/16" (perimetro 0.70 x 0.70)
- marco de tapa: angulo L 1 1/2"x1 1/2"x1/8" (0.68 x 0.68)
- tapa de concreto armado 0.68 x 0.68 x 0.08 (removible)
- anclajes 3/8" L=0.20 soldados (2 por lado)
- asas: 2 de 3/8" liso, embutidas
- refuerzo de borde: 2 barras 1/2" por lado, L=1.40
- borde engrosado 0.15 x 0.10 bajo la losa (oculto)

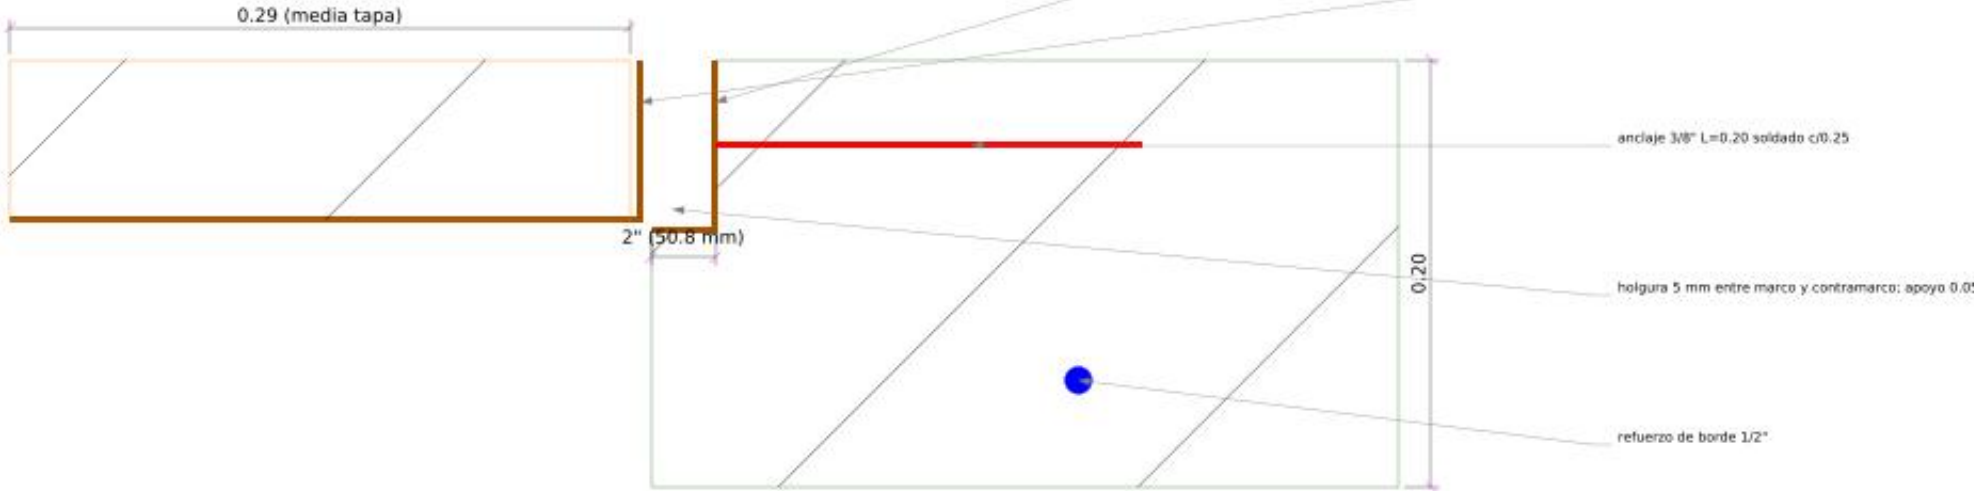


C. DETALLE 1: APOYO DE TAPA

ESC. 1/2.5

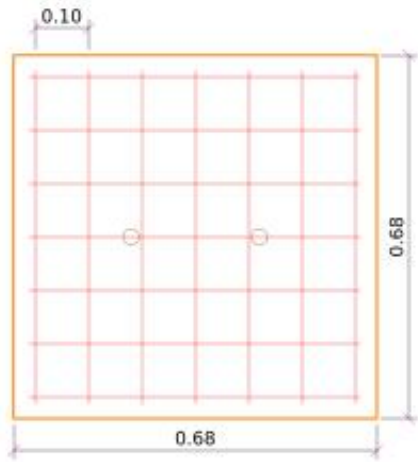

D. TAPA - ARMADO

7 + 7 barras 3/8" @0.10, L=0.62; asas 3/8" liso

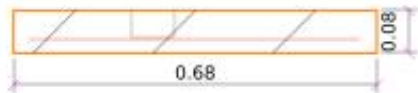

D. TAPA - CORTE

concreto f'c=210 kg/cm2 - peso aprox. 95 kg


MATERIALES POR REGISTRO

Contramarco angulo L 2"x2"x3/16": 4 x 0.70 = 2.80 m (10.2 kg); anclajes 3/8" L=0.20: 8 und
Marco de tapa angulo L 1 1/2"x1 1/2"x1/8": 4 x 0.68 = 2.72 m (5.0 kg)
Acero tapa 3/8" @0.10: 14 x 0.62 = 8.68 m (4.9 kg); asas 3/8" liso: 2 x 0.40 m
Concreto tapa f'c=210: 0.68 x 0.68 x 0.08 = 0.037 m3
Refuerzo de borde 1/2": 8 x 1.40 = 11.20 m (11.1 kg); borde engrosado: perimetro 3.00 x 0.15 x 0.10 = 0.045 m3

LEYENDA

- concreto armado f'c=210 kg/cm2
- angulos metalicos (marco y contramarco)
- tapa removible
- acero de refuerzo
- junta de dilatacion / tecnopor

PROYECTO: CREACION DEL SERVICIO DE PROTECCION INTEGRAL A NIÑAS, NIÑOS Y ADOLESCENTES SIN CUIDADOS PARENTALES O EN RIESGO DE PERDERLOS EN CENTRO DE ACOGIDA RESIDENCIAL - VARONES, DISTRITO DE MORALES, PROVINCIA Y DEPARTAMENTO DE SAN MARTIN - CJA N. 2705639 ENTIDAD: GERENCIA TERRITORIAL BAJO MAYO - TARAPOTO		
UBICACION: PREDIO ALDEA INFANTIL VIRGEN DEL PILAR - MORALES - SAN MARTIN - SAN MARTIN ESPECIALIDAD: INSTALACIONES SANITARIAS - DRENAJE PLUVIAL		
PLANO: DETALLES DE REGISTRO DE LIMPIEZA, TAPA, MARCO Y CONTRAMARCO REGISTRO CON TAPA REMOVIBLE, ANGULOS METALICOS, EMPALME DE CUNETAS Y JUNTA DE DILATACION		
PROYECTISTA: _____ CIP: _____		
ELABORADO: HIDROCONSULT	ESCALA: 1/10	
REVISADO: _____	FECHA: OCT. 2026	LAMINA:
FIRMA Y SELLO:	REVISION: 00	

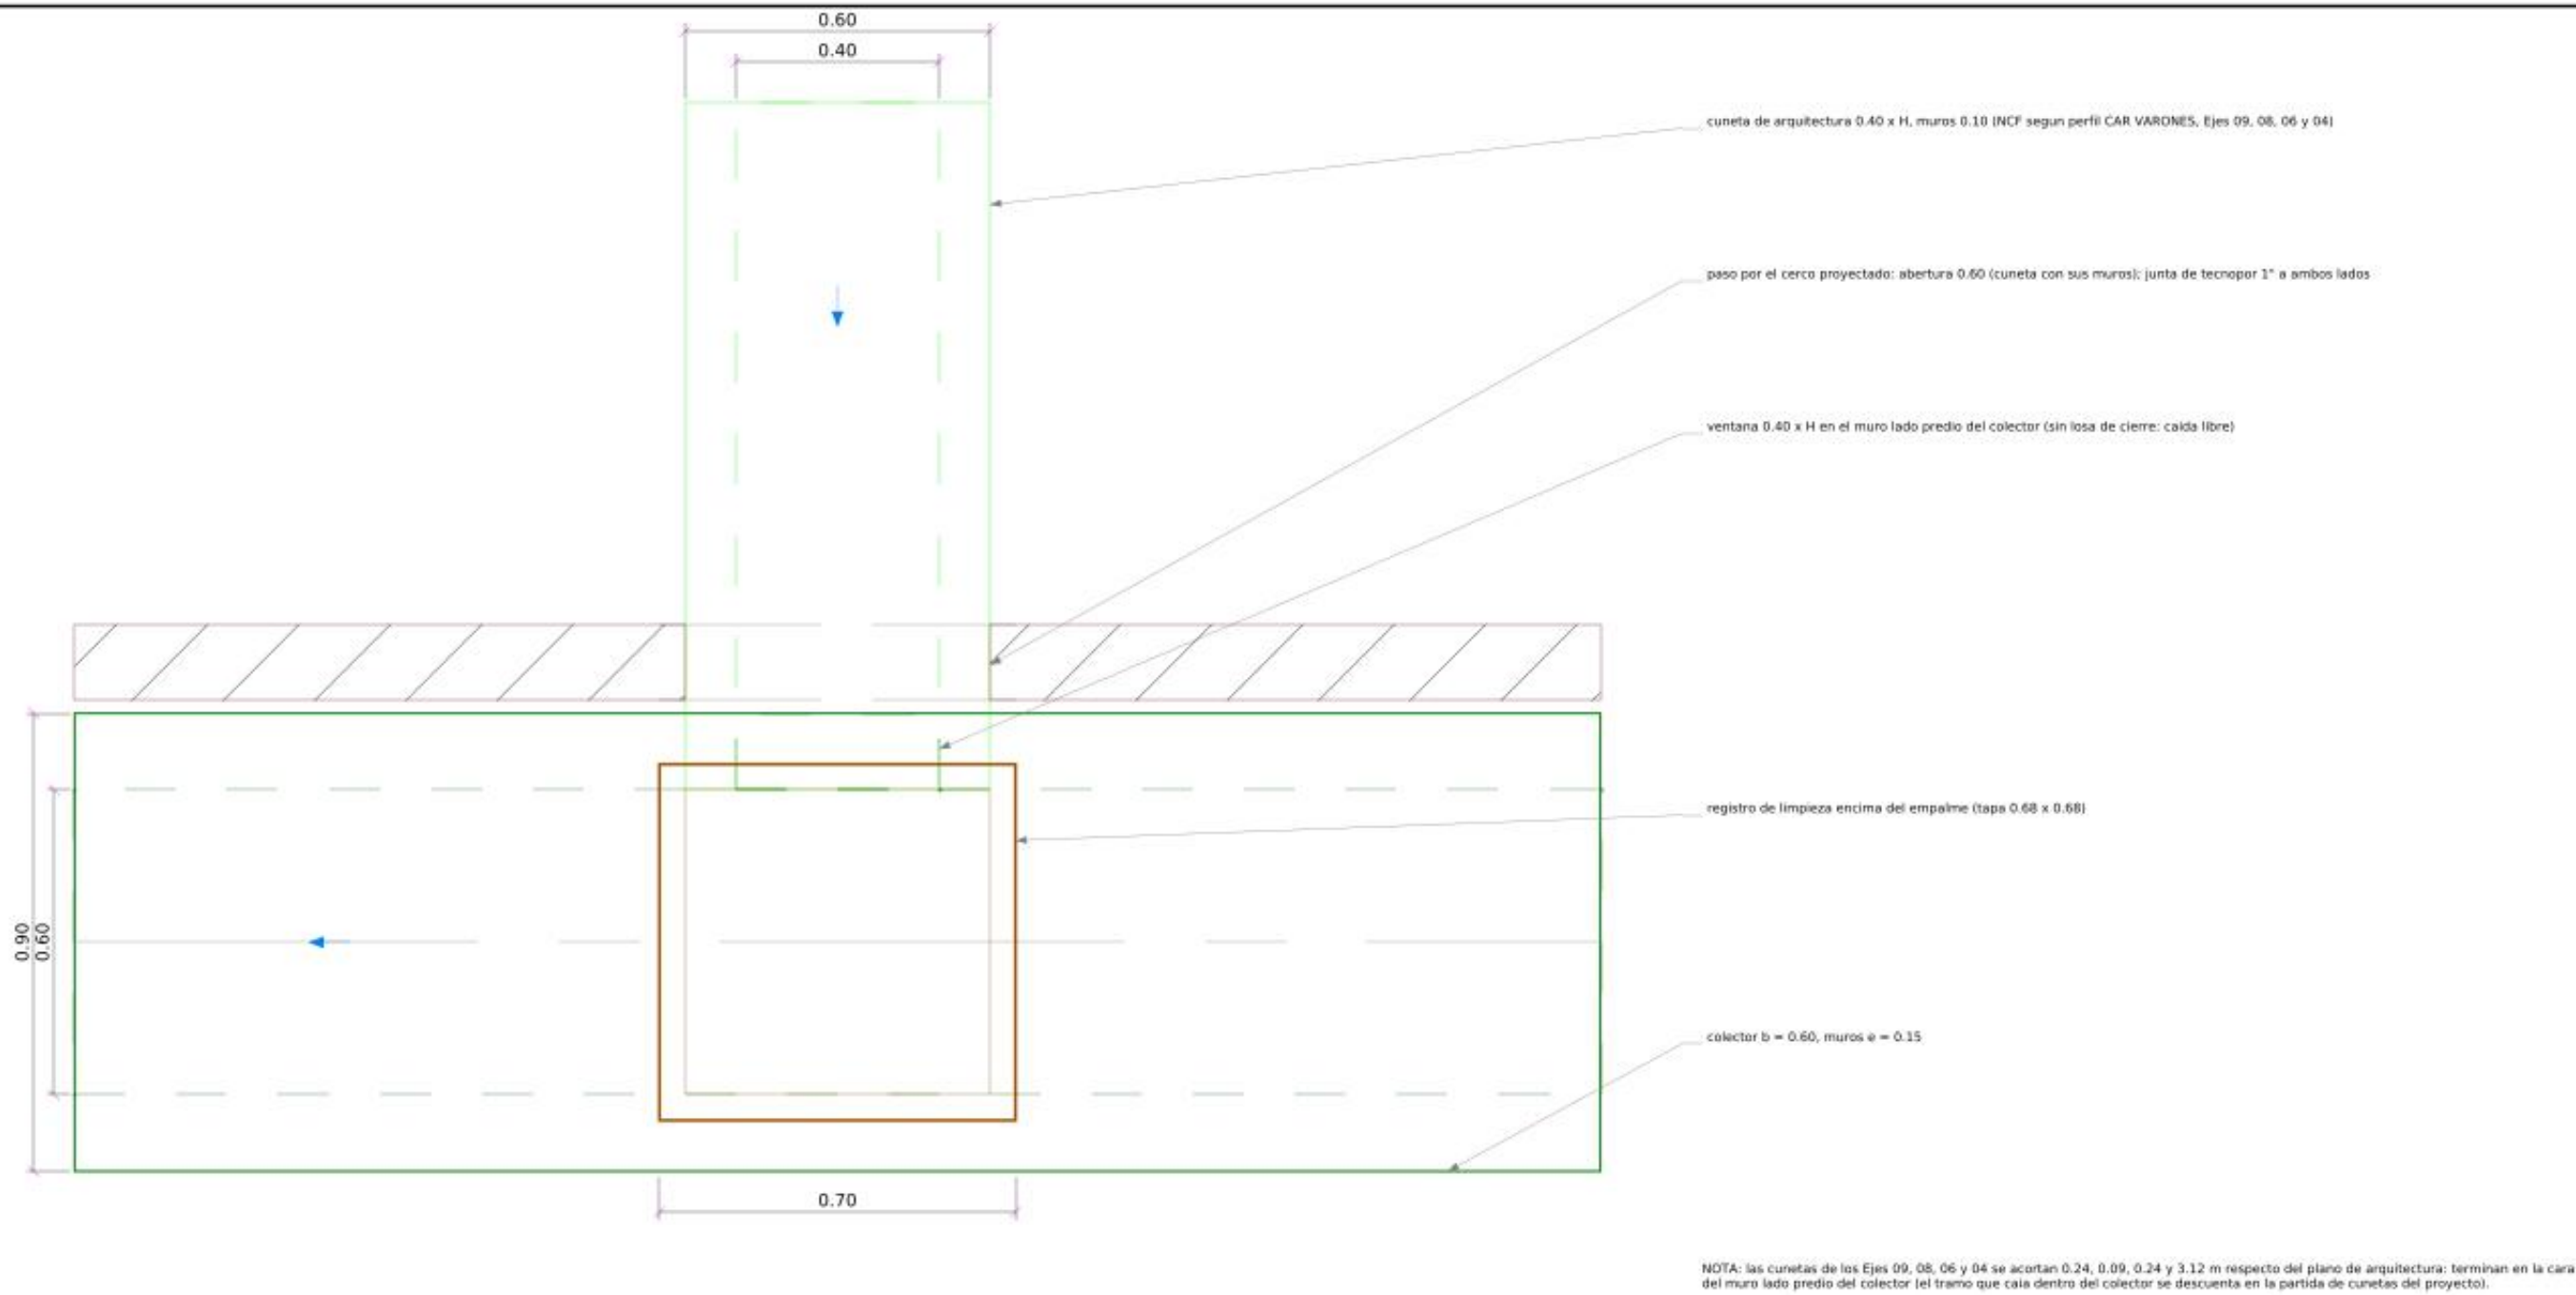

E1. EMPALME DE CUNETA - PLANTA
ESC. 1/10 - losa superior retirada para mostrar la ventana


LEYENDA

- concreto armado del colector f'c=210
- cuneta y cerco existentes (arquitectura)
- cuneta de arquitectura
- junta de tecnopor 1"
- nivel de agua
- sentido del flujo

CUADRO DE EMPALMES


CUNETA	PROG.	NCF LLEGA	H VENTANA	REGISTRO
Eje 09	0+006.24	260.69	0.36	RV-01
Eje 08	0+019.87	260.65	0.40	RV-03
Eje 06	0+046.02	260.46	0.59	RV-06
Eje 04	0+078.33	260.44	0.61	RV-09
Eje 01	0+105.29	260.39	0.66	CL

* cuneta Eje 01: no entra al colector; cae directamente a la caja de llegada CL por una ventana en su muro norte (ver DP-07).

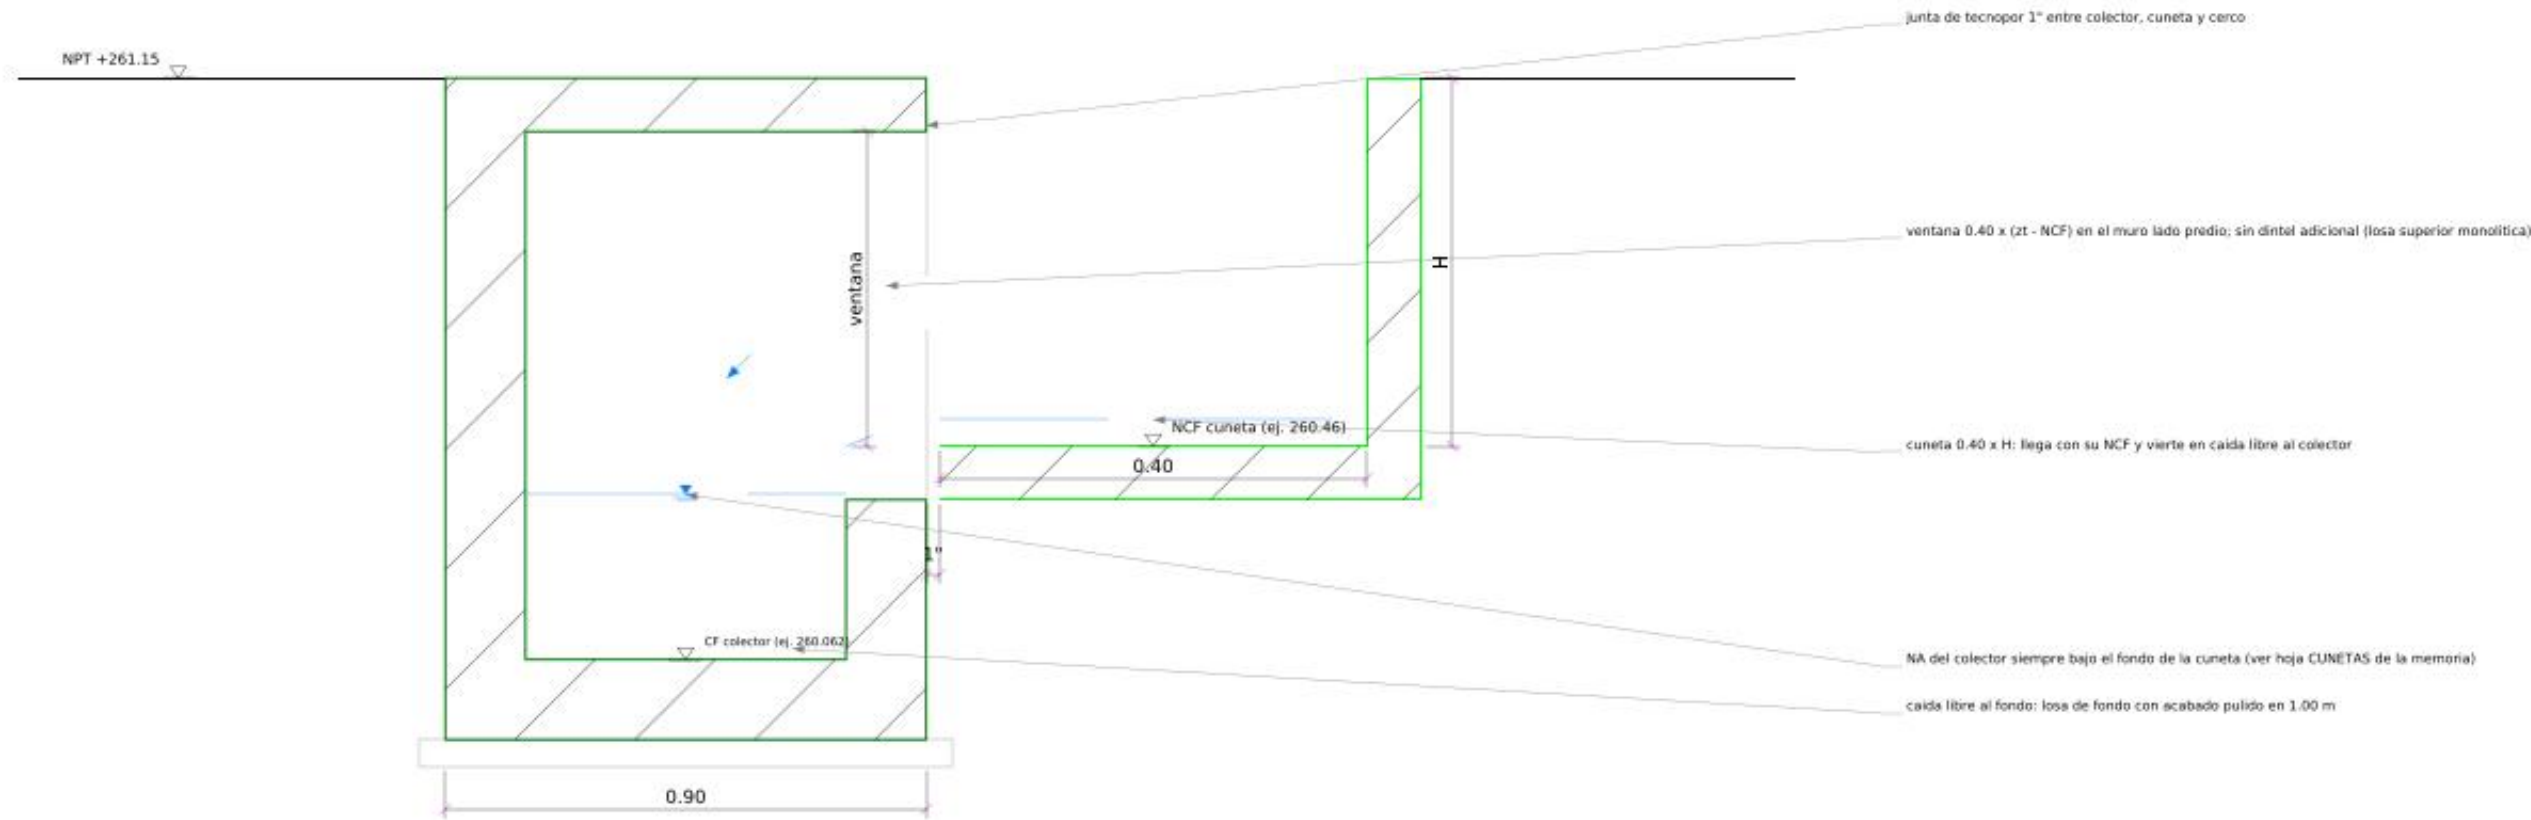

E2. EMPALME DE CUNETA - CORTE TRANSVERSAL (MIRANDO AGUAS ABAJO)
ESC. 1/10 - ejemplo cuneta Eje 06 (0+046.02, registro RV-06); en las demas varia H y la cota de fondo

PROYECTO: CREACIÓN DEL SERVICIO DE PROTECCIÓN INTEGRAL A NIÑAS, NIÑOS Y ADOLESCENTES SIN CUIDADOS PARENTALES O EN RIESGO DE PERDERLOS EN CENTRO DE ACOGIDA RESIDENCIAL - VARONES, DISTRITO DE MORALES, PROVINCIA Y DEPARTAMENTO DE SAN MARTÍN - CLJ N. 2705639 ENTIDAD: GERENCIA TERRITORIAL BAJO MAYO - TARIAPOTO		
UBICACION: PREDIO ALDEA INFANTIL VIRGEN DEL PILAR - MORALES - SAN MARTÍN - SAN MARTÍN ESPECIALIDAD: INSTALACIONES SANITARIAS - DRENAJE PLUVIAL		
PLANO: DETALLE DEL EMPALME DE CUNETA AL COLECTOR VENTANA EN EL MURO LADO PREDIO, CAIDA AL FONDO, JUNTAS Y REGISTRO - CUNETAS EJES 09, 08, 06 Y 04 - ESC. 1/10		
PROYECTISTA: _____ CIP: _____		
ELABORADO: HIDROCONSULT	ESCALA: 1/10	
REVISADO: _____	FECHA: OCT. 2026	LÁMINA:
FIRMA Y SELLO:	REVISION: 00	

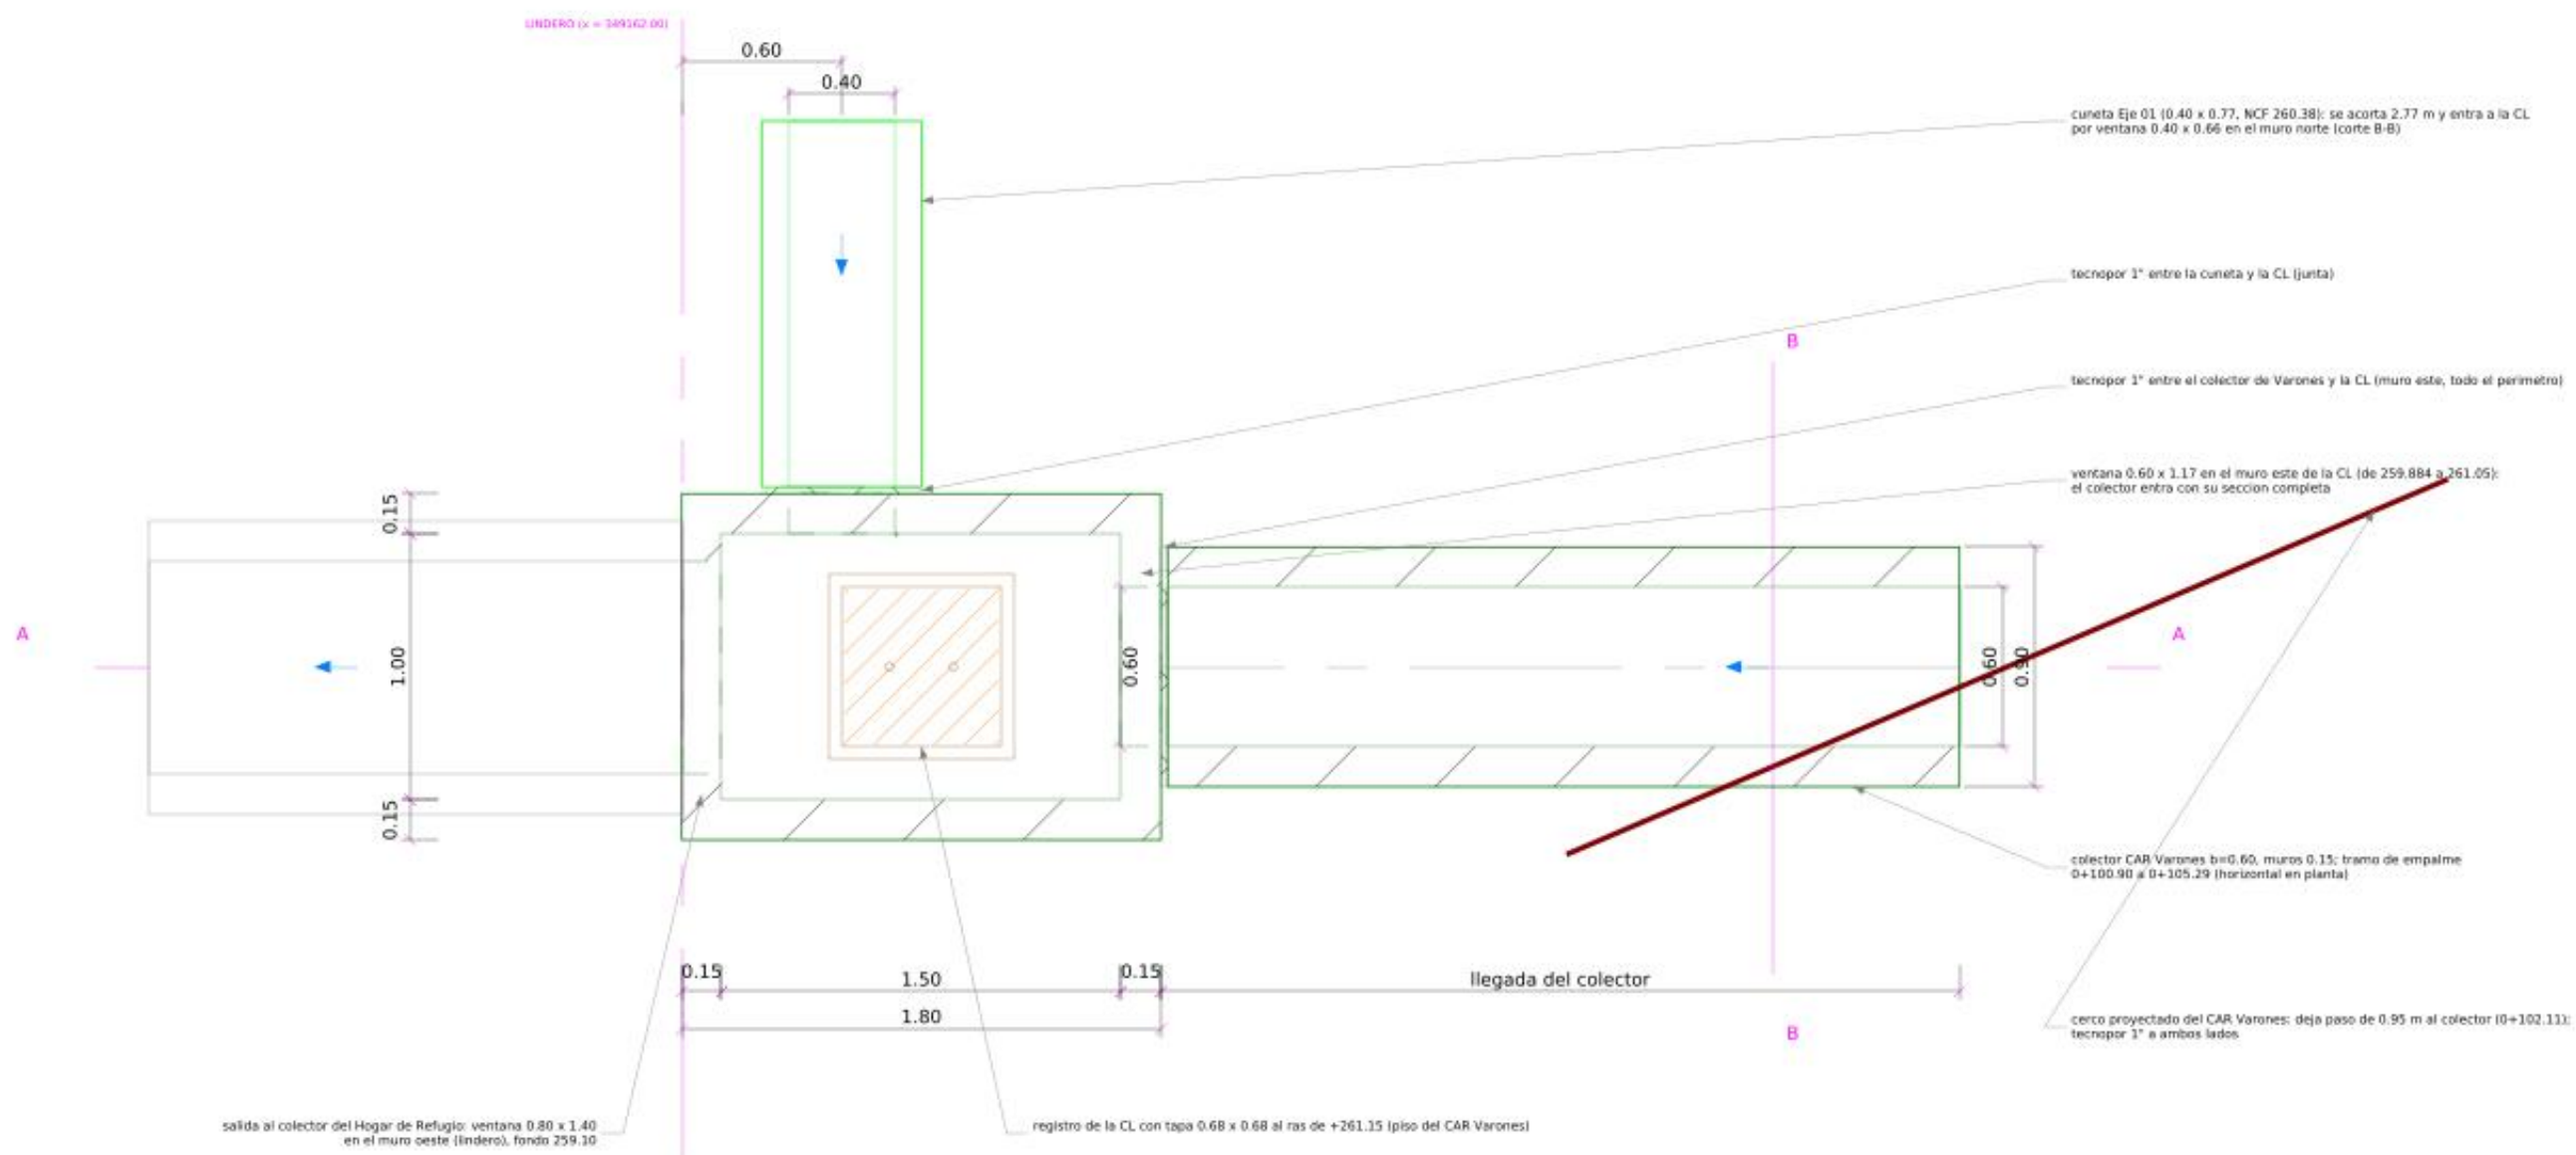

LEYENDA

concreto armado $f_c=210$ (CL: expediente del Hogar de Refugio)

colector del Hogar de Refugio (referencia)

cuneta de arquitectura (Eje 01)

ventana de llegada de cuneta

junta de tecnopor 1"

agua (nivel de diseño)

cercos proyectados

límetro entre predios

sentido del flujo

CUADRO DE LLEGADAS A LA CAJA CL

APORTE	UBICACION	Q (l/s)	COTA FONDO	VENTANA	CAIDA LIBRE (m)
Colector CAR Varones	0+105.29	221.7	259.884	ventana este 0.60 x 1.17	0.28
Cuneta Eje 01	muro norte	37.0	260.39	ventana norte 0.40 x 0.66	0.79
TOTAL a la CL		258.7		puza: piso 258.80, NA 259.606	

- NOTAS
1. La caja CL pertenece al expediente del Hogar de Refugio Temporal (CL: 2675514, lámina DP-07 de ese trámite); aquí se dibuja para definir el empalme. Queda del lado del CAR Varones ($x = 349162.00$ a 349163.80), por eso su tapa está en $+261.15$.

2. Coordinación entre expedientes: en la CL se dejan la ventana este 0.60×1.17 (cota de fondo 259.884) y la ventana norte 0.40×0.66 (NCF 260.39). El CAR Varones entrega 221.7 l/s (colector) + 37.0 l/s (cuneta Eje 01) = 258.7 l/s.


3. Si la CL se construye antes que el colector de Varones, las ventanas se dejan tapadas con muro de ladrillo pandereta (sin mortero de unión a la CL) para retirarlo al empalmar; si se construye después, el colector de Varones termina en tapon provisional.

4. Juntas de tecnopor 1" en todo el contacto entre estructuras de distinto expediente (colector - CL, cuneta - CL, colector - cerco).

5. El tramo de empalme $0+100.90$ a $0+105.29$ es horizontal en planta y mantiene la pendiente 0.30 ‰; registro RV-11 en el quiebre.

A. EMPALME CON LA CAJA CL - PLANTA

ESC. 1/20 - losas superiores retradas: norte hacia arriba del dibujo (sistema local del plano de arquitectura)

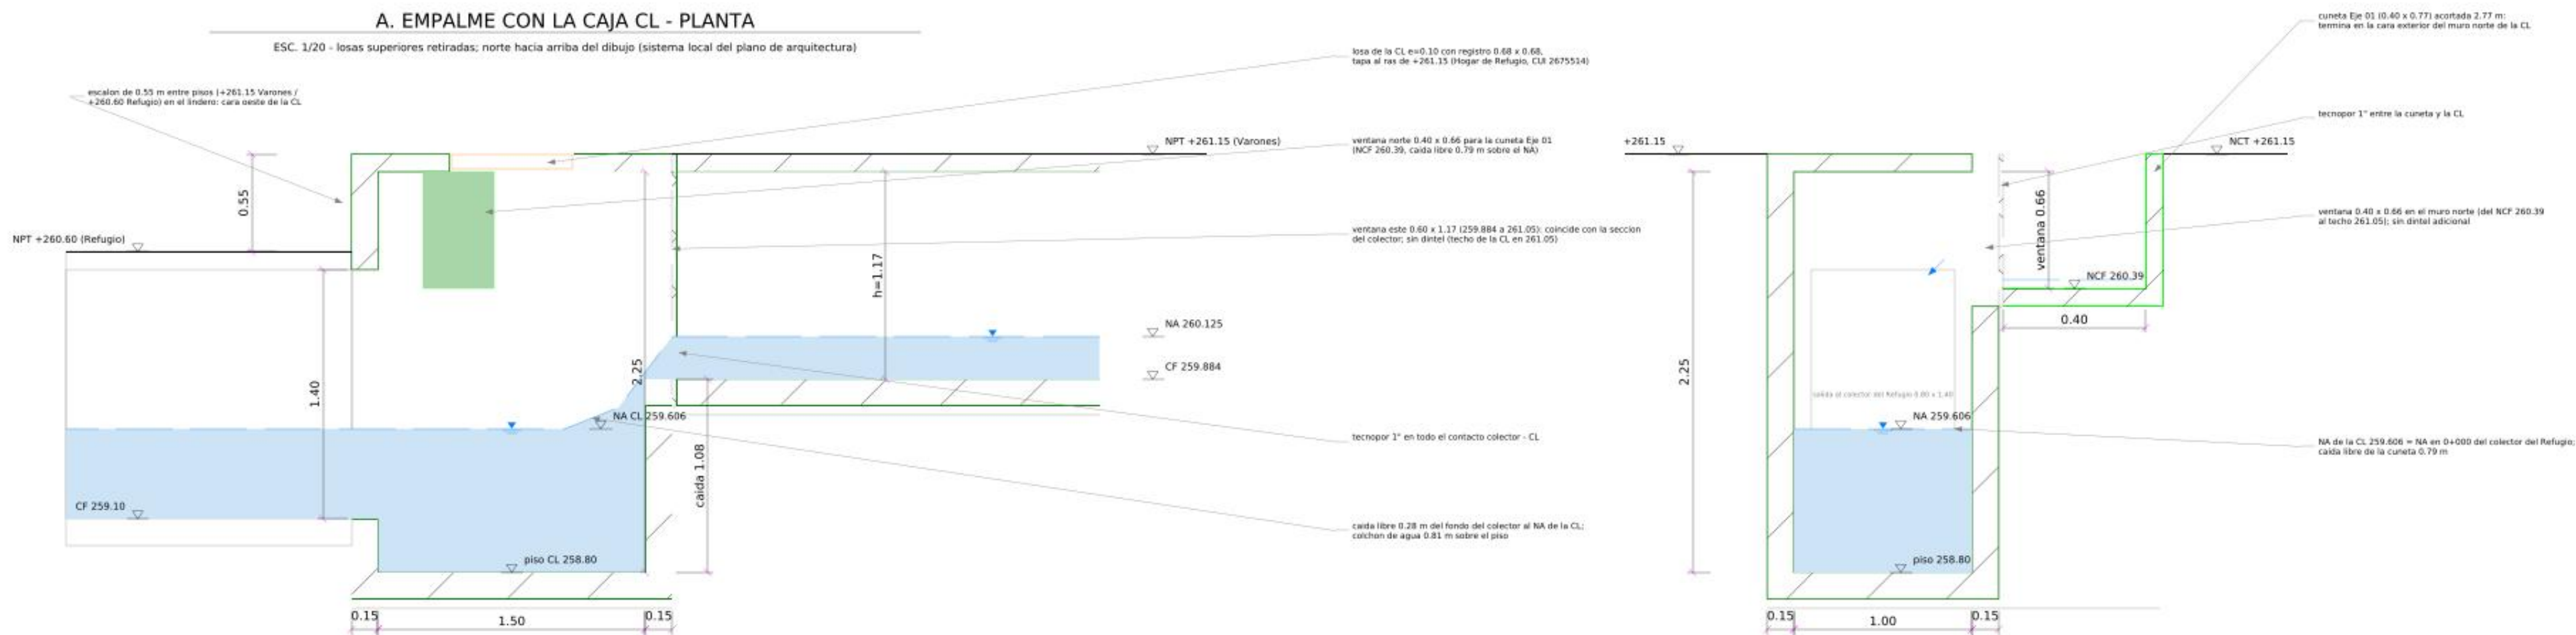

B. CORTE A-A POR EL EJE (MIRANDO AL NORTE)

ESC. 1/20 - colector CAR Varones (derecha) -> caja CL -> colector del Hogar de Refugio (izquierda, referencia)

C. CORTE B-B POR LA CAJA CL (MIRANDO AL OESTE)

ESC. 1/20

PROYECTO:
CREACIÓN DEL SERVICIO DE PROTECCIÓN INTEGRAL A NIÑAS, NIÑOS Y ADOLESCENTES SIN CUIDADOS PARENTALES O EN RIESGO DE PERDERLOS
EN CENTRO DE ACOGIDA RESIDENCIAL - VARONES, DISTRITO DE MORALES, PROVINCIA Y DEPARTAMENTO DE SAN MARTÍN - CLJ N. 2705639
ENTIDAD: GERENCIA TERRITORIAL BAJO MAYO - TARAPOTO

UBICACION: PREDIO ALDEA INFANTIL VIRGEN DEL PILAR - MORALES - SAN MARTÍN - SAN MARTÍN
ESPECIALIDAD: INSTALACIONES SANITARIAS - DRENAJE PLUVIAL

PLANO: EMPALME DEL COLECTOR CON LA CAJA DE LLEGADA CL DEL HOGAR DE REFUGIO
PLANTA Y CORTES DEL EMPALME: VENTANA ESTE 0.60 x 1.17, VENTANA NORTE PARA LA CUNETAS EJE 01, JUNTAS Y NIVELES - ESC. 1/20

PROYECTISTA: _____ CIP: _____

ELABORADO: HIDROCONSULT _____ ESCALA: 1/20

REVISADO: _____ FECHA: OCT. 2026 LÁMINA: _____

FIRMA Y SELLO: _____ REVISION: 00

CUADRO DE DOBLADO DE ACERO

ELEMENTO	FORMA	DIAMETRO	ESPACIAM.	LONGITUD (m)	LONG. TOTAL (m)	PESO (kg)
Colector: marcos tramo normal	marco unico cerrado (eje de la seccion)	3/8"	0.20 ver figura: 2 x (0.95 + h + 0.125) + 0.30	2029.3		1136.4
Colector: marcos cruce de camiones	marco doble (exterior + interior)	1/2"	0.15 ver figura		319.6	317.7
Colector: barras longitudinales	recta con traslape 0.40	3/8"	0.25 / 0.20 continua	1910.2		1069.7
Registros: refuerzo de borde de abertura	recta	1/2"	2 por lado	1.40	123.2	122.5
Tapas de registro (incluye asas)	recta / U	3/8"	0.10	0.62 / 0.40	104.3	58.4
Anclajes de contramarco	I	3/8"	8 por registro	0.20	17.6	9.9
TOTAL						2714.6

Resumen: acero 3/8" = 2274.4 kg ; acero 1/2" = 440.2 kg ; total = 2714.6 kg (incluye traslapes y ganchos). Angulos metalicos: 166.6 kg.

ESPECIFICACIONES TECNICAS

CONCRETO ARMADO: Fc = 210 kg/cm2 (colector y tapas). Cemento tipo I; agregados limpios; slump 3" a 4".
CONCRETO SIMPLE: solado Fc = 100 kg/cm2, e = 0.05 m.
ACERO DE REFUERZO: fy = 4200 kg/cm2 (grado 60), corrugado. Ganchos de 0.30 m en los marcos.
RECUBRIMIENTOS: 0.04 m en muros y losa de fondo; 0.025 m en losa superior del tramo normal; 0.04 m en el cruce de camiones; 0.025 m en tapas.
TRASLAPES: 3/8" = 0.40 m ; 1/2" = 0.50 m, alternados. Barras longitudinales de 9.00 m.
LOSA SUPERIOR: vaciada monoliticamente con los muros en todo el colector; acabado frotachado y brunado (a nivel del piso terminado +261.15).
REGISTROS: marco y contramarco de angulo 2"x2"x3/8" y 1 1/2"x1 1/2"x1/8" con anclajes, pintura anticorrosiva y esmalte; tapas de concreto 0.68 x 0.68 x 0.08 con asas.
JUNTAS: cada 4.00 m, e = 1", relleno de poliestireno expandido y sello elastomerico de poliuretano. Tecnopor de 1" entre el colector y el cerco, las cunetas, la caja CL y el piso adyacente.
CURADO: humedo minimo 7 dias; no transitar sobre la losa antes de 14 dias; no cargar con camiones antes de 28 dias.
RELLENO: material propio seleccionado, capas de 0.15 m, 95 % del Proctor modificado; incluye la nivelacion del retiro hasta la cota de la losa.
EXCAVACION: zanja de 1.40 m de ancho (0.25 m a cada lado del muro); entibar si el suelo lo requiere (profundidades de 1.10 a 1.75 m).
EMPALME: el colector entrega a la caja de llegada CL del Hogar de Refugio Temporal (CU 2675514) por la ventana 0.60 x 1.17 de su muro este; verificar la CL antes de vaciar el ultimo tramo.
CUNETAS: las cunetas de arquitectura (Ejes 09, 08, 06 y 04) terminan en la cara del muro del colector; la del Eje 01 entra a la caja CL (ver DP-07).


GROSOR DE PLUMILLA POR COLOR (CTB)

color 94 concreto (cortes y contornos) 0.40 mm
color 1 acero transversal (marcos) 0.30 mm
color 5 acero longitudinal y progresivas 0.30 mm
color 32 registros y marcos metalicos 0.30 mm
color 6 cotas, cortes y linderos 0.18 mm
color 14 cerco perimetrico 0.30 mm
color 7 textos, titulos, piso terminado 0.25 mm
color 3 cunetas 0.25 mm
color 30 tapas y cruces vehiculares 0.18 mm
color 34 poza y umbral 0.18 mm
color 150 agua y flujo 0.13 mm
color 8 achurados, auxiliares y anq. base 0.09 mm
color 9 grillas 0.05 mm
caras de isometricos y agua: color verdadero (RGB), plumilla 0.05 mm



MARCO UNICO 3/8" (tramo normal @0.20, motos @0.15)

un marco cerrado en el eje de muros y losas: 0.75 x (h + 0.125); gancho de 0.30 m; una capa (E.060 14.3.4)

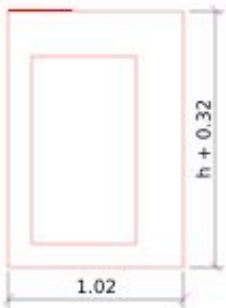


MARCO DOBLE 1/2" @0.15 (cruce de camiones)

marco exterior 1.02 x (h + 0.32) y marco interior 0.80 + 0.22 x (h + 0.08); una capa en cada cara; losa superior e=0.25

NOTAS GENERALES


- Dimensiones en metros y cotas en m.s.n.m., salvo indicacion.
- El colector conduce 221.7 L/s (cunetas Ejes 09, 08, 06 y 04); con la cuneta del Eje 01, que entra directamente a la CL, el CAR Varones entrega 258.7 L/s (TR 25 anos), igual a lo considerado en el expediente del Hogar de Refugio.
- Verificaciones hidraulica y estructural segun memoria de calculo del proyecto (RNE CE.040, E.020, E.060; AASHTO LRFD HL-93 en el cruce de camiones).
- Las cunetas de arquitectura (Ejes 01 a 09) y sus cotas de fondo son datos del plano PERFIL CAR VARONES; las de los Ejes 09, 08, 06, 04 y 01 llegan al frente.
- Confirmar la capacidad portante con el estudio de mecanica de suelos antes del vaciado.

PROYECTO: CREACION DEL SERVICIO DE PROTECCION INTEGRAL A NIÑAS, NIÑOS Y ADOLESCENTES SIN CUIDADOS PARENTALES O EN RIESGO DE PERDERLOS EN CENTRO DE ACOGIDA RESIDENCIAL - VARONES, DISTRITO DE MORALES, PROVINCIA Y DEPARTAMENTO DE SAN MARTIN - CLJ N. 2705639 ENTIDAD: GERENCIA TERRITORIAL BAJO MAYO - TARIAPOTO		
UBICACION: PREDIO ALDEA INFANTIL VIRGEN DEL PILAR - MORALES - SAN MARTIN - SAN MARTIN ESPECIALIDAD: INSTALACIONES SANITARIAS - DRENAJE PLUVIAL		
PLANO: CUADROS DE ACERO, ESPECIFICACIONES TECNICAS Y NOTAS CUADRO DE DOBLADO Y RESUMEN DE ACERO, ESPECIFICACIONES DE MATERIALES Y GROSORES DE IMPRESION		
PROYECTISTA: _____ CIP: _____		
ELABORADO: HIDROCONSULT	ESCALA: 1/25	
REVISADO: _____	FECHA: OCT. 2026	LAMINA:
FIRMA Y SELLO:	REVISION: 00	DP-08

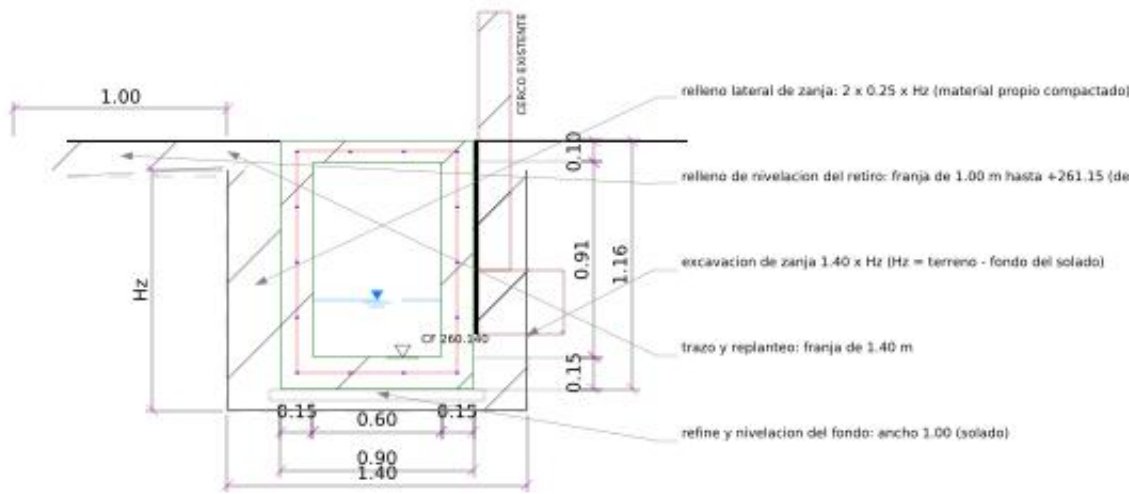


ZANJA TIPICA - TRAMO NORMAL

PROG. 0+020.00 - ESC. 1/25

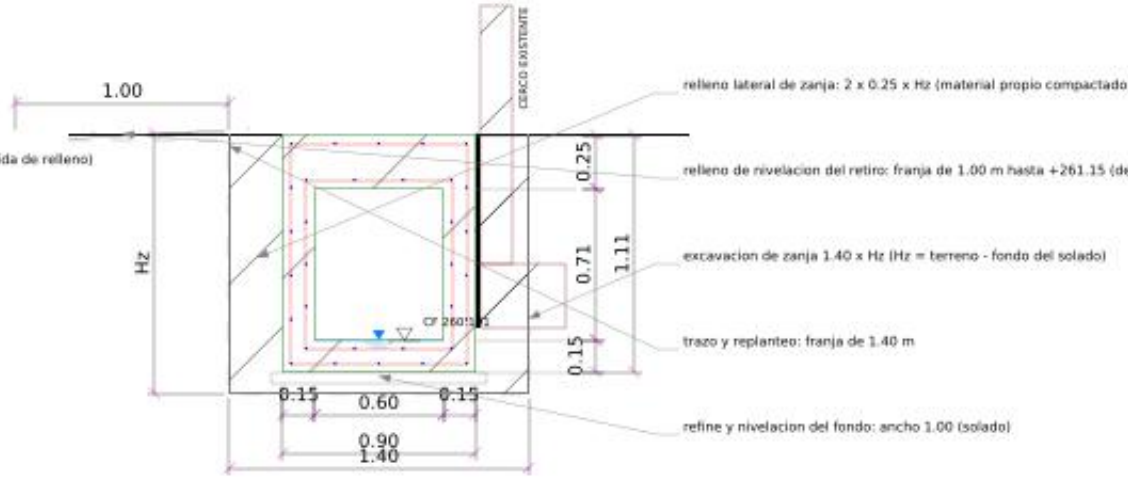

ZANJA - CRUCE DE CAMIONES

PROG. 0+003.00 - ESC. 1/25

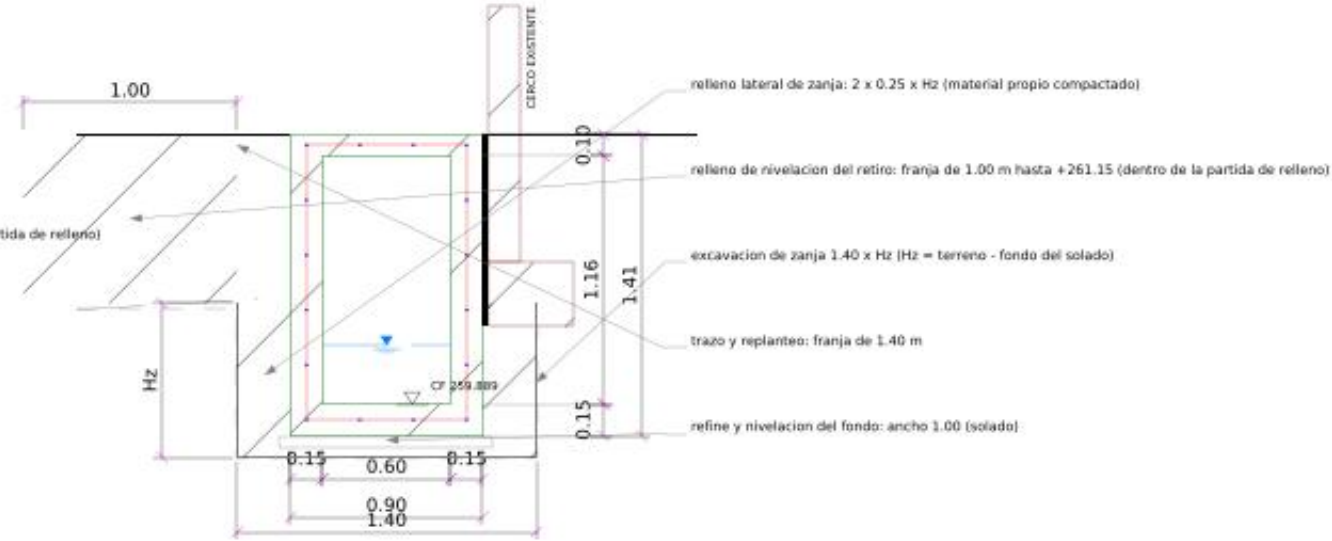

ZANJA - TRAMO DE EMPALME CON LA CL

PROG. 0+103.50 - ESC. 1/25


RESUMEN DE MOVIMIENTO DE TIERRAS

PARTIDA	UND	METRADO	CRITERIO
Trazo, niveles y replanteo	m2	147.41	franja de 1.40 m x L
Excavacion de zanja	m3	130.68	1.40 x Hz x L por tramo (Hz desde el terreno existente)
Refine y nivelacion de fondo	m2	105.29	1.00 x L
Relleno compactado con material propio	m3	91.49	relleno lateral de zanja + franja de nivelacion del retiro (1.00 m)
Eliminacion de material excedente	m3	47.03	(excavacion - relleno) x 1.25

NOTAS


- Hz varia con el terreno existente (superficie topografica) y la cota de fondo del colector; ver tabla de tramos en la planilla de metrados.
- Criterio: los rellenos menores (nivelacion de la franja adyacente) van dentro de la partida de relleno, no como partida aparte.
- Donde el terreno existente queda por debajo de la losa, el muro lado via se vacia con encofrado exterior y luego se rellena.

PROYECTO: CREACION DEL SERVICIO DE PROTECCION INTEGRAL A NIÑAS, NIÑOS Y ADOLESCENTES SIN CUIDADOS PARENTALES O EN RIESGO DE PERDERLOS EN CENTRO DE ACOGIDA RESIDENCIAL - VARONES, DISTRITO DE MORALES, PROVINCIA Y DEPARTAMENTO DE SAN MARTIN - CLJ N. 2705639 ENTIDAD: GERENCIA TERRITORIAL BAJO MAYO - TARIAPOTO		
UBICACION: PREDIO ALDEA INFANTIL VIRGEN DEL PILAR - MORALES - SAN MARTIN - SAN MARTIN ESPECIALIDAD: INSTALACIONES SANITARIAS - DRENAJE PLUVIAL		
PLANO: DETALLE DE PARTIDAS: TRAZO, EXCAVACION, RELLENO Y ELIMINACION SECCION TIPICA DE ZANJA POR ZONA Y RESUMEN DE METRADO - ESC. 1/25		
PROYECTISTA: _____ CIP: _____		
ELABORADO: HIDROCONSULT	ESCALA: 1/25	
REVISADO: _____	FECHA: OCT. 2026	LAMINA:
FIRMA Y SELLO:	REVISION: 00	

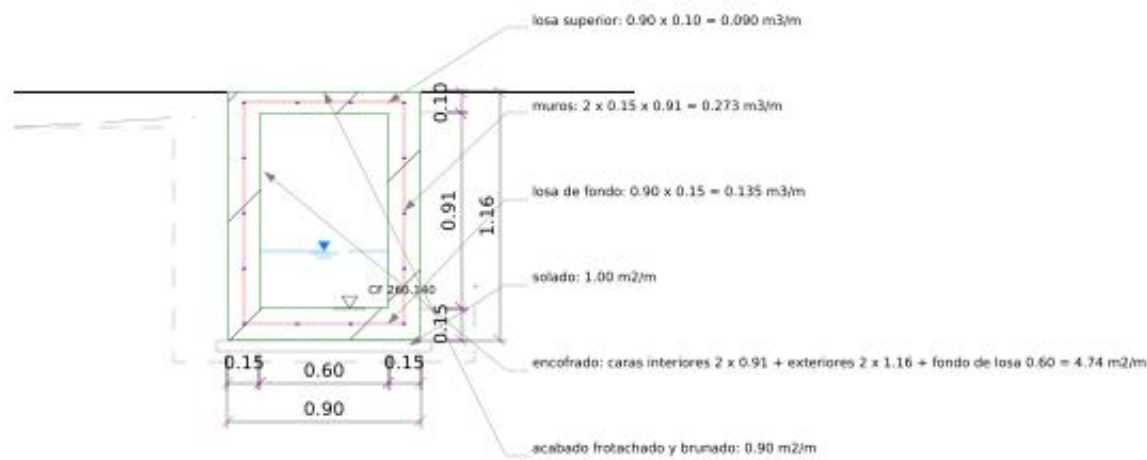


TRAMO NORMAL

PROG. 0+020.00 - h = 0.91 m - ESC. 1/25

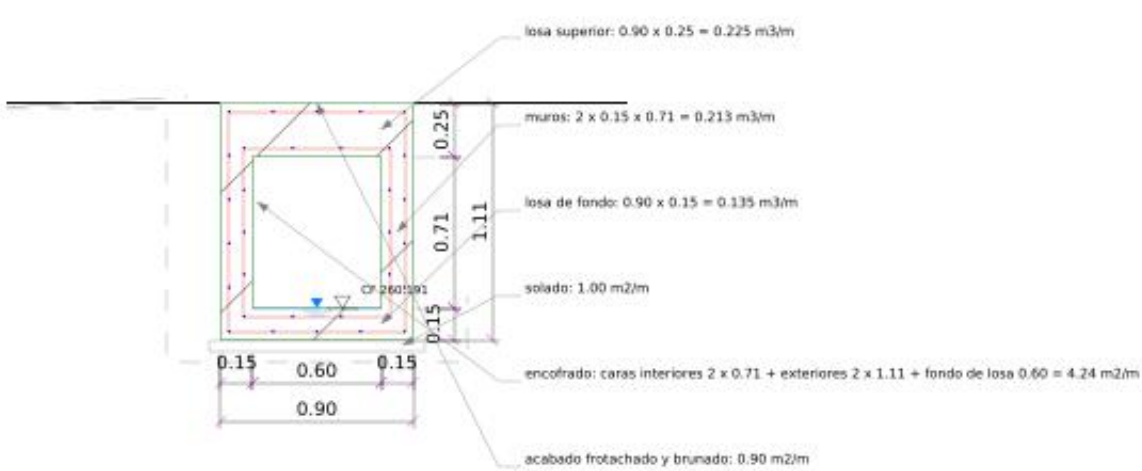

CRUCE DE CAMIONES

PROG. 0+003.00 - h = 0.71 m - ESC. 1/25

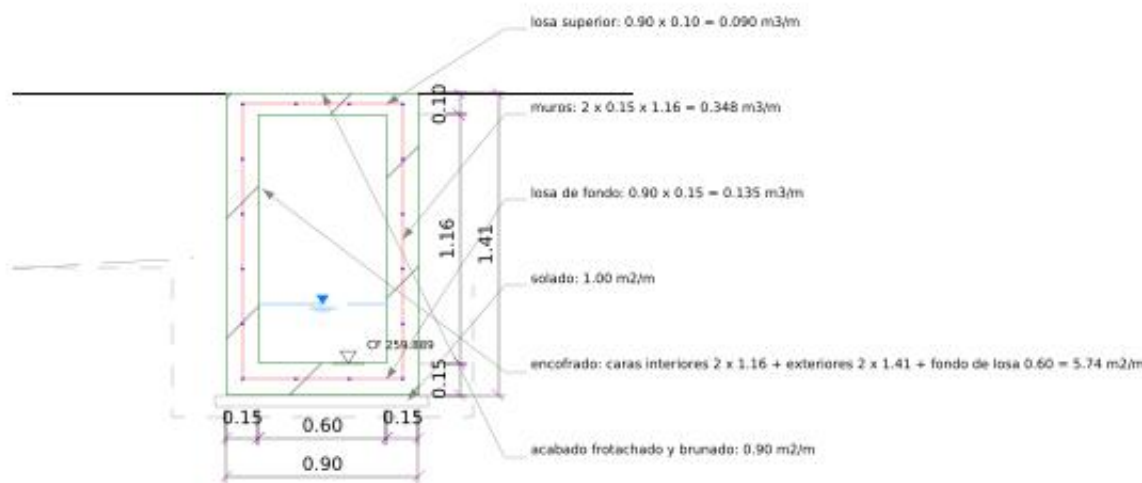


TRAMO DE EMPALME (h max.)

PROG. 0+103.50 - h = 1.16 m - ESC. 1/25

RESUMEN DE CONCRETO Y ENCOFRADO (colector)


PARTIDA	UND	METRADO
Solado f'c=100 e=0.05	m2	105.29
Concreto f'c=210 - losa de fondo	m3	14.21
Concreto f'c=210 - muros	m3	31.56
Concreto f'c=210 - losa superior (incluye bordes de registro)	m3	10.25
Encofrado y desencofrado	m2	538.50
Acabado frotachado y brunado de losa superior	m2	94.76

PROYECTO: CREACIÓN DEL SERVICIO DE PROTECCIÓN INTEGRAL A NIÑAS, NIÑOS Y ADOLESCENTES SIN CUIDADOS PARENTALES O EN RIESGO DE PERDERLOS EN CENTRO DE ACOGIDA RESIDENCIAL - VARONES, DISTRITO DE MORALES, PROVINCIA Y DEPARTAMENTO DE SAN MARTÍN - CLJ N. 2705639 ENTIDAD: GERENCIA TERRITORIAL BAJO MAYO - TARIAPOTO		
UBICACION: PREDIO ALDEA INFANTIL VIRGEN DEL PILAR - MORALES - SAN MARTIN - SAN MARTIN ESPECIALIDAD: INSTALACIONES SANITARIAS - DRENAJE PLUVIAL		
PLANO: DETALLE DE PARTIDAS: SOLADO, CONCRETO ARMADO Y ENCOFRADO ÁREAS Y VOLUMENES POR METRO LINEAL EN CADA ZONA - ESC. 1/25		
PROYECTISTA: _____ CIP: _____		
ELABORADO: HIDROCONSULT	ESCALA: 1/25	
REVISADO: _____	FECHA: OCT. 2026	LÁMINA:
FIRMA Y SELLO:	REVISION: 00	

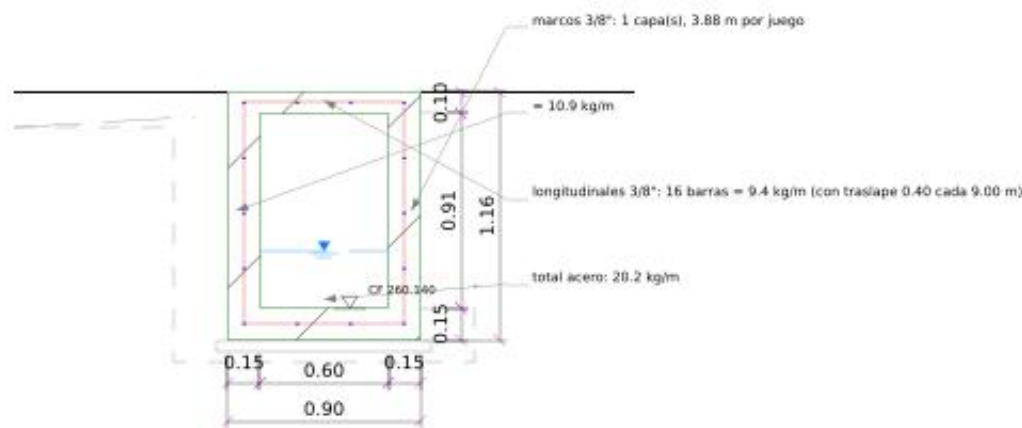


TRAMO NORMAL 3/8" @0.20

PROG. 0+020.00 - ESC. 1/25

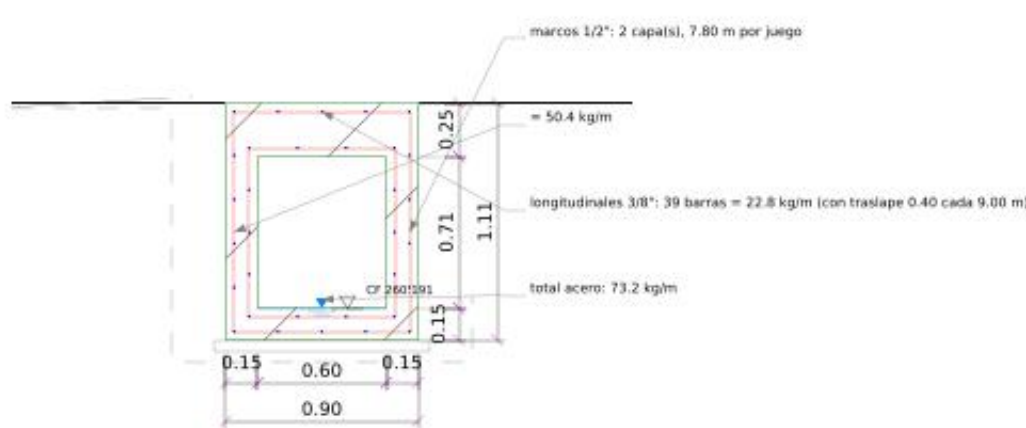

CRUCE DE CAMIONES 1/2" @0.15 DOBLE

PROG. 0+003.00 - ESC. 1/25

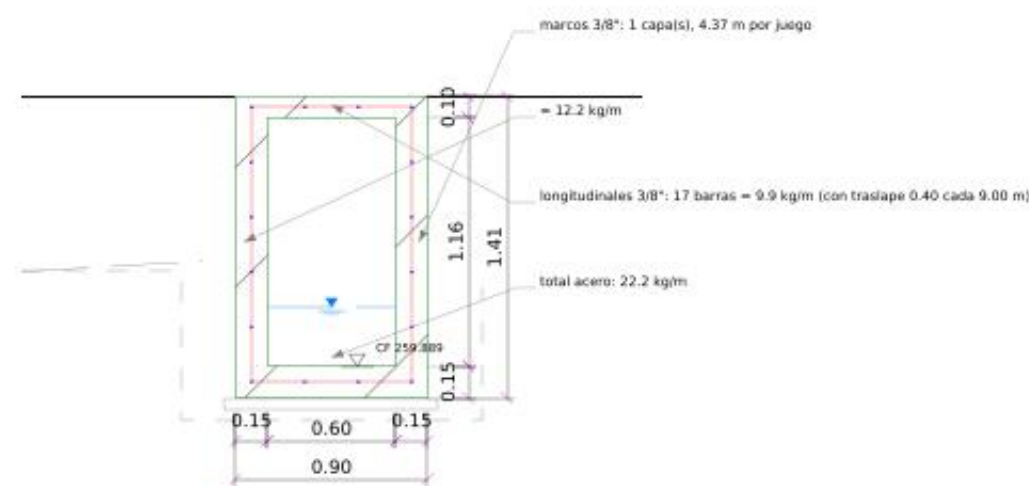

TRAMO DE EMPALME 3/8" @0.20

PROG. 0+103.50 - ESC. 1/25

RESUMEN DE ACERO, REGISTROS, JUNTAS Y EMPALMES

PARTIDA	UND	METRADO
Acero fy=4200 colector - 3/8"	kg	2206.1
Acero fy=4200 colector - 1/2" (cruce de camiones)	kg	317.7
Registros: contramarco L 2'x2'x3/16" (11 und)	kg	111.8
Registros: marco de tapa L 1 1/2"x1 1/2"x1/8"	kg	94.8
Tapas de concreto 0.68 x 0.68 x 0.08	und / m3	11 / 0.41
Acero en tapas, bordes, asas y anclajes	kg	190.7
Pintura anticorrosiva y esmalte en angulos	m2	10.80
Junta de dilatacion e=1" con sello (26 und x 4.63 m)	m	120.43
Junta de tecnopor e=1" con el cerco (muro)	m	103.73
Junta de tecnopor e=1" con el piso adyacente	m	211.88
Empalme de cuneta al colector (ventana + caída)	und	5

PROYECTO:
CREACIÓN DEL SERVICIO DE PROTECCIÓN INTEGRAL A NIÑAS, NIÑOS Y ADOLESCENTES SIN CUIDADOS PARENTALES O EN RIESGO DE PERDERLOS
EN CENTRO DE ACOGIDA RESIDENCIAL - VARONES, DISTRITO DE MORALES, PROVINCIA Y DEPARTAMENTO DE SAN MARTÍN - CLJ N. 2705639
ENTIDAD: GERENCIA TERRITORIAL BAJO MAYO - TARIAPOTO

UBICACION: PREDIO ALDEA INFANTIL VIRGEN DEL PILAR - MORALES - SAN MARTIN - SAN MARTIN
ESPECIALIDAD: INSTALACIONES SANITARIAS - DRENAJE PLUVIAL


PLANO: DETALLE DE PARTIDAS: ACERO, REGISTROS, JUNTAS Y EMPALMES
DESPIECE POR METRO, INSUMOS POR REGISTRO Y LONGITUDES DE JUNTA - ESC. 1/25

PROYECTISTA: _____ CIP: _____

ELABORADO: HIDROCONSULT ESCALA: 1/25

REVISADO: _____ FECHA: OCT. 2026 LAMINA:

FIRMA Y SELLO: _____ REVISION: 00

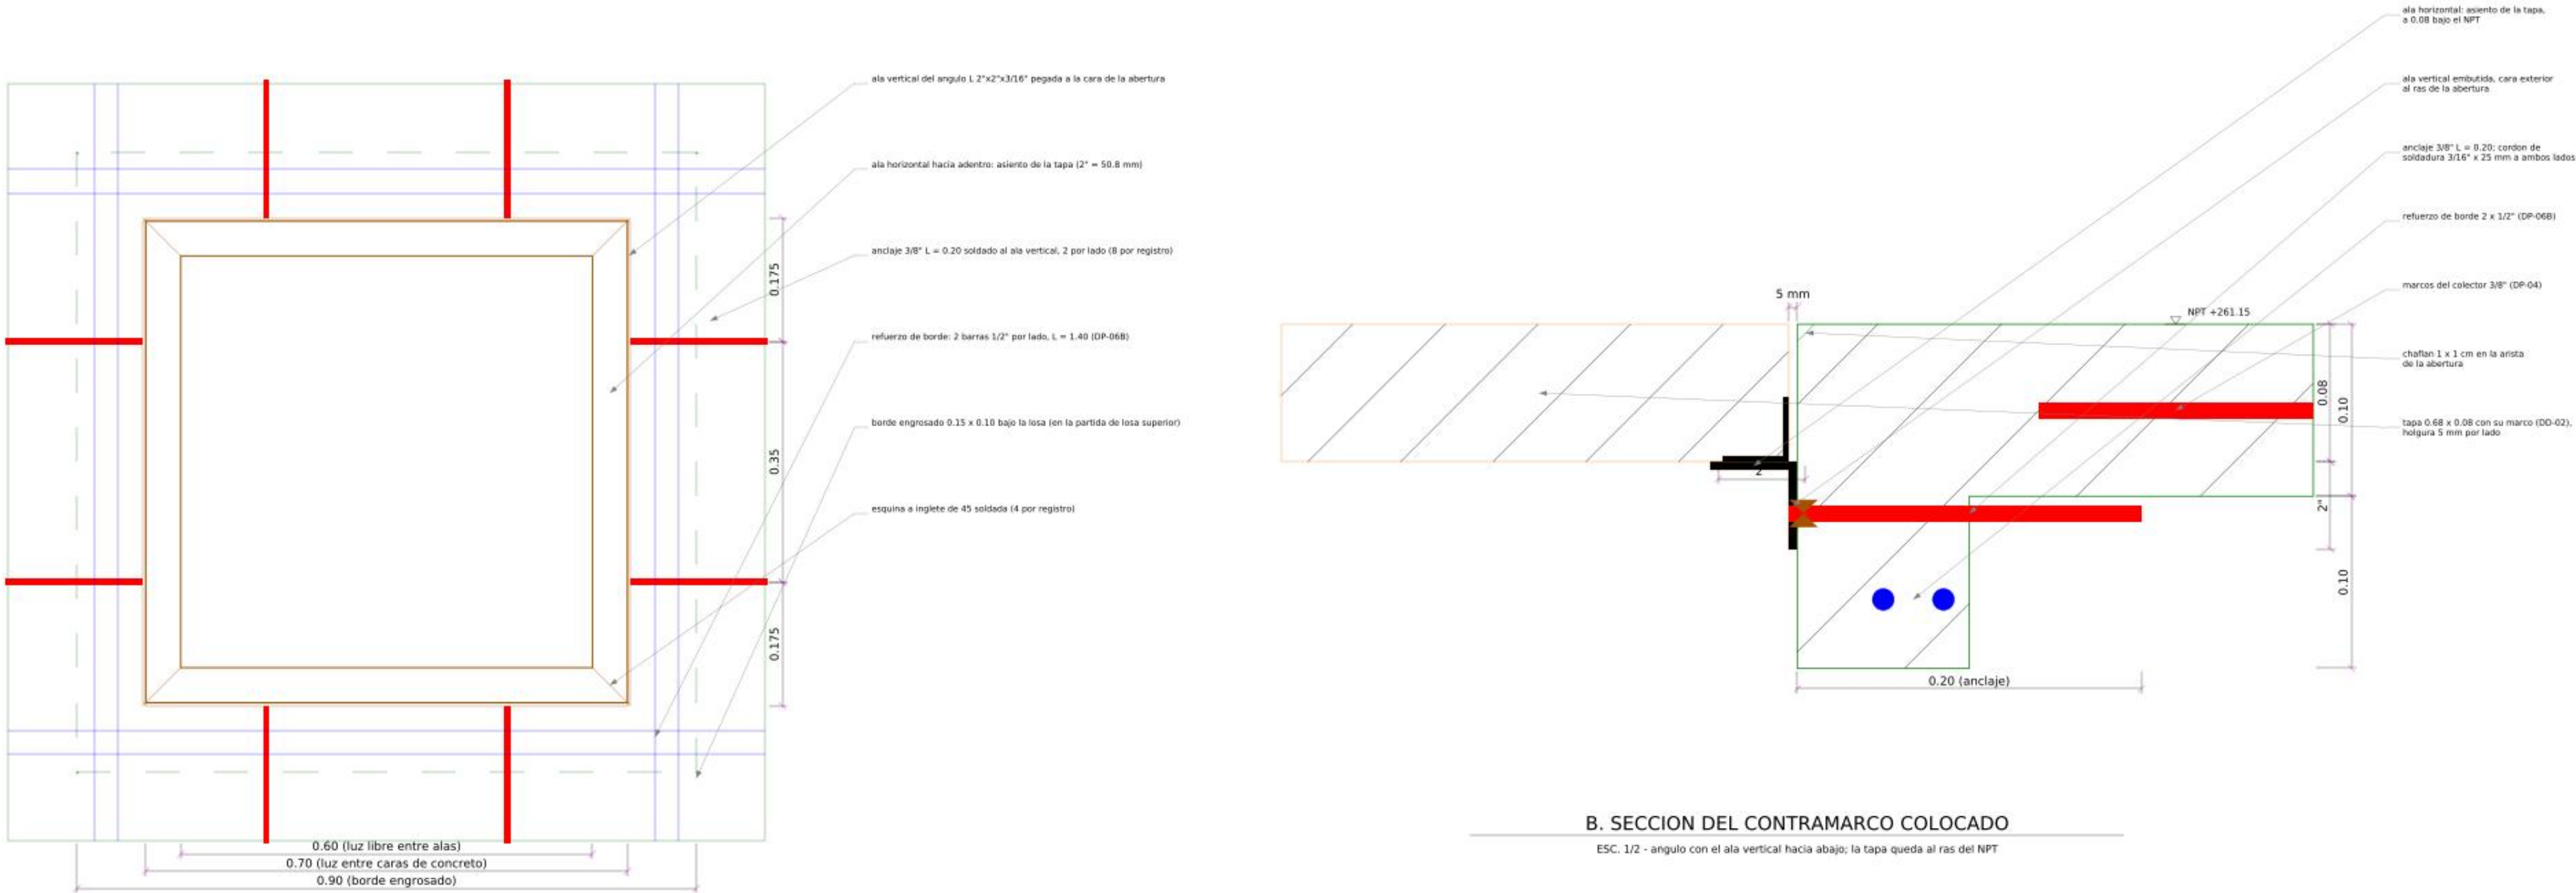


A. CONTRAMARCO - PLANTA

ESC. 1/5 - 1 por registro: 11 en la losa del colector (RV-01 a RV-11)

B. SECCION DEL CONTRAMARCO COLOCADO

ESC. 1/2 - angulo con el ala vertical hacia abajo; la tapa queda al ras del NPT

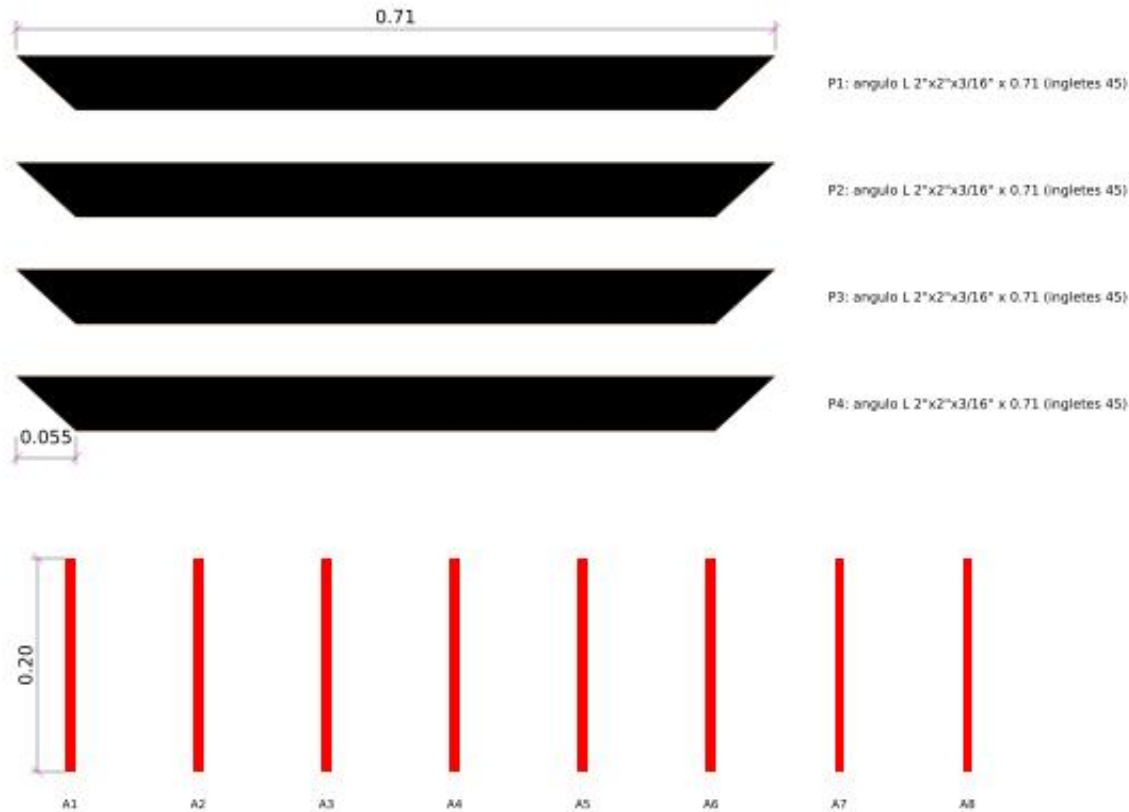

C. DESPIECE DEL CONTRAMARCO

ESC. 1/5 - 4 angulos + 8 anclajes por registro

PROCEDIMIENTO

1. Cortar 4 piezas de angulo L 2"x2"x3/16" de 0.71 m con los extremos a inglete de 45 y armar el cuadro de 0.70 x 0.70 (medida exterior de las alas verticales).
2. Soldar las 4 esquinas con electrodo E6011 de 1/8" (cordon 3/16" por ambas caras); verificar escuadra (diagonales iguales) y planitud.
3. Soldar 8 anclajes 3/8" L = 0.20 al ala vertical (2 por lado, a 0.175 de las esquinas), cordon 3/16" x 25 mm a ambos lados.
4. Limpiar escoria; 2 manos de anticorrosivo epoxico y 2 de esmalte sintetico (partida 01.04.04.05.07), salvo en la zona de los anclajes.
5. Fijar el contramarco al encofrado de la losa con el asiento a 0.08 bajo el NPT, nivelado y amarrado al refuerzo de borde; vaciar la losa con el borde engrosado.
6. Al desencofrar, retirar rebabas; la tapa con su marco debe asentar en las 4 alas con holgura de 5 mm por lado.


CUADRO DE COMPONENTES POR CONTRAMARCO (1 und) Y TOTAL (11 und)

COMPONENTE	UND	CANT. / UND	x TOTAL	PARTIDA / OBSERVACION
Angulo L 2"x2"x3/16" (4 piezas de 0.71 m, 3.63 kg/m)	m / kg	2.84 / 10.30	31.22 / 113.33	01.04.04.05.03 ANGULOS METALICOS (kg)
Anclajes 3/8" corrugado L = 0.20 (8 und, 0.56 kg/m)	m / kg	1.60 / 0.90	17.60 / 9.86	01.04.04.05.06 ACERO EN TAPAS, BORDES Y ANCLAJES
Cordon de soldadura 3/16" (4 esquinas x 2 caras + 8 anclajes x 2 lados)	m	0.81	8.87	electrodo E6011 1/8": aprox. 0.12 kg por registro
Refuerzo de borde de la abertura 2 x 1/2" por lado, L = 1.40 (8 barras)	m / kg	11.20 / 11.13	123.20 / 122.46	01.04.04.05.06 (ver DP-06B)
Borde engrosado 0.15 x 0.10, perimetro medio 3.00 m	m3	0.045	0.49	01.04.04.04.03 LOSA SUPERIOR (ya incluido)
Pintura anticorrosiva + esmalte (desarrollo 0.203 m2/m x 2.80 m)	m2	0.57	6.25	01.04.04.05.07 PINTURA (parte)
Mano de obra de habilitacion, soldadura y colocacion	und	1	11	01.04.04.05.01 CONTRAMARCO (und)


LEYENDA

- angulo metalico
- anclaje 3/8"
- refuerzo de borde 1/2" (proyeccion)
- concreto f'c=210
- tapa (referencia, ver DD-02)


PROYECTO: CREACION DEL SERVICIO DE PROTECCION INTEGRAL A NIÑAS, NIÑOS Y ADOLESCENTES SIN CUIDADOS PARENTALES O EN RIESGO DE PERDERLOS EN CENTRO DE ACOGIDA RESIDENCIAL - VARONES, DISTRITO DE MORALES, PROVINCIA Y DEPARTAMENTO DE SAN MARTIN - CLJ N. 2705639 ENTIDAD: GERENCIA TERRITORIAL BAJO MAYO - TARAPOTO		
UBICACION: PREDIO ALDEA INFANTIL VIRGEN DEL PILAR - MORALES - SAN MARTIN - SAN MARTIN ESPECIALIDAD: INSTALACIONES SANITARIAS - DRENAJE PLUVIAL		
PLANO: DETALLE CONSTRUCTIVO: CONTRAMARCO METALICO L 2"x2"x3/16" CON ANCLAJES PARTIDAS 01.04.04.05.01, 01.04.04.05.03 (parte) y 01.04.04.05.06 (parte) - 10 REGISTROS - ESC. INDICADAS		
PROYECTISTA: _____ CIP: _____		
ELABORADO: HIDROCONSULT	ESCALA: 1/10	
REVISADO: _____	FECHA: OCT. 2026	LAMINA: _____
FIRMA Y SELLO: _____	REVISION: 00	DD-01

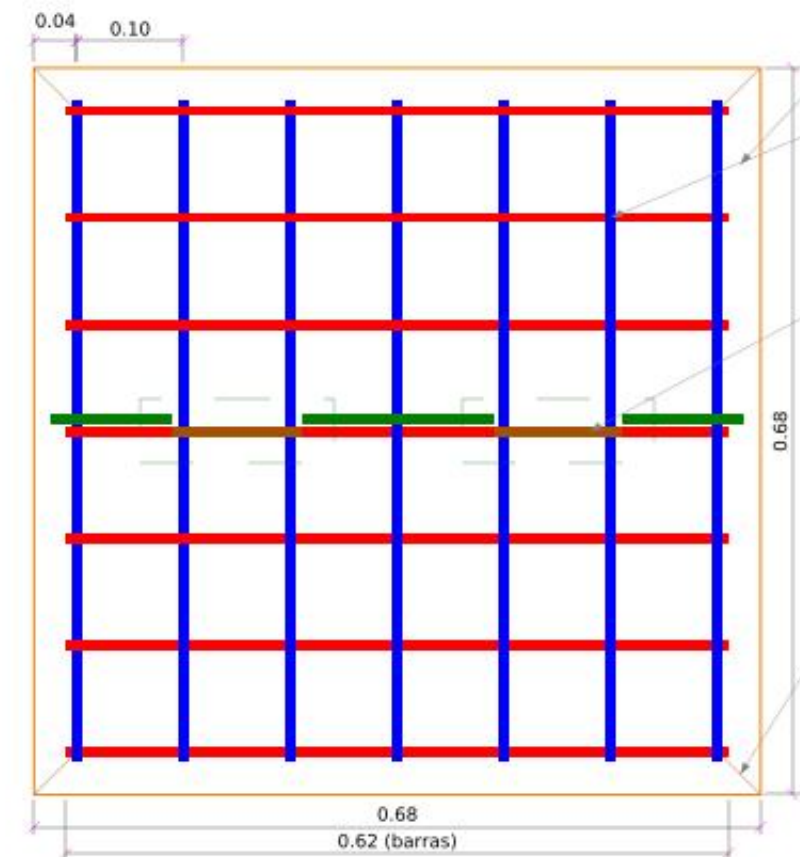


A. TAPA DE CONCRETO ARMADO - PLANTA (armado)
ESC. 1/5 - 11 und (RV-01 a RV-11)

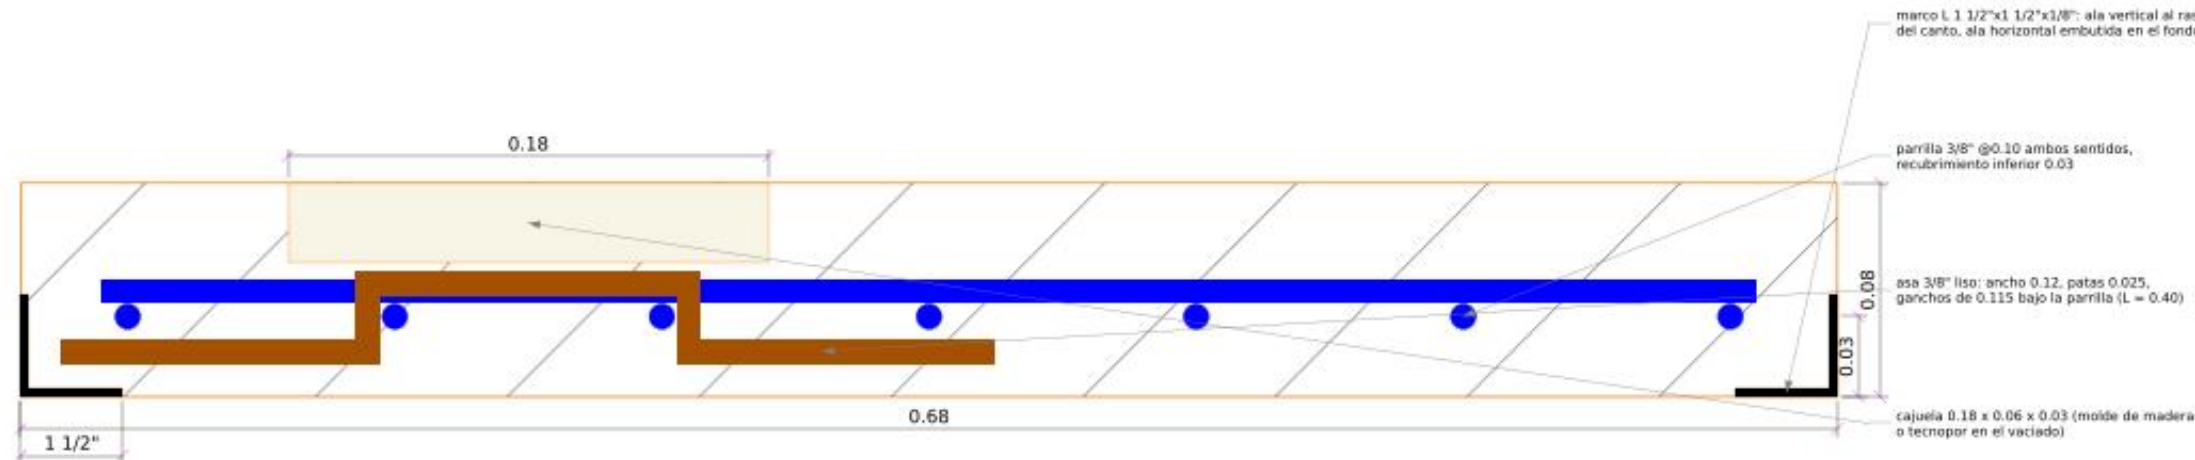

B. TAPA - CORTE
ESC. 1/2

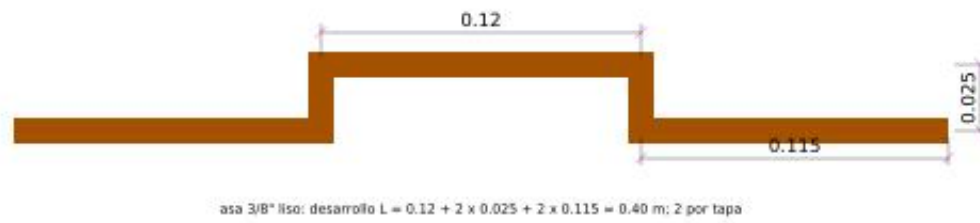

C. ASA DE IZAJE
ESC. 1/2

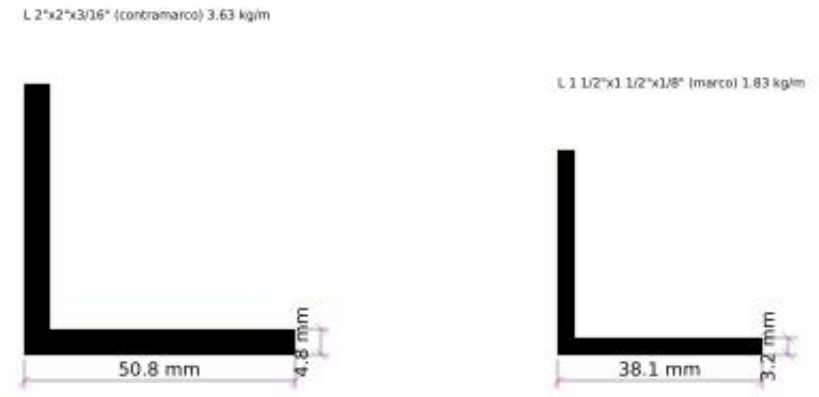

D. SECCIONES DE LOS ANGULOS
ESC. 1/1

PROCEDIMIENTO DE FABRICACION


1. Marco: 4 piezas de angulo L 1 1/2"x1 1/2"x1/8" de 0.68 m a inglete 45, soldadas en las esquinas (E6011 1/8"); medida exterior 0.68 x 0.68.
2. Parrilla: 7 + 7 barras 3/8" de 0.62 m @0.10, amarradas con alambre N 16 y soldadas por puntos en sus extremos al ala vertical del marco (28 puntos).
3. Asas: 2 barras lisas 3/8" en U (0.12 x 0.025, ganchos 0.115) amarradas bajo la parrilla; cajuela de 0.18 x 0.06 x 0.03 con molde para que no sobresalgan.
4. Vaciado en molde metalico o de madera sobre superficie plana, con el marco como encofrado lateral: concreto f'c = 210 kg/cm2; piedra de 1/2", vibrado.
5. Curado humedo 7 dias; desmoldar a los 2 dias. Acabado superior frotachado. Pintar el marco con 2 manos de anticorrosivo y 2 de esmalte.
6. Colocar sobre el contramarco (DD-01); holgura 5 mm por lado; la tapa queda al ras del NPT. Marcar el numero de registro en la tapa.

CUADRO DE COMPONENTES POR TAPA CON MARCO (1 und) Y TOTAL (11 und)

COMPONENTE	UND.	CANT. / UND	x TOTAL	PARTIDA / OBSERVACION
Concreto f'c = 210 kg/cm2 (0.68 x 0.68 x 0.08)	m3	0.037	0.41	01.04.04.05.05 CONCRETO EN TAPAS
Parrilla 3/8" corrugado, 14 barras de 0.62 m	m / kg	8.68 / 4.86	95.48 / 53.47	01.04.04.05.06 ACERO EN TAPAS, BORDES Y ANCLAJES
Asas 3/8" liso, 2 und de 0.40 m	m / kg	0.80 / 0.45	8.80 / 4.93	01.04.04.05.06
Angulo L 1 1/2"x1 1/2"x1/8" (4 piezas de 0.68 m, 1.83 kg/m)	m / kg	2.72 / 4.98	29.92 / 54.75	01.04.04.05.03 ANGULOS METALICOS (kg)
Alambre negro N 16 (amarries) / soldadura por puntos (28)	kg	0.10 / 0.05	1.10 / 0.55	Insumo del ACU
Molde: fondo 0.68 x 0.68 + cajuelas (reutilizable 10 veces)	m2	0.46	0.46	Insumo del ACU (1 molde)
Pintura anticorrosiva + esmalte del marco (0.152 m2/m x 2.72 m)	m2	0.41	4.55	01.04.04.05.07 PINTURA (parte)
Pintura total por registro: contramarco 0.57 + marco 0.41	m2	0.98	10.80	01.04.04.05.07 PINTURA (total)
Fabricacion, curado y colocacion de la tapa.	und	1	11	01.04.04.05.04 TAPA (und); marco: 01.04.04.05.02 (und)


LEYENDA

- angulo metalico / asa
- barra 3/8" (sentido X)
- barra 3/8" (sentido Y)
- concreto f'c=210 de la tapa
- cajuela del asa

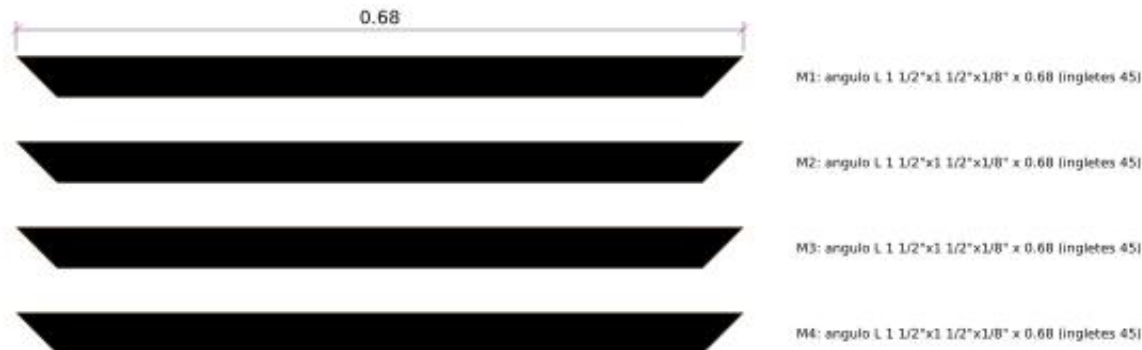

E. DESPIECE DEL MARCO Y DE LA PARRILLA
ESC. 1/5 (barras acortadas en el dibujo)

PROYECTO: CREACION DEL SERVICIO DE PROTECCION INTEGRAL A NIÑAS, NIÑOS Y ADOLESCENTES SIN CUIDADOS PARENTALES O EN RIESGO DE PERDERLOS EN CENTRO DE ACOGIDA RESIDENCIAL - VARONES, DISTRITO DE MORALES, PROVINCIA Y DEPARTAMENTO DE SAN MARTIN - CUS N. 2705639		
ENTIDAD: GERENCIA TERRITORIAL BAJO MAYO - TARAPOTO		
UBICACION: PREDIO ALDEA INFANTIL VIRGEN DEL PILAR - MORALES - SAN MARTIN - SAN MARTIN		
ESPECIALIDAD: INSTALACIONES SANITARIAS - DRENAJE PLUVIAL		
PLANO: DETALLE CONSTRUCTIVO: MARCO METALICO L 1 1/2"x1 1/2"x1/8" Y TAPA DE CONCRETO ARMADO 0.68 x 0.68		
PARTIDAS 01.04.04.05.02, .05.03 (parte), .05.04, .05.05, .05.06 (parte) y .05.07 - 10 TAPAS - ESC. INDICADAS		
PROYECTISTA: _____	CIP: _____	
ELABORADO: HIDROCONSULT	ESCALA: 1/10	
REVISADO: _____	FECHA: OCT. 2026	LAMINA:
FIRMA Y SELLO:	REVISION: 00	

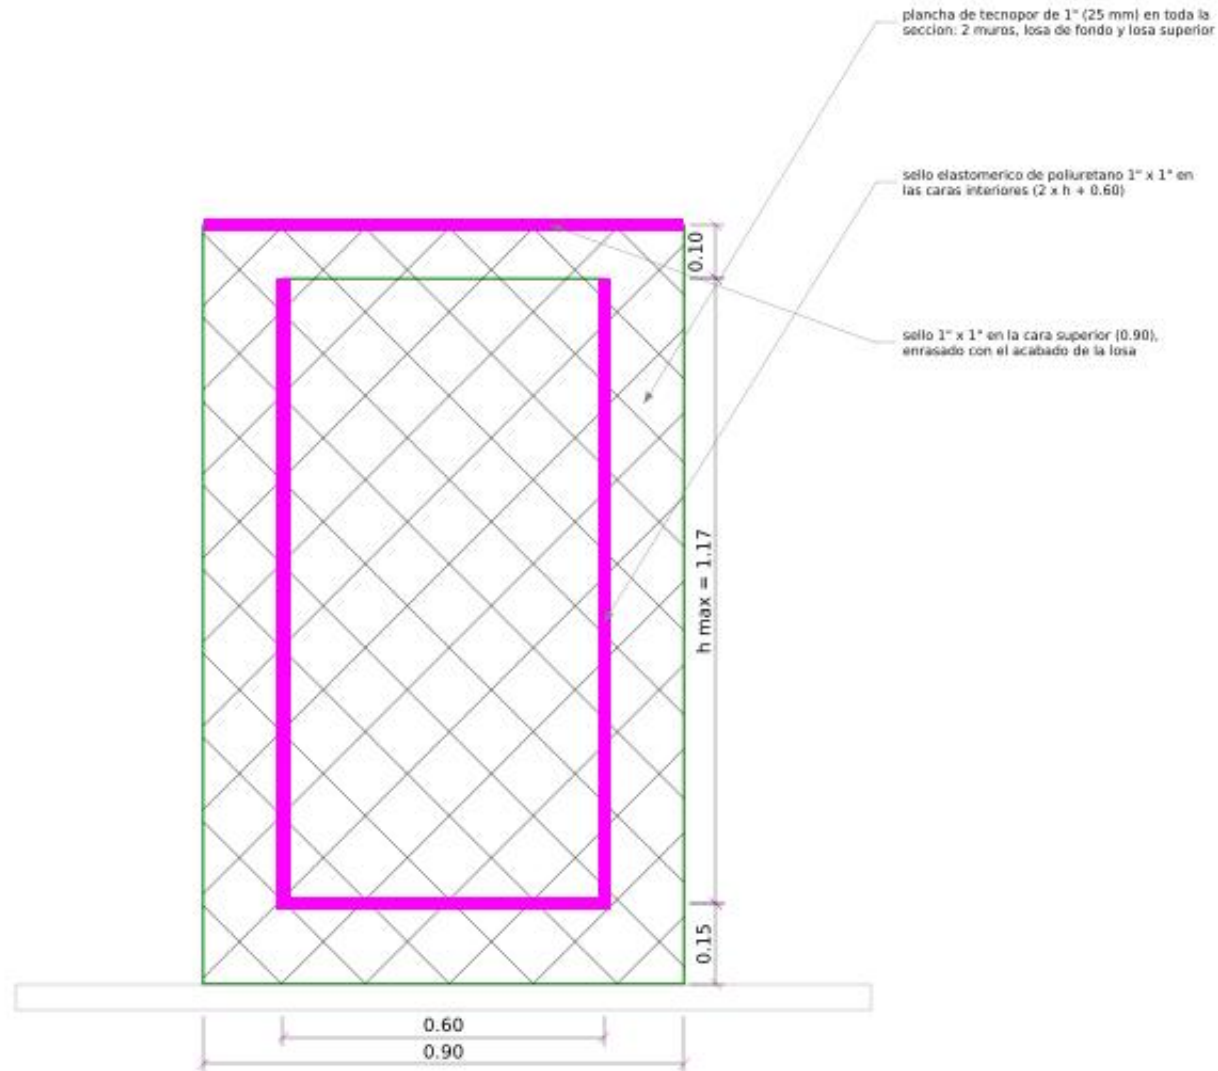


A. JUNTA DE DILATACION - SECCION TRANSVERSAL

ESC. 1/10 - perimetro = $2 \times 0.90 + 2 \times (0.15 + h + 0.10) = 4.63 \text{ m}$ (h = 1.17)


LEYENDA

- concreto $f_c=210$
- tecnopor 1"
- sello elastomerico
- cercos existentes
- barra longitudinal 3/8"
- relleno compactado

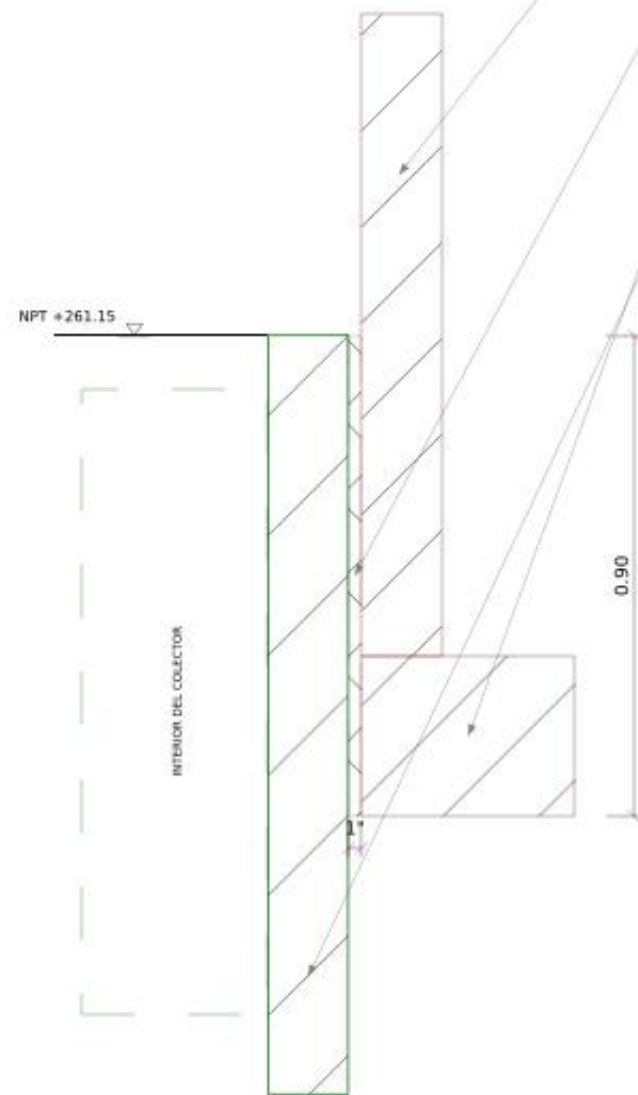


C. JUNTA DE TECNOPOR CONTRA EL CERCO

ESC. 1/10 - tramo 0+000.00 a 0+100.90 (pegado al cerco)

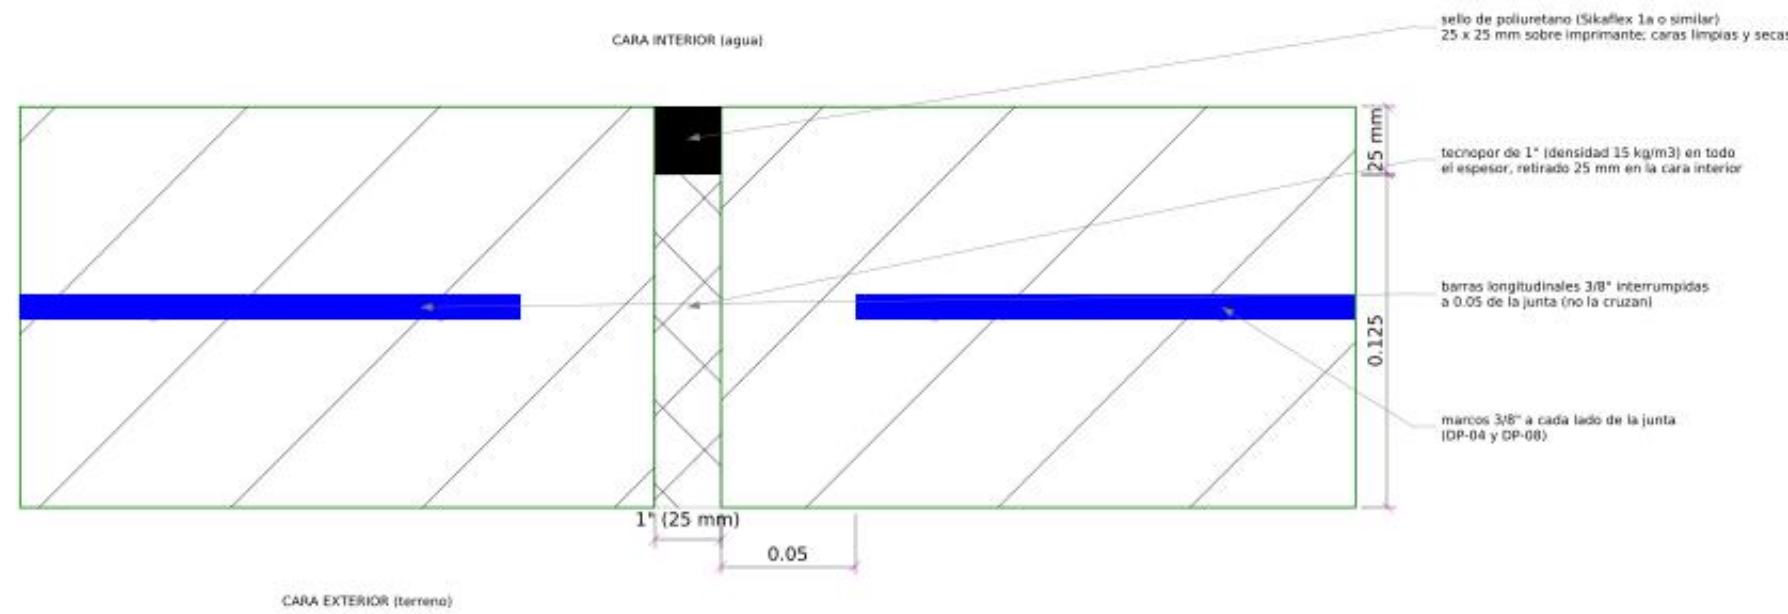

B. DETALLE DE LA JUNTA DE DILATACION

ESC. 1/2 - corte longitudinal por el muro (igual en las losas)

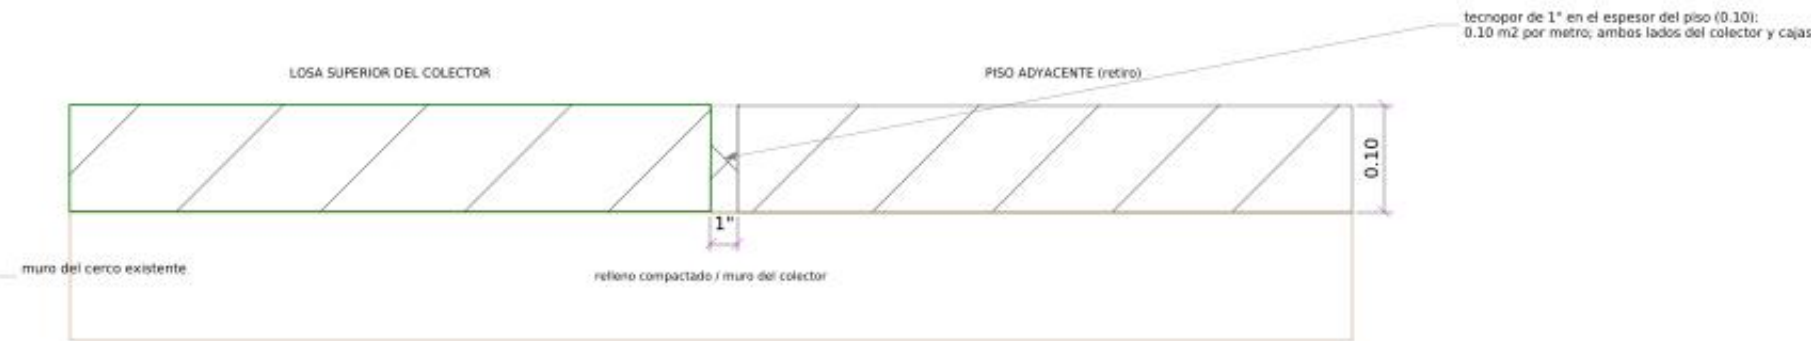

D. JUNTA DE TECNOPOR EN EL BORDE DE LA LOSA

ESC. 1/5

PROCEDIMIENTO

- Marcar las juntas cada 4.00 m (cuadro). Cortar la plancha de tecnopor a la forma de la seccion (aviso 0.90 x 1.42 con hueco 0.60 x h) y fijarla al concreto ya vaciado.
- Vaciar el tramo siguiente contra la plancha. El acero longitudinal termina a 0.05 de cada lado; los marcos se colocan a cada lado de la junta.
- Retirar 25 mm de tecnopor en las caras interiores y en la cara superior; limpiar, imprimir y aplicar el sello de poliuretano 25 x 25 mm con pistola; alisar.
- Juntas de tecnopor (02): plancha de 1" pegada al cimiento del cerco antes de vaciar el muro; plancha de 1" x 0.10 en el borde de la losa antes de vaciar el piso.

COMPONENTES POR JUNTA DE DILATACION (perimetro 4.63 m) Y TOTAL (26 und); JUNTAS DE TECNOPOR POR METRO


COMPONENTE	UND	CANT. / UND	x TOTAL	PARTIDA / OBSERVACION
Plancha de tecnopor 1" (seccion 0.90 x 1.42 menos el hueco 0.60 x 1.17)	m2	0.576 (0.124/m)	14.98	01.04.04.06.01 (por metro de junta: perimetro 4.63 m)
Sello de poliuretano 25 x 25 mm (caras interiores 2h + 0.60 y superior 0.90)	m	3.84 (0.829/m)	99.84	01.04.04.06.01: 0.63 L por metro de sello (aprox. 0.75 kg)
Imprimante para el sello (0.10 L por metro de cordón)	l	0.38	9.98	insumo del ACU
Tecnopor 1" contra el cerco: altura 0.90 x 103.73 m	m2	0.90 por m	93.36	01.04.04.06.02 (tramo pegado al cerco)
Tecnopor 1" en el borde de la losa con el piso: altura 0.10 x 231.88 m	m2	0.10 por m	23.19	01.04.04.06.02 (ambos lados del colector y cajas)

UBICACION DE LAS 26 JUNTAS (planta y perfil)

JUNTA (prog.)	JUNTA (prog.)
0+004.00	0+040.00
0+008.00	0+044.00
0+012.00	0+048.00
0+016.00	0+052.00
0+020.00	0+056.00
0+024.00	0+060.00
0+028.00	0+064.00
0+032.00	0+068.00
0+036.00	0+072.00


El colector lleva tecnopor en su contacto con la caja CL del Hogar de Refugio (muro este: 1.30 x 1.52).

PROYECTO: CREACION DEL SERVICIO DE PROTECCION INTEGRAL A NIÑAS, NIÑOS Y ADOLESCENTES SIN CUIDADOS PARENTALES O EN RIESGO DE PERDERLOS EN CENTRO DE ACOGIDA RESIDENCIAL - VARONES, DISTRITO DE MORALES, PROVINCIA Y DEPARTAMENTO DE SAN MARTIN - CUS N. 2705639 ENTIDAD: GERENCIA TERRITORIAL BAJO MAYO - TARIAPOTO		
UBICACION: PREDIO ALDEA INFANTIL VIRGEN DEL PILAR - MORALES - SAN MARTIN - SAN MARTIN ESPECIALIDAD: INSTALACIONES SANITARIAS - DRENAJE PLUVIAL		
PLANO: DETALLE CONSTRUCTIVO: JUNTA DE DILATACION E=1" CON SELLADOR Y JUNTAS DE TECNOPOR PARTIDAS 01.04.04.06.01 y 01.04.04.06.02 - 17 JUNTAS DE DILATACION CADA 4.00 m - ESC. INDICADAS		
PROYECTISTA: _____ CIP: _____		
ELABORADO: HIDROCONSULT		ESCALA: 1/10
REVISADO: _____		FECHA: OCT. 2026 LAMINA:
FIRMA Y SELLO:		REVISION: 00

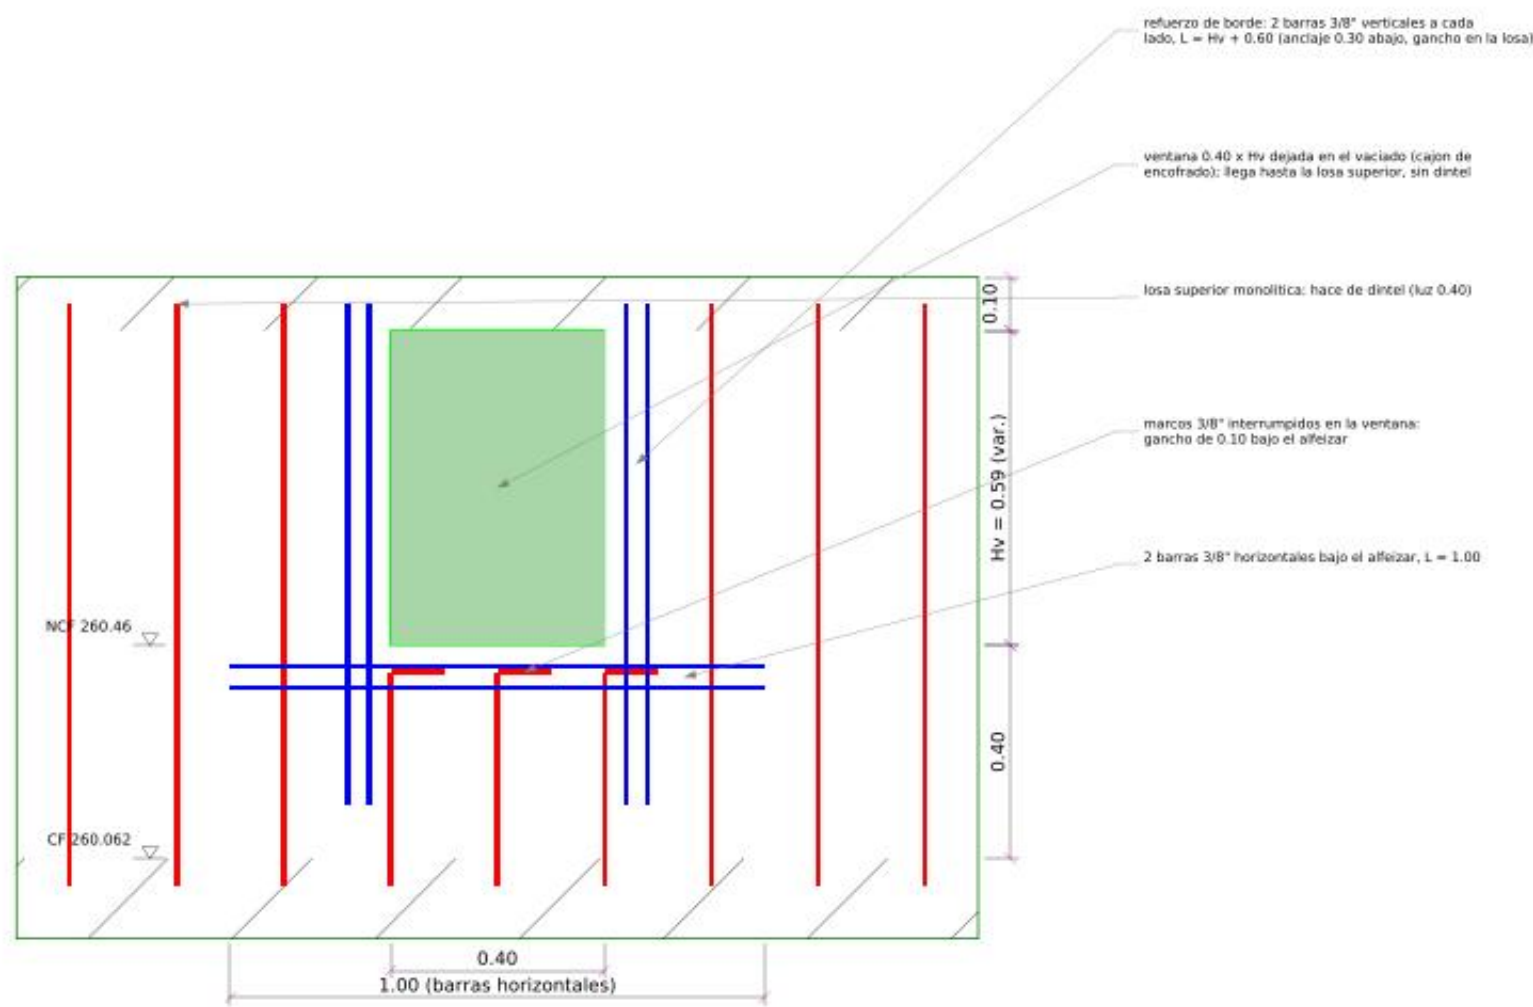

A. VENTANA DE EMPALME - ELEVACION INTERIOR

ESC. 1/10 - ejemplo cuneta Eje 06 (0+046.02); Hv de cada cuneta en el cuadro

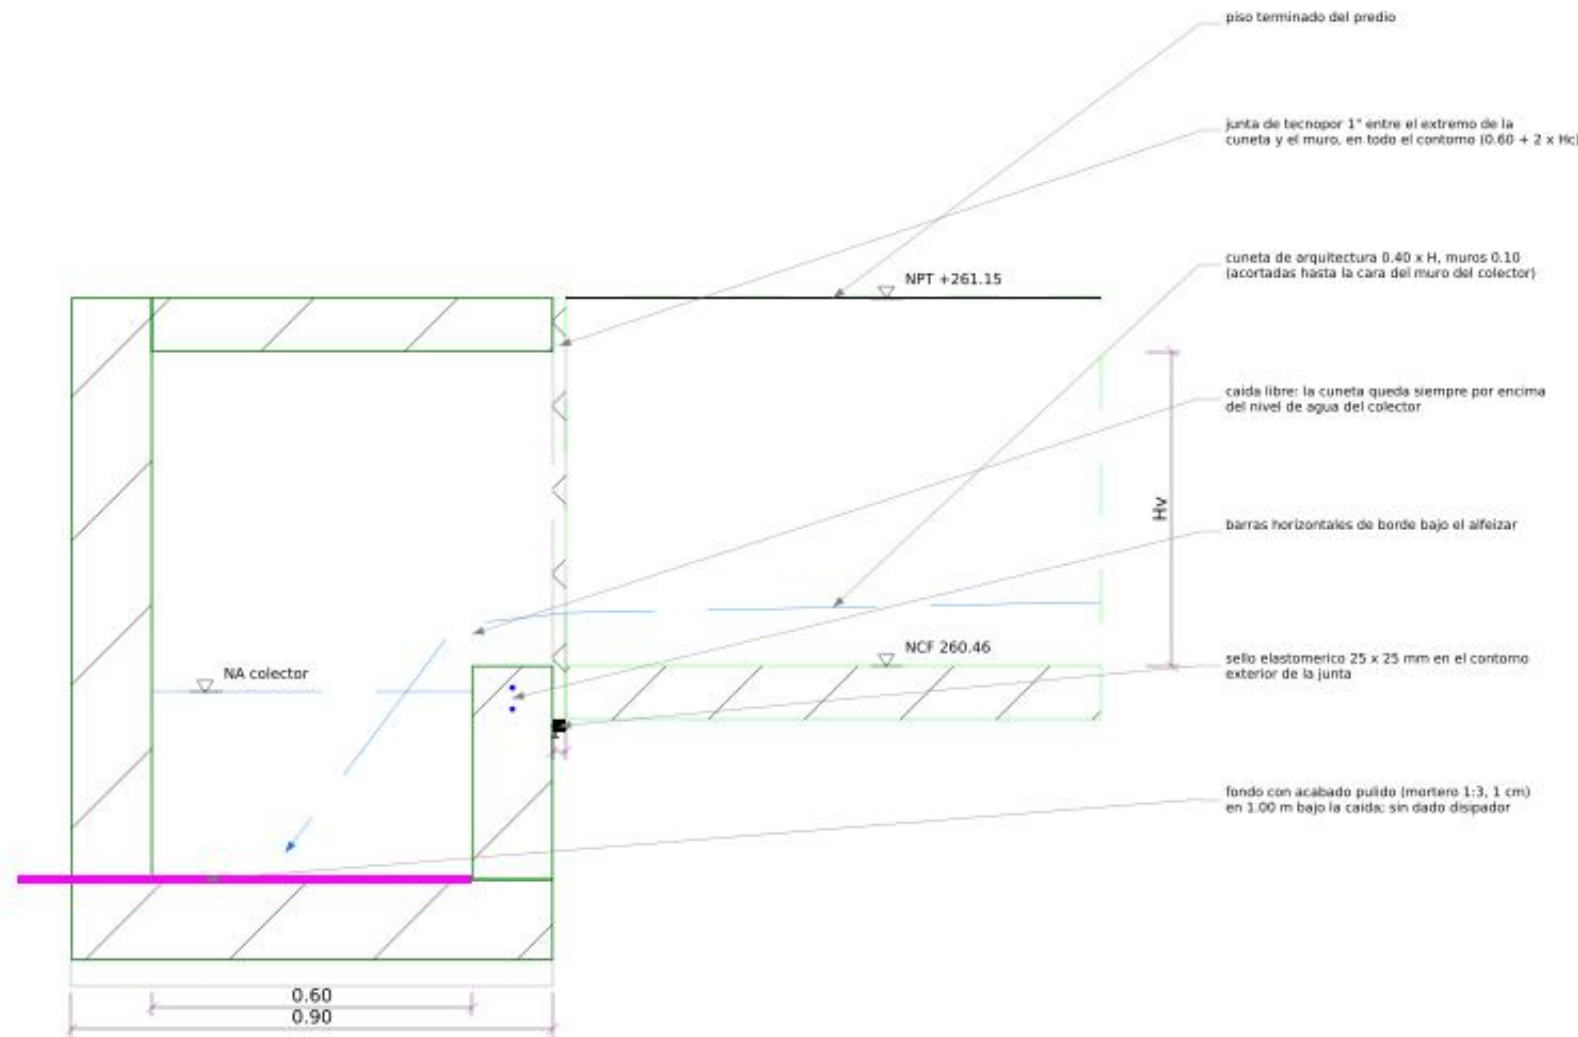

B. CORTE POR EL EMPALME (mirando aguas abajo)

ESC. 1/10 - ejemplo Eje 06; registro de limpieza encima (DD-01 y DD-02)

CUADRO DE EMPALMES: DIMENSIONES Y COMPONENTES POR CUNETA (DP-06C)


CUNETA	PROG.	NCF LLEGA (msnm)	H CUNETA (m)	Hv VENTANA (m)	ENCOF. CAJON (m2)	ACERO BORDE 3/8" (kg)	TECNOPOR (m2)	SELLO (m)
Eje 09	0+006.24	260.69	0.56	0.36	0.23	3.27	0.04	1.72
Eje 08	0+019.87	260.65	0.60	0.40	0.24	3.36	0.04	1.80
Eje 06	0+046.02	260.46	0.69	0.59	0.30	3.78	0.05	1.98
Eje 04	0+078.33	260.44	0.73	0.61	0.30	3.84	0.05	2.06

CUADRO DE COMPONENTES POR EMPALME (promedio) Y TOTAL (4 und)

COMPONENTE	UND	CANT. / UND	x TOTAL	PARTIDA / OBSERVACION
Cajon de encofrado de la ventana 0.40 x Hv x 0.15 (madera, 2 usos)	m2	0.27	1.07	01.04.04.06.03 EMPALME (und)
Refuerzo de borde 3/8": 4 verticales (Hv + 0.60) + 2 horizontales de 1.00	kg	3.56	14.25	01.04.04.06.03 EMPALME (und)
Tecnopor 1" en el contorno de la cuneta (0.60 + 2 x H)	m2	0.04	0.18	01.04.04.06.03 EMPALME (und)
Sello elastomerico 25 x 25 mm en el contorno exterior	m	1.89	7.56	01.04.04.06.03 EMPALME (und)
Acabado pulido del fondo (mortero 1:3, e = 1 cm) 0.60 x 1.00	m2	0.60	2.40	01.04.04.06.03 EMPALME (und)
Perfilado y resane de los bordes de la ventana (mortero 1:3)	m	1.78	7.12	01.04.04.06.03 EMPALME (und)
Registro de limpieza encima del empalme	und	1	4	partidas 01.04.04.05.xx (DD-01 y DD-02)

PROCEDIMIENTO

1. Al armar el muro lado predio, colocar el refuerzo de borde (4 verticales y 2 horizontales) y el cajon de 0.40 x Hv con su fondo en la cota NCF de la cuneta (cuadro).
2. Vaciar el muro y la losa superior monolítica; retirar el cajon a los 2 días, perfilar y resanar los bordes de la ventana.
3. Empalmar la cuneta (o su prolongacion) contra el muro con la plancha de tecnopor de 1" en todo su contorno; sellar el contorno exterior con poliuretano.
4. Pulir el fondo del colector en 1.00 m bajo la caída. Colocar el registro de limpieza sobre el empalme (DD-01 y DD-02).

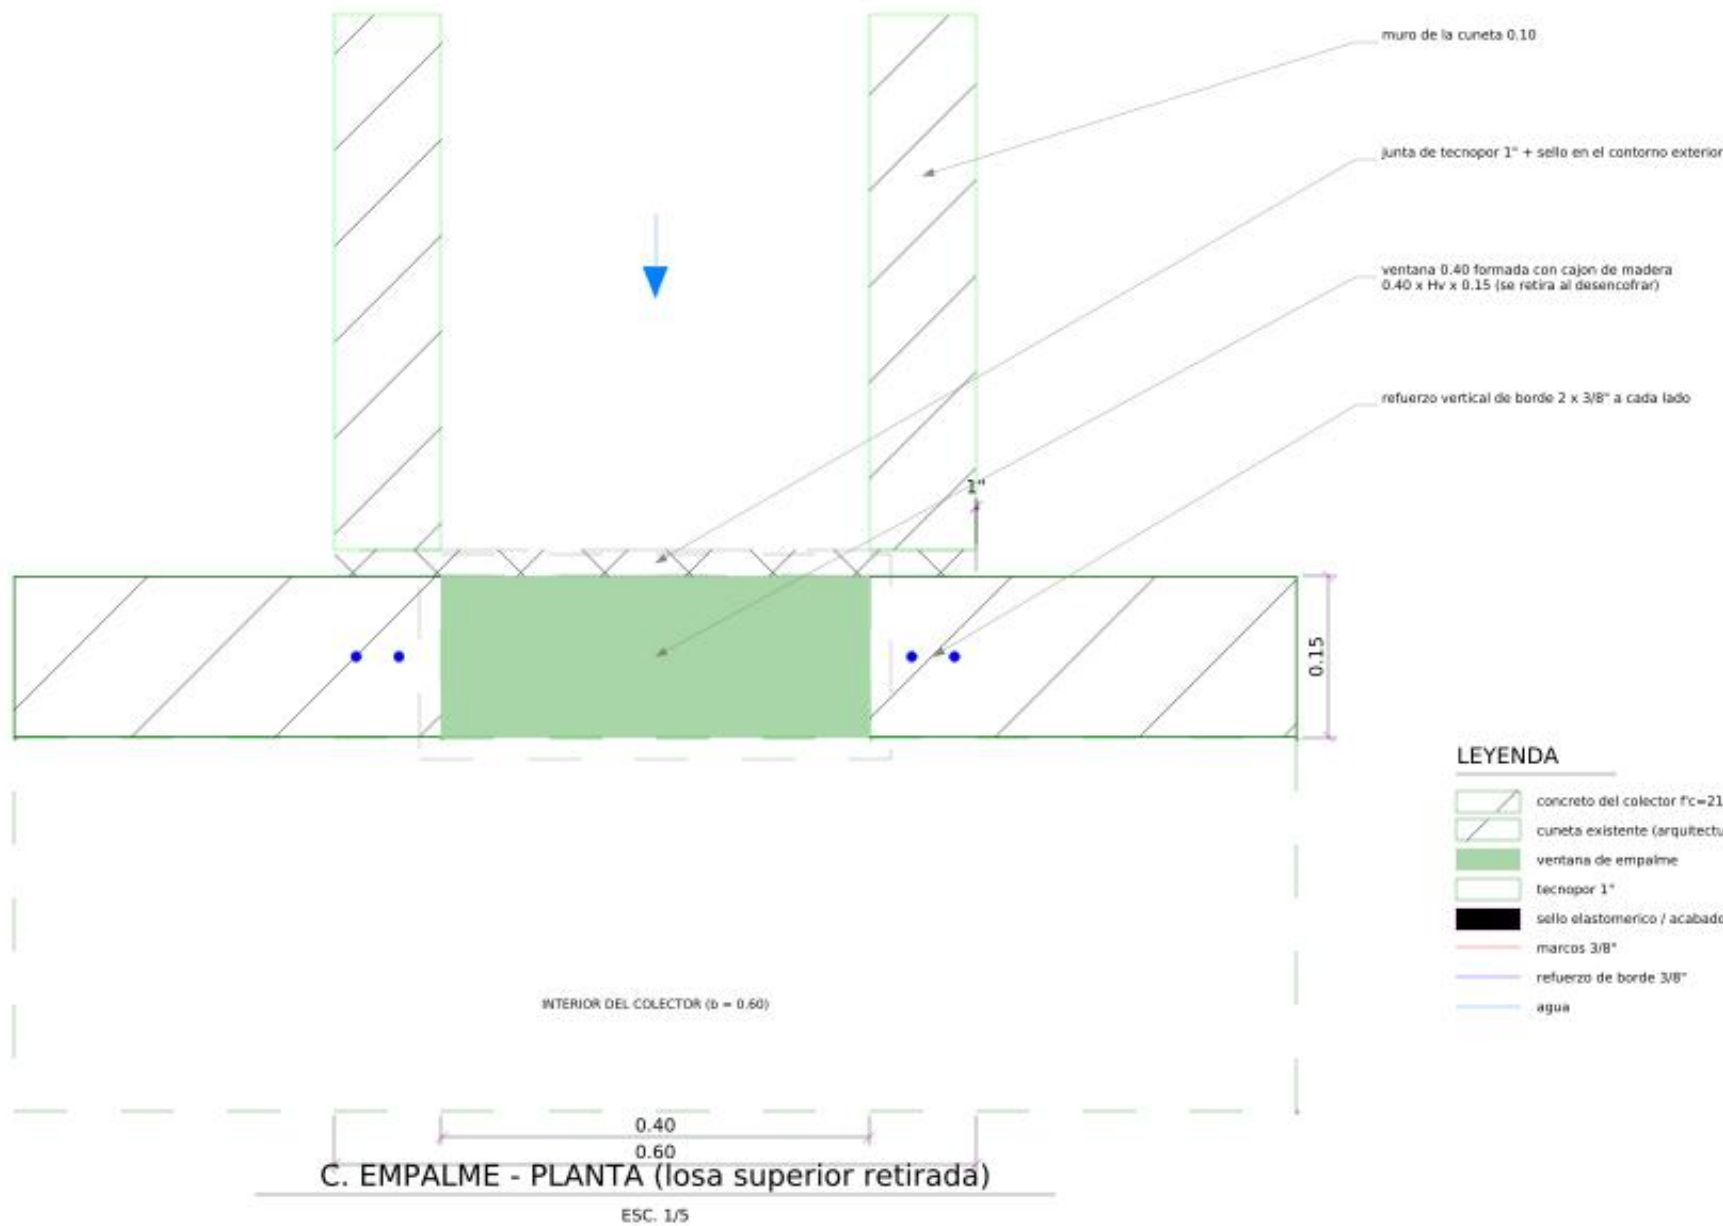

C. EMPALME - PLANTA (losa superior retirada)

ESC. 1/5

PROYECTO: CREACION DEL SERVICIO DE PROTECCION INTEGRAL A NIÑAS, NIÑOS Y ADOLESCENTES SIN CUIDADOS PARENTALES O EN RIESGO DE PERDERLOS EN CENTRO DE ACOGIDA RESIDENCIAL - VARONES, DISTRITO DE MORALES, PROVINCIA Y DEPARTAMENTO DE SAN MARTIN - CLJ N. 2705639 ENTIDAD: GERENCIA TERRITORIAL BAJO MAYO - TARIAPOTO		
UBICACION: PREDIO ALDEA INFANTIL VIRGEN DEL PILAR - MORALES - SAN MARTIN - SAN MARTIN ESPECIALIDAD: INSTALACIONES SANITARIAS - DRENAJE PLUVIAL		
PLANO: DETALLE CONSTRUCTIVO: EMPALME DE CUNETA AL COLECTOR (VENTANA EN MURO Y CAIDA) 4 EMPALMES AL COLECTOR (CUNETAS EJES 09, 08, 06 Y 04) - LA CUNETA DEL EJE 01 ENTRA A LA CAJA CL (DP-07) - ESC. INDICADAS		
PROYECTISTA: _____ CIP: _____		
ELABORADO: HIDROCONSULT	ESCALA: 1/10	
REVISADO: _____	FECHA: OCT. 2026	LAMINA: _____
FIRMA Y SELLO: _____	REVISION: 00	DD-04